DATA FOR "MARITIME TERRESTRIAL ZONE LIMIT"

COURSE	BEARING	DISTANCE	POINT	NORTHING	EASTING	DESCRIPTION
	–	–	16s	261559.1958	275189.8219	STEEL-ROD W/ 3"ø PVC PIPE
16s–17s	N20°32'13"W	20.8612	17s	261578.7312	275182.5036	
17s–18s	S85°20'05"W	31.1254	18s	261576.1996	275151.4813	
18s–19s	N53°45'29"W	46.1214	19s	261603.4664	275114.2830	
19s–20s	N63°46'17"W	20.0860	20s	261612.3435	275096.2651	
20s–21s	S75°27'55"W	39.0654	21s	261602.5395	275058.4500	
21s–22s	S62°23'41"W	9.7048	22s	261598.0425	275049.8500	
22s–23s	N43°35'51"W	12.4106	23s	261607.0303	275041.2918	
23s–24s	N66°08'08"W	28.3284	24s	261618.4913	275015.3853	
24s–25s	S64°55'04"W	13.6221	25s	261612.7166	275003.0478	
25s–26s	S85°47'34"W	40.5382	26s	261609.7426	274962.6189	
26s–27s	S64°43'45"W	28.0638	27s	261597.7622	274937.2408	
27s–28s	N86°10'36"W	9.1527	28s	261598.3725	274928.1085	
28s–29s	N80°37'17"W	40.4286	29s	261604.9607	274888.2203	
29s–30s	S70°17'31"W	33.4460	30s	261593.6817	274856.7334	
30s–31s	S84°37'19"W	17.2824	31s	261592.0619	274839.5271	
31s–596	N02°03'34"E	6.0509	596	261598.1089	274839.7446	
596–622	N09°24'40"E	23.6088	622	261621.4000	274843.6050	
622–624	N41°04'17"E	24.2223	624	261639.6610	274859.5190	
624–623	N66°59'55"E	58.2781	623	261662.4333	274913.1637	
623–631	N57°02'42"E	53.1875	631	261691.3664	274957.7932	
631–634	N77°10'21"E	48.0983	634	261702.0450	275004.6911	
634–637	N84°45'22"E	49.4971	637	261706.5687	275053.9810	
637–640	S86°05'54"E	62.7206	640	261702.3010	275116.5563	
640–643	N84°03'27"E	78.1943	643	261710.3967	275194.3304	
643–646	S86°05'46"E	49.8421	646	261707.0033	275244.0568	
646–649	S63°27'43"E	38.6480	649	261689.7358	275278.6328	
649–652	S51°46'41"E	26.1451	652	261673.5596	275299.1729	
652–655	S37°55'50"E	41.7125	655	261640.6585	275324.8138	STEEL-ROD W/ 3"ø PVC PIPE

DATA FOR "ZONA DE SALVAMENTO"

COURSE	BEARING	DISTANCE	POINT	NORTHING	EASTING	DESCRIPTION
–	–	–	31s	261592.0619	274839.5271	MONUMENTED STEEL-ROD
31s–596	N02°03'34"E	6.0509	596	261598.1089	274839.7446	
596–622	N09°24'40"E	23.6088	622	261621.4000	274843.6050	
622–624	N41°04'17"E	24.2223	624	261639.6610	274859.5190	
624–623	N66°59'55"E	58.2781	623	261662.4333	274913.1637	
623–631	N57°02'42"E	53.1875	631	261691.3664	274957.7932	
631–634	N77°10'21"E	48.0983	634	261702.0450	275004.6911	
634–637	N84°45'22"E	49.4971	637	261706.5687	275053.9810	
637–640	S86°05'54"E	62.7206	640	261702.3010	275116.5563	
640–643	N84°03'27"E	78.1943	643	261710.3967	275194.3304	
643–646	S86°05'46"E	49.8421	646	261707.0033	275244.0568	
646–649	S63°27'43"E	38.6480	649	261689.7358	275278.6328	
649–652	S51°46'41"E	26.1451	652	261673.5596	275299.1729	
652–655	S37°55'50"E	41.7125	655	261640.6585	275324.8138	
655–13L	S61°49'31"W	6.0880	13L	261637.7840	275319.4471	
13L–656	S61°49'31"W	14.2054	656	261631.0767	275306.9249	
656–653	N37°55'50"W	35.8451	653	261659.3498	275284.8907	
653–650	N51°46'41"W	21.6701	650	261672.7573	275267.8663	
650–647	N63°27'43"W	32.5991	647	261687.3222	275238.7019	
647–644	N86°05'46"W	44.1167	644	261690.3258	275194.6875	
644–641	S84°03'27"W	78.1939	641	261682.2302	275116.9138	
641–638	N86°05'54"W	62.8434	638	261686.5062	275054.2160	
638–635	S84°45'22"W	46.5720	635	261682.2498	275007.8390	
635–632	S77°10'21"W	43.2233	632	261672.6535	274965.6944	
632–628	S57°02'42"W	51.3796	628	261644.7039	274922.5820	
628–625	S66°59'55"W	55.4157	625	261623.0501	274871.5720	
625–620	S41°04'17"W	5.4163	620	261618.9668	274868.0135	
619–1s	N70°17'31"E	19.4884	1s	261625.5388	274886.3603	
1s–2s	S80°37'17"E	44.6467	2s	261618.2633	274930.4103	MONUMENTED STEEL-ROD

DATA FOR "ZONA DE SALVAMENTO" (CONTINUATION)

COURSE	BEARING	DISTANCE	POINT	NORTHING	EASTING	DESCRIPTION
2s–3s	S86°10'36"E	2.9925	3s	261618.0637	274933.3961	MONUMENTED STEEL-ROD
3s–4s	N64°43'45"E	26.5922	4s	261629.4159	274957.4434	
4s–5s	N85°47'34"E	40.5722	5s	261632.3924	274997.9062	
5s–6s	N64°55'04"E	19.0412	6s	261640.4644	275015.1518	
6s–7s	[illegible]	41.4169	7s	261623.7081	275053.0278	
7s–8s	[illegible]	[illegible]	8s	261622.1737	275054.4888	
8s–9s	[illegible]	[illegible]	9s	261633.5683	275098.4387	
9s–10s	S63°46'17"E	29.2688	10s	261620.6328	275124.6939	
10s–11s	S53°45'29"E	40.4143	11s	261596.7400	275157.2891	
11s–12s	N85°20'05"E	38.7724	12s	261599.8936	275195.9331	
12s–13s	S20°32'13"E	25.1411	13s	261576.3503	275204.7528	
13s–14s	S61°49'31"W	11.0712	14s	261571.1228	275194.9934	
14s–15s	S23°26'29"W	4.3593	15s	261567.1234	275193.2593	
15s–16s	S23°26'29"W	8.6407	16s	261559.1958	275189.8219	
16s–17s	N20°32'13"W	20.8612	17s	261578.7312	275182.5036	
17s–18s	S85°20'05"W	31.1254	18s	261576.1996	275151.4813	
18s–19s	N53°45'29"W	46.1214	19s	261603.4664	275114.2830	
19s–20s	N63°46'17"W	20.0860	20s	261612.3435	275096.2651	
20s–21s	S75°27'55"W	39.0654	21s	261602.5395	275058.4500	
21s–22s	S62°23'41"W	9.7048	22s	261598.0425	275049.8500	
22s–23s	N43°35'51"W	12.4106	23s	261607.0303	275041.2918	
23s–24s	N66°08'08"W	28.3284	24s	261618.4913	275015.3853	
24s–25s	S64°55'04"W	13.6221	25s	261612.7166	275003.0478	
25s–26s	S85°47'34"W	40.5382	26s	261609.7426	274962.6189	
26s–27s	S64°43'45"W	28.0638	27s	261597.7622	274937.2408	
27s–28s	N86°10'36"W	9.1527	28s	261598.3725	274928.1085	
28s–29s	N80°37'17"W	40.4286	29s	261604.9607	274888.2203	
29s–30s	S70°17'31"W	33.4460	30s	261593.6817	274856.7334	
30s–31s	S84°37'19"W	17.2824	31s	261592.0619	274839.5271	MONUMENTED STEEL-ROD

AREA= 18,098.5887 Mts. ≎ 4.6048 Cuerdas

CONTROL STATIONS

STATION	COORDINATES NORTHING	COORDINATES EASTING	ELEVATION	DESCRIPTION
STA-PLB1	261477.6900	275353.3790	1.87	PK-NAIL
STA-PLB2	261533.7452	275263.9235	1.30	PK-NAIL

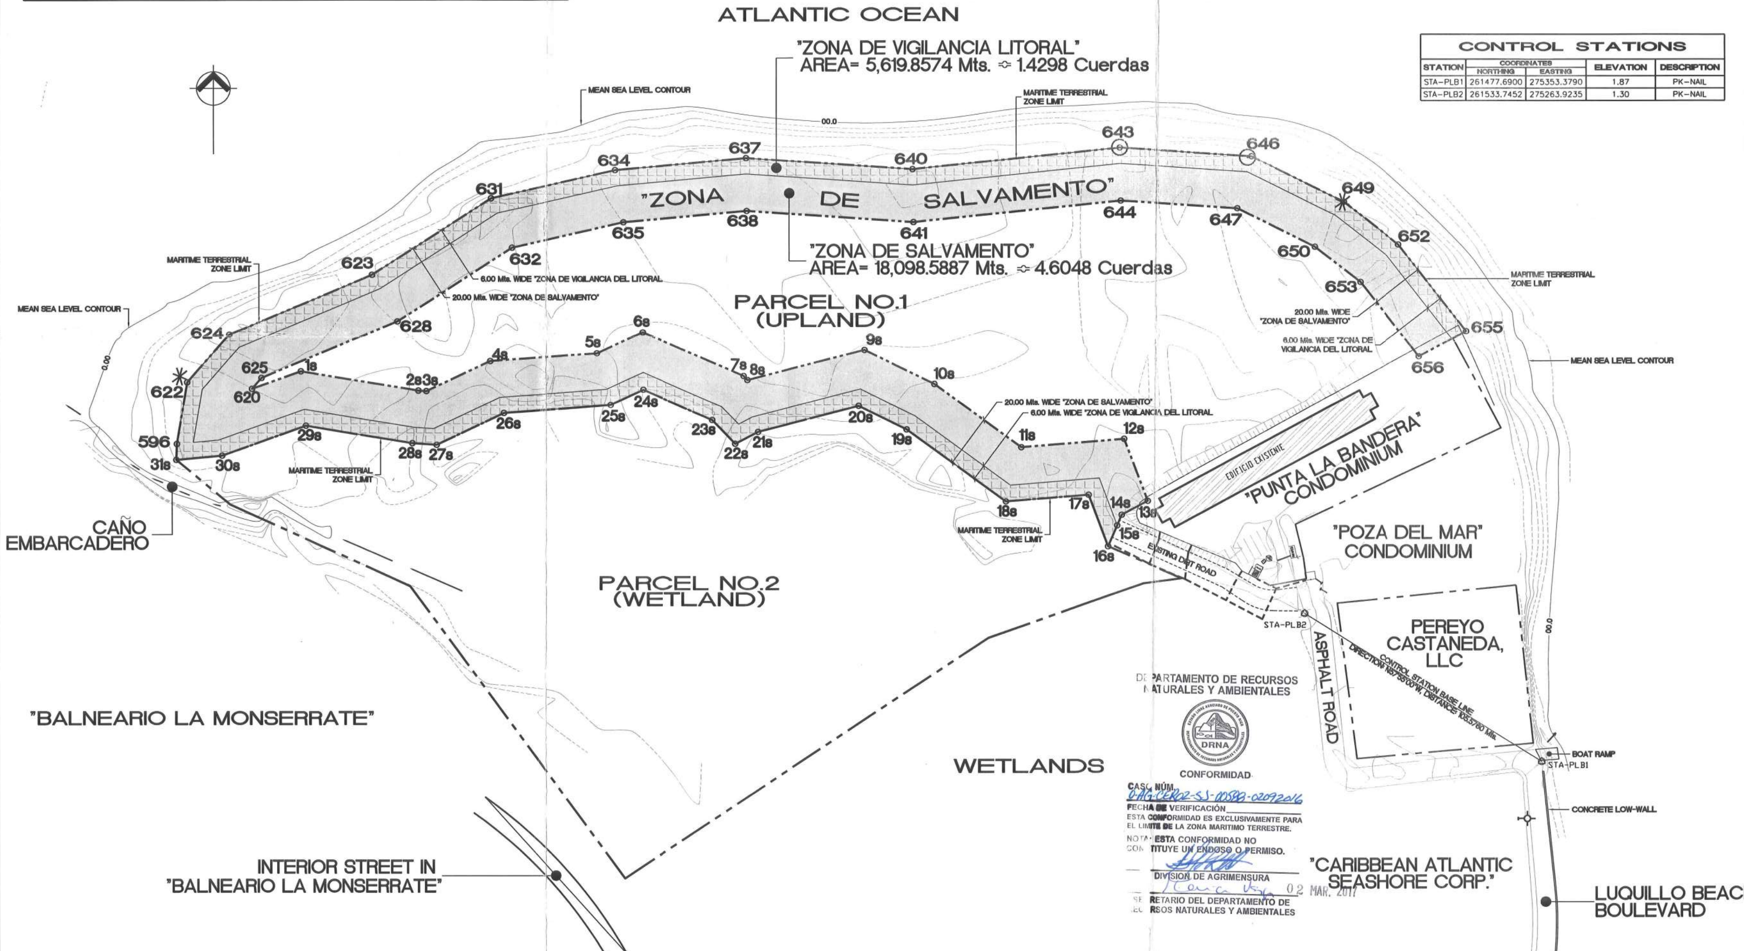
ATLANTIC OCEAN
"ZONA DE VIGILANCIA LITORAL"
AREA= 5,619.8574 Mts. ≎ 1.4298 Cuerdas
"ZONA DE SALVAMENTO"
"ZONA DE SALVAMENTO"
AREA= 18,098.5887 Mts. ≎ 4.6048 Cuerdas
MEAN SEA LEVEL CONTOUR
MARITIME TERRESTRIAL ZONE LIMIT
6.00 Mts. WIDE "ZONA DE VIGILANCIA DEL LITORAL"
20.00 Mts. WIDE "ZONA DE SALVAMENTO"
00.0
0.00
596
31s
30s
622
620
625
624
1s
29s
28s
27s
2s
3s
623
628
4s
26s
631
632
5s
6s
25s
24s
634
635
637
638
7s
8s
23s
22s
21s
640
641
9s
20s
19s
10s
643
644
646
647
649
650
653
652
655
656
11s
12s
13s
14s
15s
16s
17s
18s
PARCEL NO.1
(UPLAND)
PARCEL NO.2
(WETLAND)
CAÑO EMBARCADERO
"BALNEARIO LA MONSERRATE"
INTERIOR STREET IN
"BALNEARIO LA MONSERRATE"
WETLANDS
EDIFICIO EXISTENTE
"PUNTA LA BANDERA"
CONDOMINIUM
EXISTING DIRT ROAD
"POZA DEL MAR"
CONDOMINIUM
PEREYO
CASTANEDA,
LLC
ASPHALT ROAD
STA-PLB2
STA-PLB1
CONTROL STATION BASE LINE
DIRECTION N57°35'00"W, DISTANCE 105.5760 Mts.
BOAT RAMP
CONCRETE LOW-WALL
"CARIBBEAN ATLANTIC
SEASHORE CORP."
LUQUILLO BEACH
BOULEVARD
"LA ESMERALDA"
CONDOMINIUM

DEPARTAMENTO DE RECURSOS NATURALES Y AMBIENTALES

DRNA

CONFORMIDAD

CASO NÚM. 0-AG-CER02-SJ-00598-02092016

FECHA DE VERIFICACIÓN

ESTA CONFORMIDAD ES EXCLUSIVAMENTE PARA EL LIMITE DE LA ZONA MARITIMO TERRESTRE.

NOTA: ESTA CONFORMIDAD NO CONSTITUYE UN ENDOSO O PERMISO.

DIVISION DE AGRIMENSURA

02 MAR. 2017

SECRETARIO DEL DEPARTAMENTO DE RECURSOS NATURALES Y AMBIENTALES

ORIGINAL REGISTRATION NOTES:

1– THE SITE IS REGISTERED IN THE MUNICIPALITY OF FAJARDO:

A. PROPERTY NUMBER: NO.1: 4,969 & NO.2: 5722.

B. PAGE: NO.1: 223 & NO.2: 159.

LEGEND:

STA-1 CONTROL STATION

100 CONTOUR LINES (EVERY 0.25 METER)

▦ 6.00 Mts. WIDE "ZONA DE VIGILANCIA LITORAL"

GRAPHIC SCALE

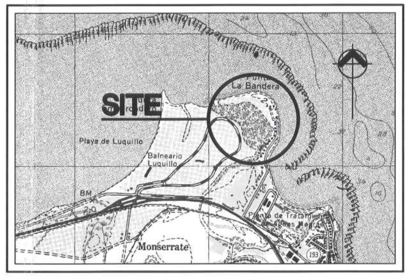
SITE
La Bandera
Playa de Luquillo
Balneario Luquillo
BM
Monserrate
193

LOCATION PLAN

SCALE 1:20,000

SITE
Monserrate
Solmar
Costa Azul
N

AERIAL MAP

NTS

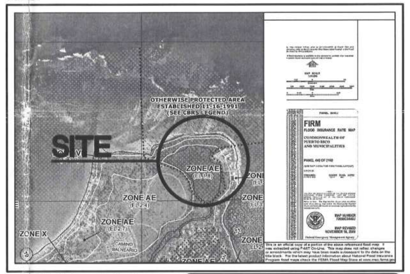
SITE
OTHERWISE PROTECTED AREA ESTABLISHED 11-16-1991 (SEE CBRS LEGEND)
ZONE AE
ZONE X
FIRM

FEMA MAP

NTS

MAP NUMBER: 72000C0440J
MAP REVISED DATE: NOVEMBER 18, 2009
PANEL: 0440J

NOTES:

1– DIMENSIONS AND/OR ELEVATIONS ARE SHOWN IN METRIC SYSTEM, UNLESS OTHERWISE NOTED.

2– HORIZONTAL CONTROLS ARE REFERRED TO THE PUERTO RICO LAMBERT COORDINATE SYSTEM (NAD–83 2011 ED REV).

3– ELEVATIONS ARE REFERRED TO MEAN SEA LEVEL (M.S.L.) SYSTEM.

4– THE EQUIPMENT USED TO OBTAIN FIELD DATA WAS:
A – SOUTH S82–2013 RTK–GNSS BASE AND ROVER.
B – GETAC PS336 DATA COLLECTOR.

5– FIELD JOB WAS PERFORMED ON AUGUST, 2016.

6– THIS PLAN IS BASED ON INFORMATION INCLUDED IN THE "SURVEY AND TOPOGRAPHIC PLAN", DATED DECEMBER, 1998 AND PREPARED BY PCM SURVEYING SERVICES, PRIMITIVO COLON MARTINEZ PLS., LIC. NO.7507.

7– SYMBOLS SHOWN ARE FOR ILLUSTRATION PURPOSES ONLY. THEY ARE NOT, NECESSARILY, OF THE SAME TYPE AND/OR SIZE OF THE OBJECT WHICH THEY REPRESENT.

8– FOR MARITIME TERRESTRIAL ZONE LIMIT MONUMENTATION PHOTOS, PLEASE REFER TO DWG. MTZP–1

SURVEY PLAN SHOWING THE DEPARTMENT OF NATURAL & ENVIRONMENTAL RESOURCES "MARITIME

SURVEY PLAN SHOWING THE DEPARTMENT OF NATURAL & ENVIRONMENTAL RESOURCES "MARITIME TERRESTRIAL ZONE LIMIT DELIMITATION"

FOR

"PUNTA LA BANDERA"

INTERIOR STATE ROAD PR-193 & LUQUILLO BEACH BOULEVARD

PUNTA LA BANDERA SECTOR, MATA DE PLATANO WARD

LUQUILLO PUERTO RICO

LAND SURVEYING SERVICES, PSC

ENRIQUE BLANES PALMER
207 DEL PARQUE ST. 4TH FLOOR
SAN JUAN, PUERTO RICO 00912
RPA LIC. 06416

SEAL:

ENRIQUE BLANES PALMER
INGENIERO LICENCIADO
LIC. #6416
PUERTO RICO

CERTIFICATION:
I, ENRIQUE BLANES PALMER, WITH LICENSE NUMBER 6416, CERTIFY THAT I AM THE PROFESSIONAL THAT PREPARED THESE PLANS AND THE COMPLEMENTARY SPECIFICATIONS. IN ADDITION, I CERTIFY THAT, BASED ON THE BEST OF MY KNOWLEDGE, INFORMATION AND UNDERSTANDING, IN MY PROFESSIONAL OPINION, SAID PLANS AND SPECIFICATIONS GENERALLY COMPLY WITH THE APPLICABLE DISPOSITIONS OF THE JOINT REGULATION AND AGENCY CODES, REGULATORY AGENCIES OR PUBLIC CORPORATIONS WITH JURISDICTION. I RECOGNIZE THAT ANY FALSE DECLARATION OR FACT FALSIFICATIONS PRODUCE WITHOUT MY CONSENT OR BY NEGLIGENCE, EITHER BY ME, MY AGENTS OR EMPLOYEES, OR BY OTHER PERSONS WITH MY KNOWLEDGE, MAKE ME RESPONSIBLE OF ANY JUDICIAL AND DISCIPLINARY ACTION BY THE "OIGPe" AND OTHER COMPETENT AUTHORITIES, INCLUDING, BUT NOT LIMITED TO, THE TERMINATION OF THE PARTICIPATION IN THE PROFESSIONAL CERTIFICATION PROCEDURES AT "OGPe".

DRAWING TITLE:
SURVEY PLAN SHOWING THE DEPARTMENT OF NATURAL & ENVIRONMENTAL RESOURCES "MARITIME TERRESTRIAL ZONE LIMIT DELIMITATION"

CAD FILE: 16-MM-DNER-WETLAND-REV-Carta-DNER.dwg
DRAWN BY: ROD
SCALE DWG.: 1:1,000m
DATE: AUGUST 25, 2016
REVIEWED BY: C.T.R. / E.B.P.

NO.	DATE	BY	DESCRIPTION
3	DEC-14-2016	ROD	REVISED POINTS NO. 620, 622, 624 Y 625 AS RECOMENDED FROM FIELD INSPECTION VISIT WITH D.N.E.R TECHNICIAN ON NOV. 30 2016
2	OCT-26-2016	ROD	ADDITIONAL "ZONA DE SALVAMENTO" MONUMENT PHOTOS
1	OCT-17-2016	ROD	REVISED PLAN FROM COMMENTS OF LETTER RESIVED FROM THE SURVEYING DIVISION OF D.N.E.R.

REVISIONS

DRAWING No.:

...y Data\MAREMIO-Luquillo\dwg\16-MM-DNER-WETLAND-REV-Carta-DNER.dwg

PNT. NO.596
NTS

PNT. NO.622
NTS

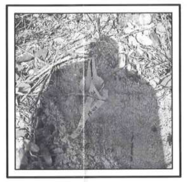
PNT. NO.624
NTS

PNT. NO.623
NTS

PNT. NO.631
NTS

PNT. NO.634
NTS

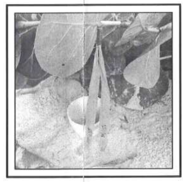
PNT. NO.655
NTS

PNT. NO.1s
NTS

PNT. NO.2s
NTS

PNT. NO.3s
NTS

PNT. NO.4s
NTS

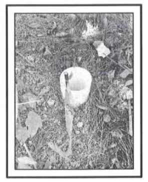
PNT. NO.5s
NTS

PNT. NO.6s
NTS

PNT. NO.7s
NTS

PNT. NO.8s
NTS

PNT. NO.9s
NTS

PNT. NO.10s
NTS

PNT. NO.11s
NTS

PNT. NO.12s
NTS

PNT. NO.13s
NTS

PNT. NO.14s
NTS

PNT. NO.15s
NTS

PNT. NO.16s
NTS

PNT. NO.17s
NTS

PNT. NO.18s
NTS

PNT. NO.19s
NTS

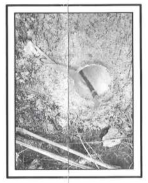
PNT. NO.20s
NTS

PNT. NO.21s
NTS

PNT. NO.22s
NTS

PNT. NO.23s
NTS

PNT. NO.24s
NTS

PNT. NO.25s
NTS

PNT. NO.26s
NTS

PNT. NO.27s
NTS

PNT. NO.28s
NTS

PNT. NO.29s
NTS

PNT. NO.30s
NTS

PNT. NO.31s
NTS

PNT. NO.619
NTS

PNT. NO.620
NTS

PNT. NO.625
NTS

PNT. NO.628
NTS

PNT. NO.632
NTS

PNT. NO.635
NTS

PNT. NO.638
NTS

PNT. NO.641
NTS

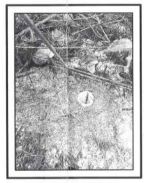
PNT. NO.644
NTS

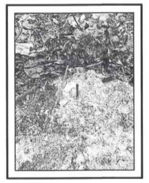
PNT. NO.647
NTS

PNT. NO.650
NTS

PNT. NO.653
NTS

PNT. NO.656
NTS

NOTE:

1– FOR GENERAL NOTES & LOCATION OF MARITIME TERRESTIAL ZONE LIMIT POINT, PLEASE REFER TO DWG. MTZ–1.

SURVEY PLAN SHOWING THE DEPARTMENT OF NATURAL & ENVIRONMENTAL RESOURCES "MARITIME TERRESTRIAL ZONE LIMIT DELIMITATION" POINTS

SCALE 1:1000

SURVEY PLAN SHOWING THE DEPARTMENT OF NATURAL & ENVIRONMENTAL RESOURCES "MARITIME TERRESTRIAL ZONE LIMIT DELIMITATION"
FOR
"PUNTA LA BANDERA"
INTERIOR STATE ROAD PR-193 & LUQUILLO BEACH BOULEVARD
PUNTA LA BANDERA SECTOR, MATA DE PLATANO WARD
LUQUILLO PUERTO RICO

LAND SURVEYING SERVICES, PSC
ENRIQUE BLANES PALMER
207 DEL PARQUE ST. 4TH FLOOR
SAN JUAN, PUERTO RICO 00912

SEAL:
ENRIQUE BLANES PALMER
LIC. #6416

CERTIFICATION:
I, ENRIQUE BLANES PALMER, WITH LICENSE NUMBER 6416, CERTIFY THAT I AM THE PROFESSIONAL THAT DESIGNED THESE PLANS AND THE COMPLEMENTARY SPECIFICATIONS. IN ADDITION, I CERTIFY THAT, BASED ON THE BEST OF MY KNOWLEDGE, INFORMATION AND UNDERSTANDING, IN MY PROFESSIONAL OPINION, SAID PLANS AND SPECIFICATIONS GENERALLY COMPLY WITH THE APPLICABLE DISPOSITIONS OF THE JOINT REGULATION AND AGENCY CODES, REGULATORY AGENCIES OR PUBLIC CORPORATIONS WITH JURISDICTION. I RECOGNIZE THAT ANY FALSE DECLARATION OR FACT FALSIFICATIONS PRODUCE WITHOUT MY CONSENT OR BY NEGLIGENCE, EITHER BY ME, MY AGENTS OR EMPLOYEES, OR BY OTHER PERSONS WITH MY KNOWLEDGE, MAKE ME RESPONSIBLE OF ANY JUDICIAL AND DISCIPLINARY ACTION BY THE "OIGPe" AND OTHER COMPETENT AUTHORITIES, INCLUDING, BUT NOT LIMITED TO, THE TERMINATION OF THE PARTICIPATION IN THE PROFESSIONAL CERTIFICATION PROCEDURES AT "OIGPe".

Survey Data\MAREMIO-Luquillo\dwg\16-MM-DNER-WETLAND-REV-Carta-DNER.dwg

DRAWING TITLE:
SURVEY PLAN SHOWING THE DEPARTMENT OF NATURAL & ENVIRONMENTAL RESOURCES "MARITIME TERRESTRIAL ZONE LIMIT DELIMITATION" POINTS

CAD FILE: 16-MM-DNER-WETLAND-REV-Carta-DNER.dwg
DRAWN BY: ROD
SCALE DWG.: NTS
DATE: AUGUST 25, 2016
REVIEWED BY: C.T.R. / E.B.P.

NO.	DATE	BY	DESCRIPTION
△			
3	DEC-14-2016	ROD	REVISED POINTS NO. 620, 622, 624 Y 625 AS RECOMENDED FROM FIELD INSPECTION VISIT WITH D.N.E.R TECHNICIAN ON NOV. 30 2016
2	OCT-26-2016	ROD	ADDITIONAL "ZONA DE SALVAMENTO" MONUMENT PHOTOS
1	OCT-17-2016	ROD	REVISED PLAN FROM COMMENTS OF LETTER RESIVED FROM THE SURVEYING DIVISION OF D.N.E.R.

REVISIONS

DRAWING No.: