



FED AID H'WAY PROJECT NO.	AC. PROJECT CODE NO.	HIGHWAY P. R. 115	MUNICIPALITY	ISLAND	FISCAL YEAR	SHEET NO.	TOTAL SHEETS
FED CODE	L-005000023 AC-500023	---	RINCON	P.R.	2015	1	11

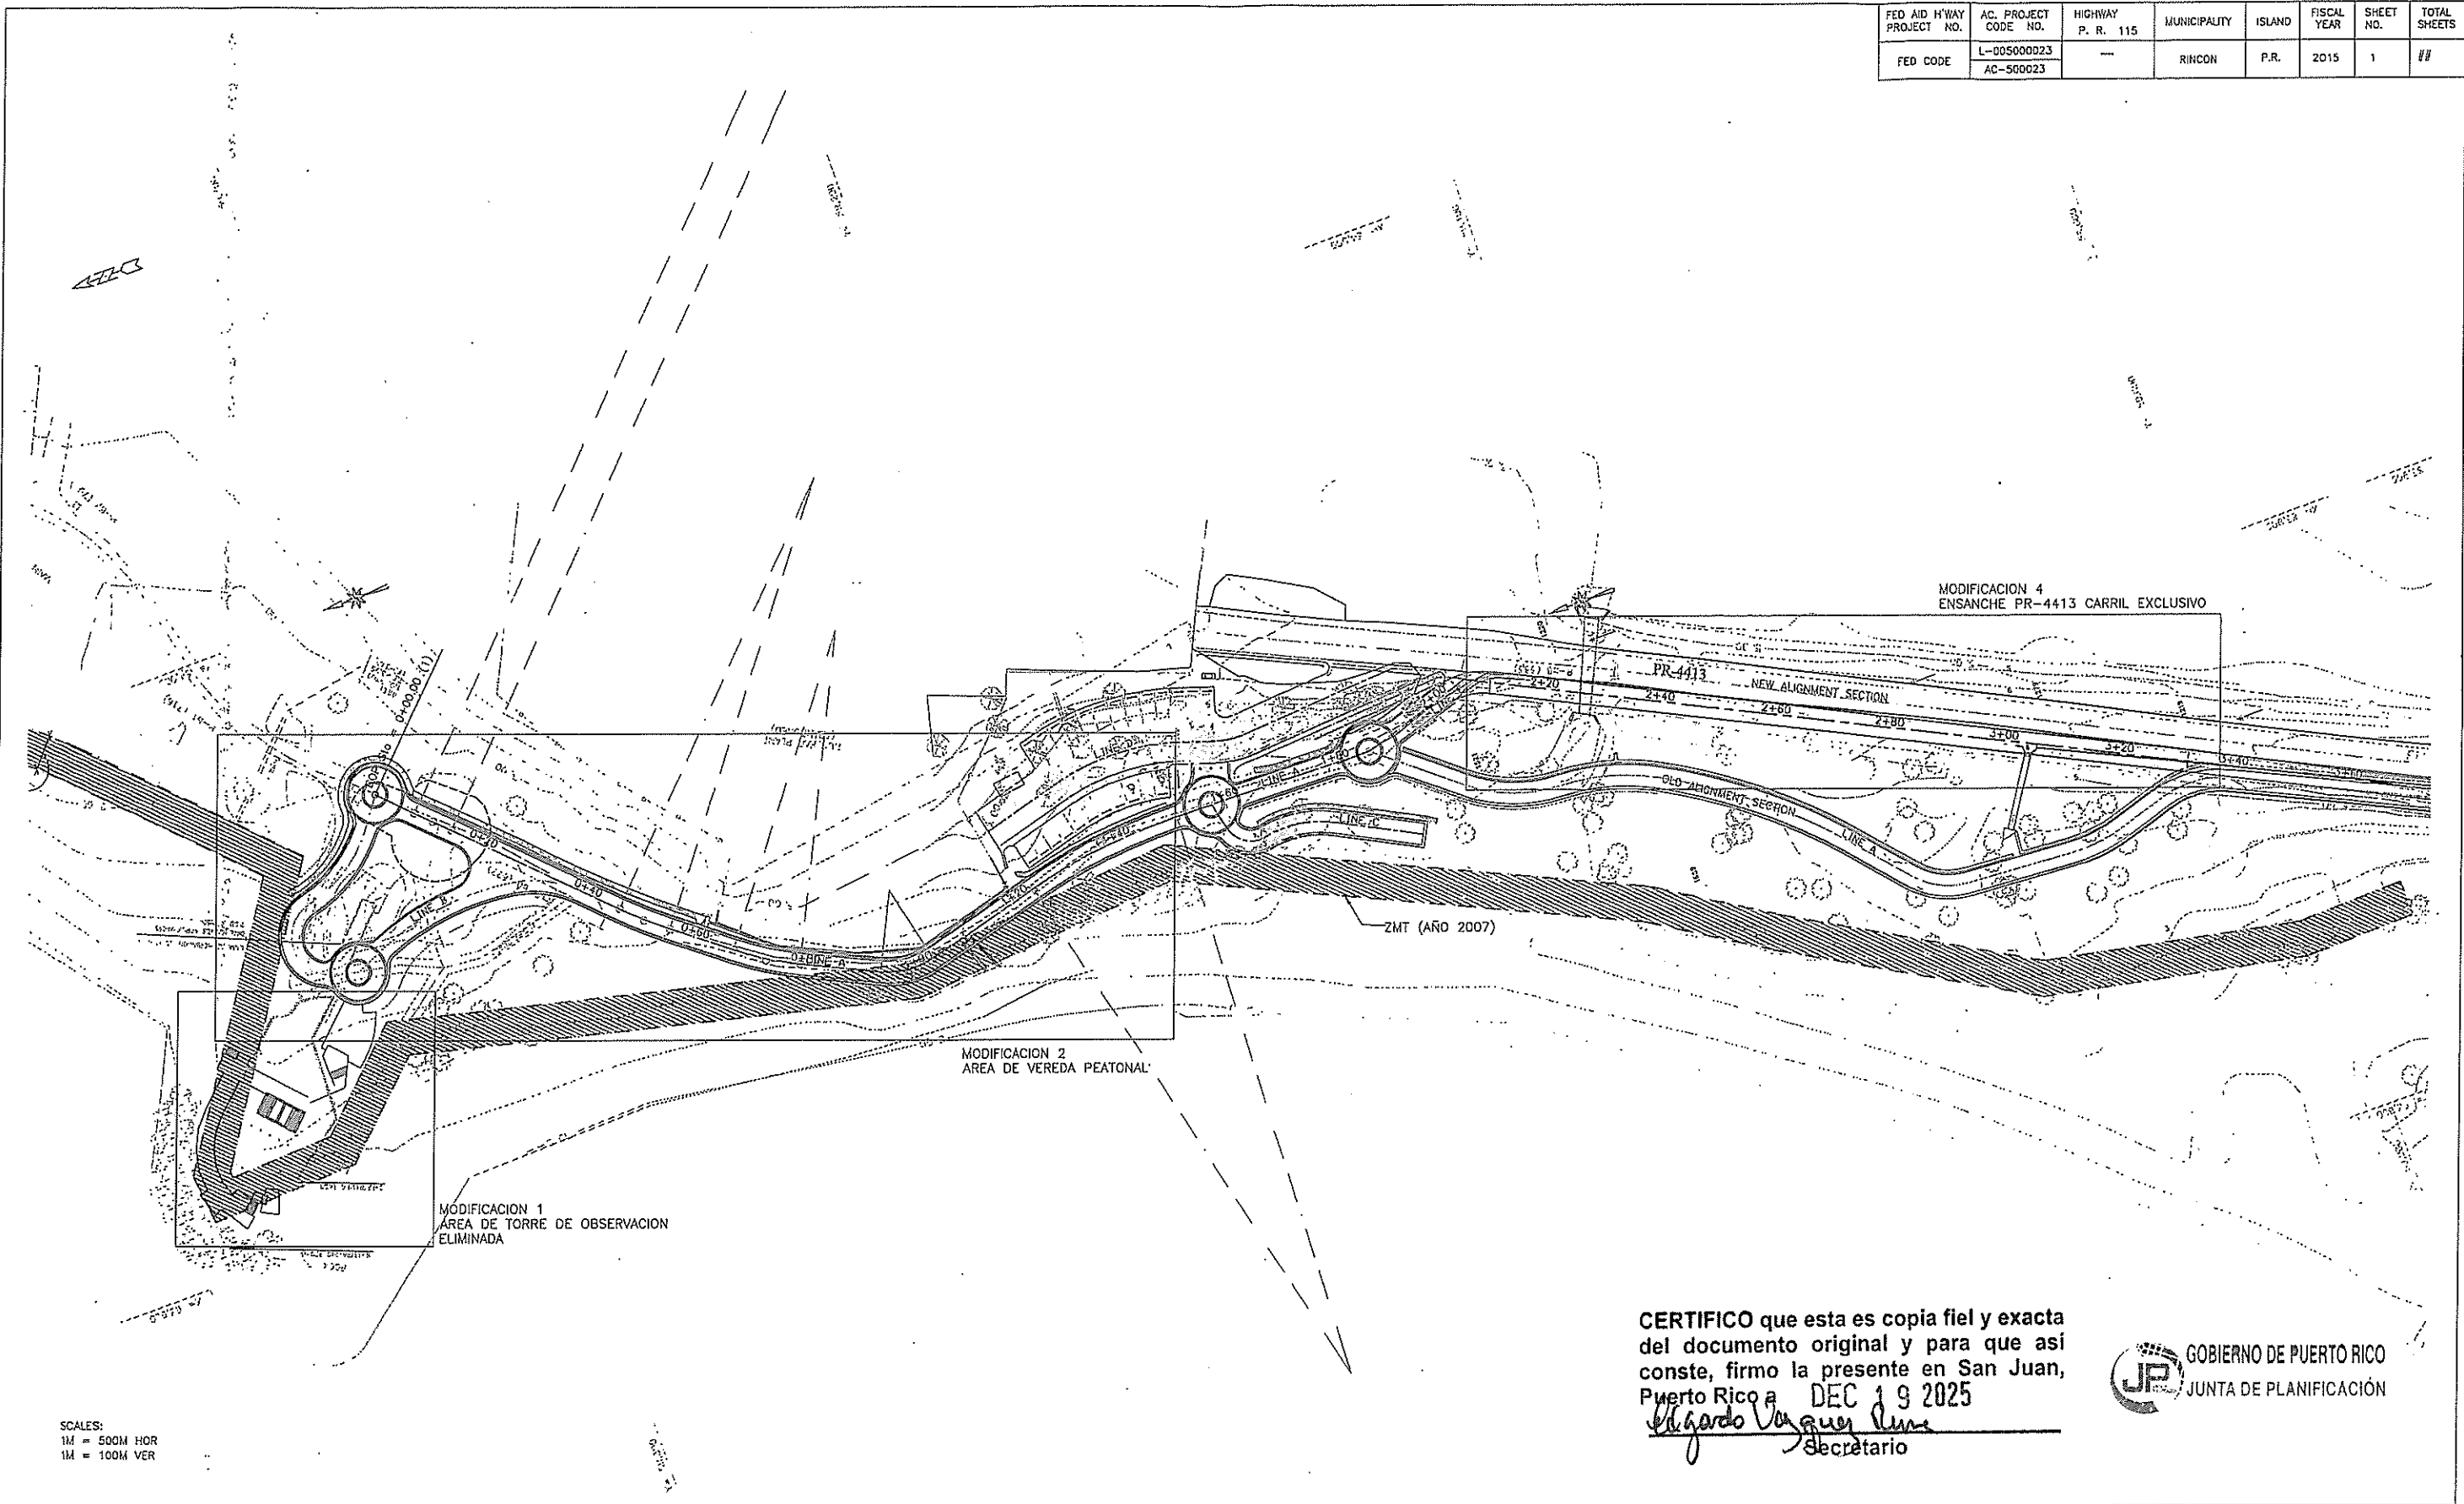

CERTIFICO que esta es copia fiel y exacta del documento original y para que asi conste, firmo la presente en San Juan, Puerto Rico a **DEC 19 2025**
Edgardo Vazquez Luna
Secretario

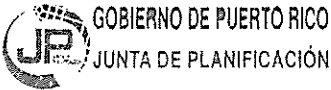

WORK	BY	DATE
DESIGN	AA	AA
DRAWING	AA	AA
TRACED	AA	AA
CHECK	AA	AA
FINAL CHECK	AA	AA

FILE NAME: C:\PROJECTS\RN-500023 TRIANGULACION\CARRETERAS\LOT\RCF25001.DWG

PUERTO RICO HIGHWAY AND TRANSPORTATION AUTHORITY
DESIGN AREA
HIGHWAY DESIGN OFFICE

SCENIC WALK FOR BICYCLE AND
PEDESTRIAN ROUTE
MUNICIPALITY OF RINCON


DATE	REVISIONS

SCALE
1:500

PRELIMINARY CONSTRUCTION PLANS
OLD AND NEW ALIGNMENT COMPARISON

PP
1

FED AID HWAY PROJECT NO.	AC. PROJECT CODE NO.	HIGHWAY P. R. 115	MUNICIPALITY	ISLAND	FISCAL YEAR	SHEET NO.	TOTAL SHEETS
FED CODE	L-005000023 AC-500023	—	RINCON	P.R.	2015	2	##

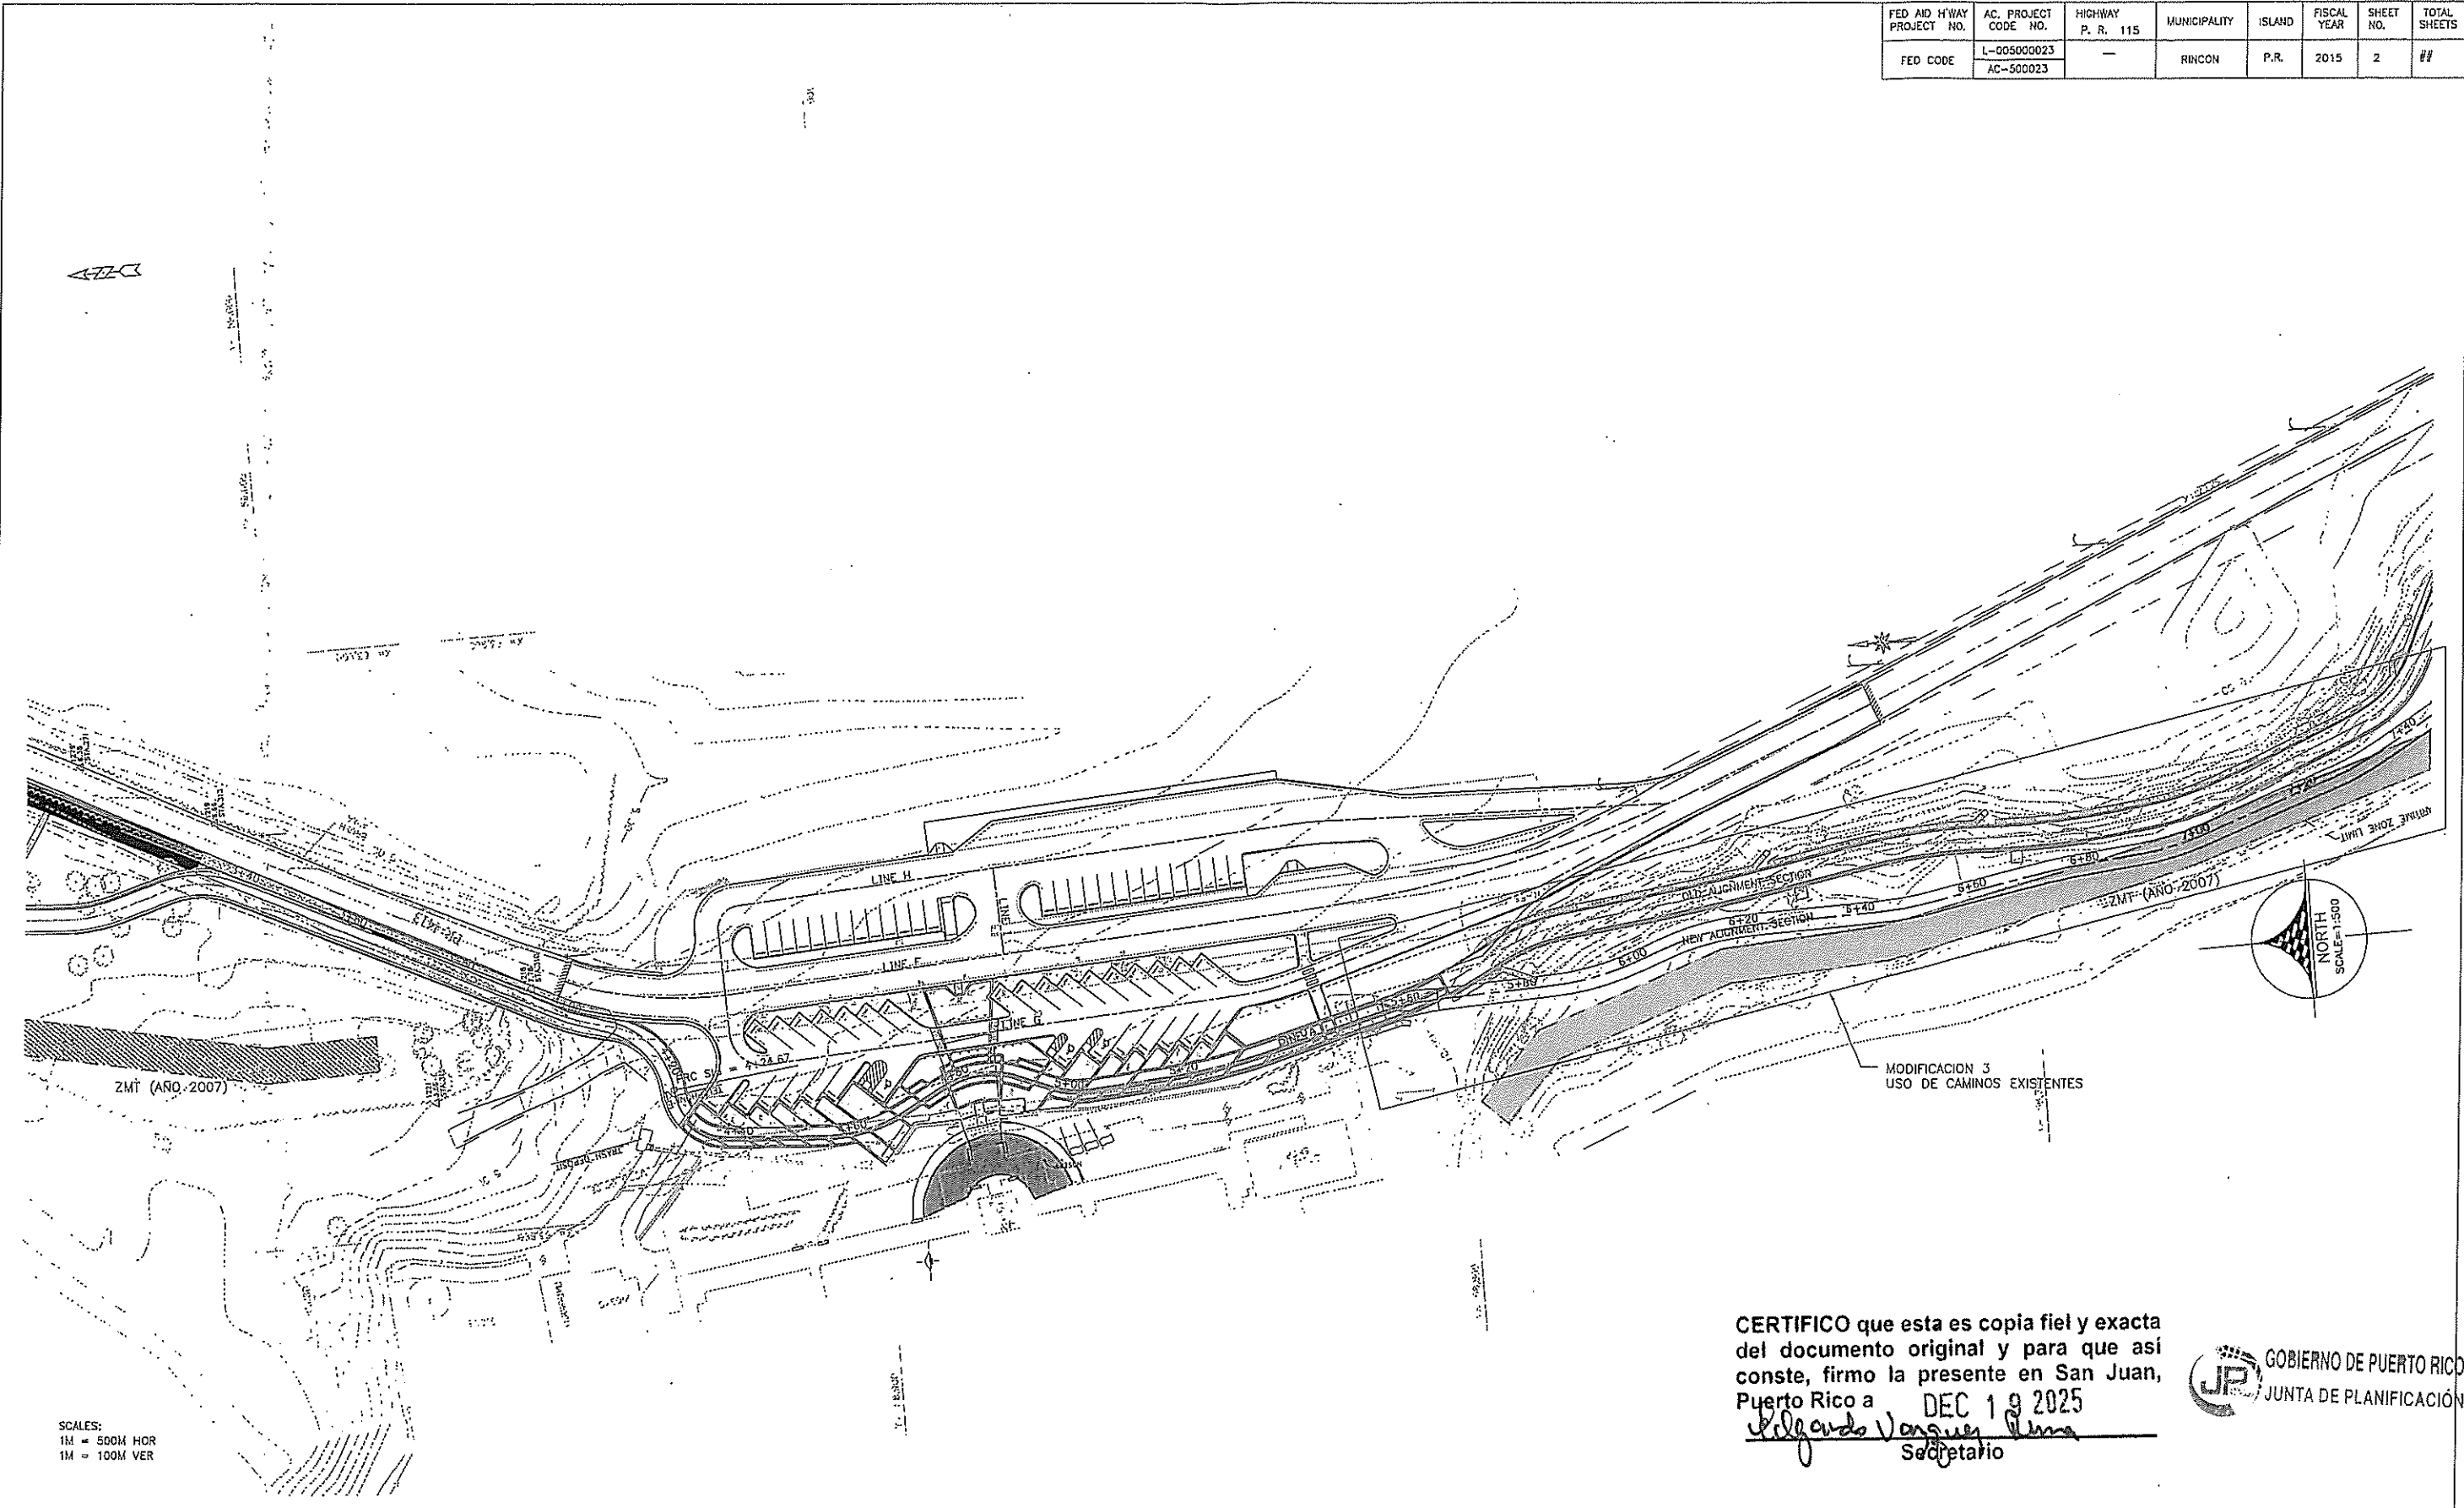

WORK	BY	DATE
DESIGN	AA	AA
DRAWING	AA	AA
REVISION	AA	AA
CHECK	AA	AA
FINAL CHECK	AA	AA

FILE NAME: C:\PROJECTS\VO-500023 TRIANGULACION 500023 TRIANGULACION CARRETERAS\LOT RCP26001.DWG

PUERTO RICO HIGHWAY AND TRANSPORTATION AUTHORITY
DESIGN AREA
HIGHWAY DESIGN OFFICE

SCENIC WALK FOR BICYCLE
AND PEDESTRIAN ROUTE
MUNICIPALITY OF RINCON

DATE	REVISIONS

SCALE
1:500


PRELIMINARY CONSTRUCTION PLAN
OLD AND NEW ALIGNMENT COMPARISON

PP
2

CERTIFICO que esta es copia fiel y exacta
del documento original y para que así
conste, firmo la presente en San Juan,
Puerto Rico a **DEC 19 2025**
Edgardo Vazquez Luna
Secretario

GOBIERNO DE PUERTO RICO
JUNTA DE PLANIFICACIÓN

FED AID H'WAY PROJECT NO.	AC. PROJECT CODE NO.	HIGHWAY P. R. 115	MUNICIPALITY	ISLAND	FISCAL YEAR	SHEET NO.	TOTAL SHEETS
FED CODE	L-005000023 AC-500023	—	RINCON	P.R.	2015	4	##

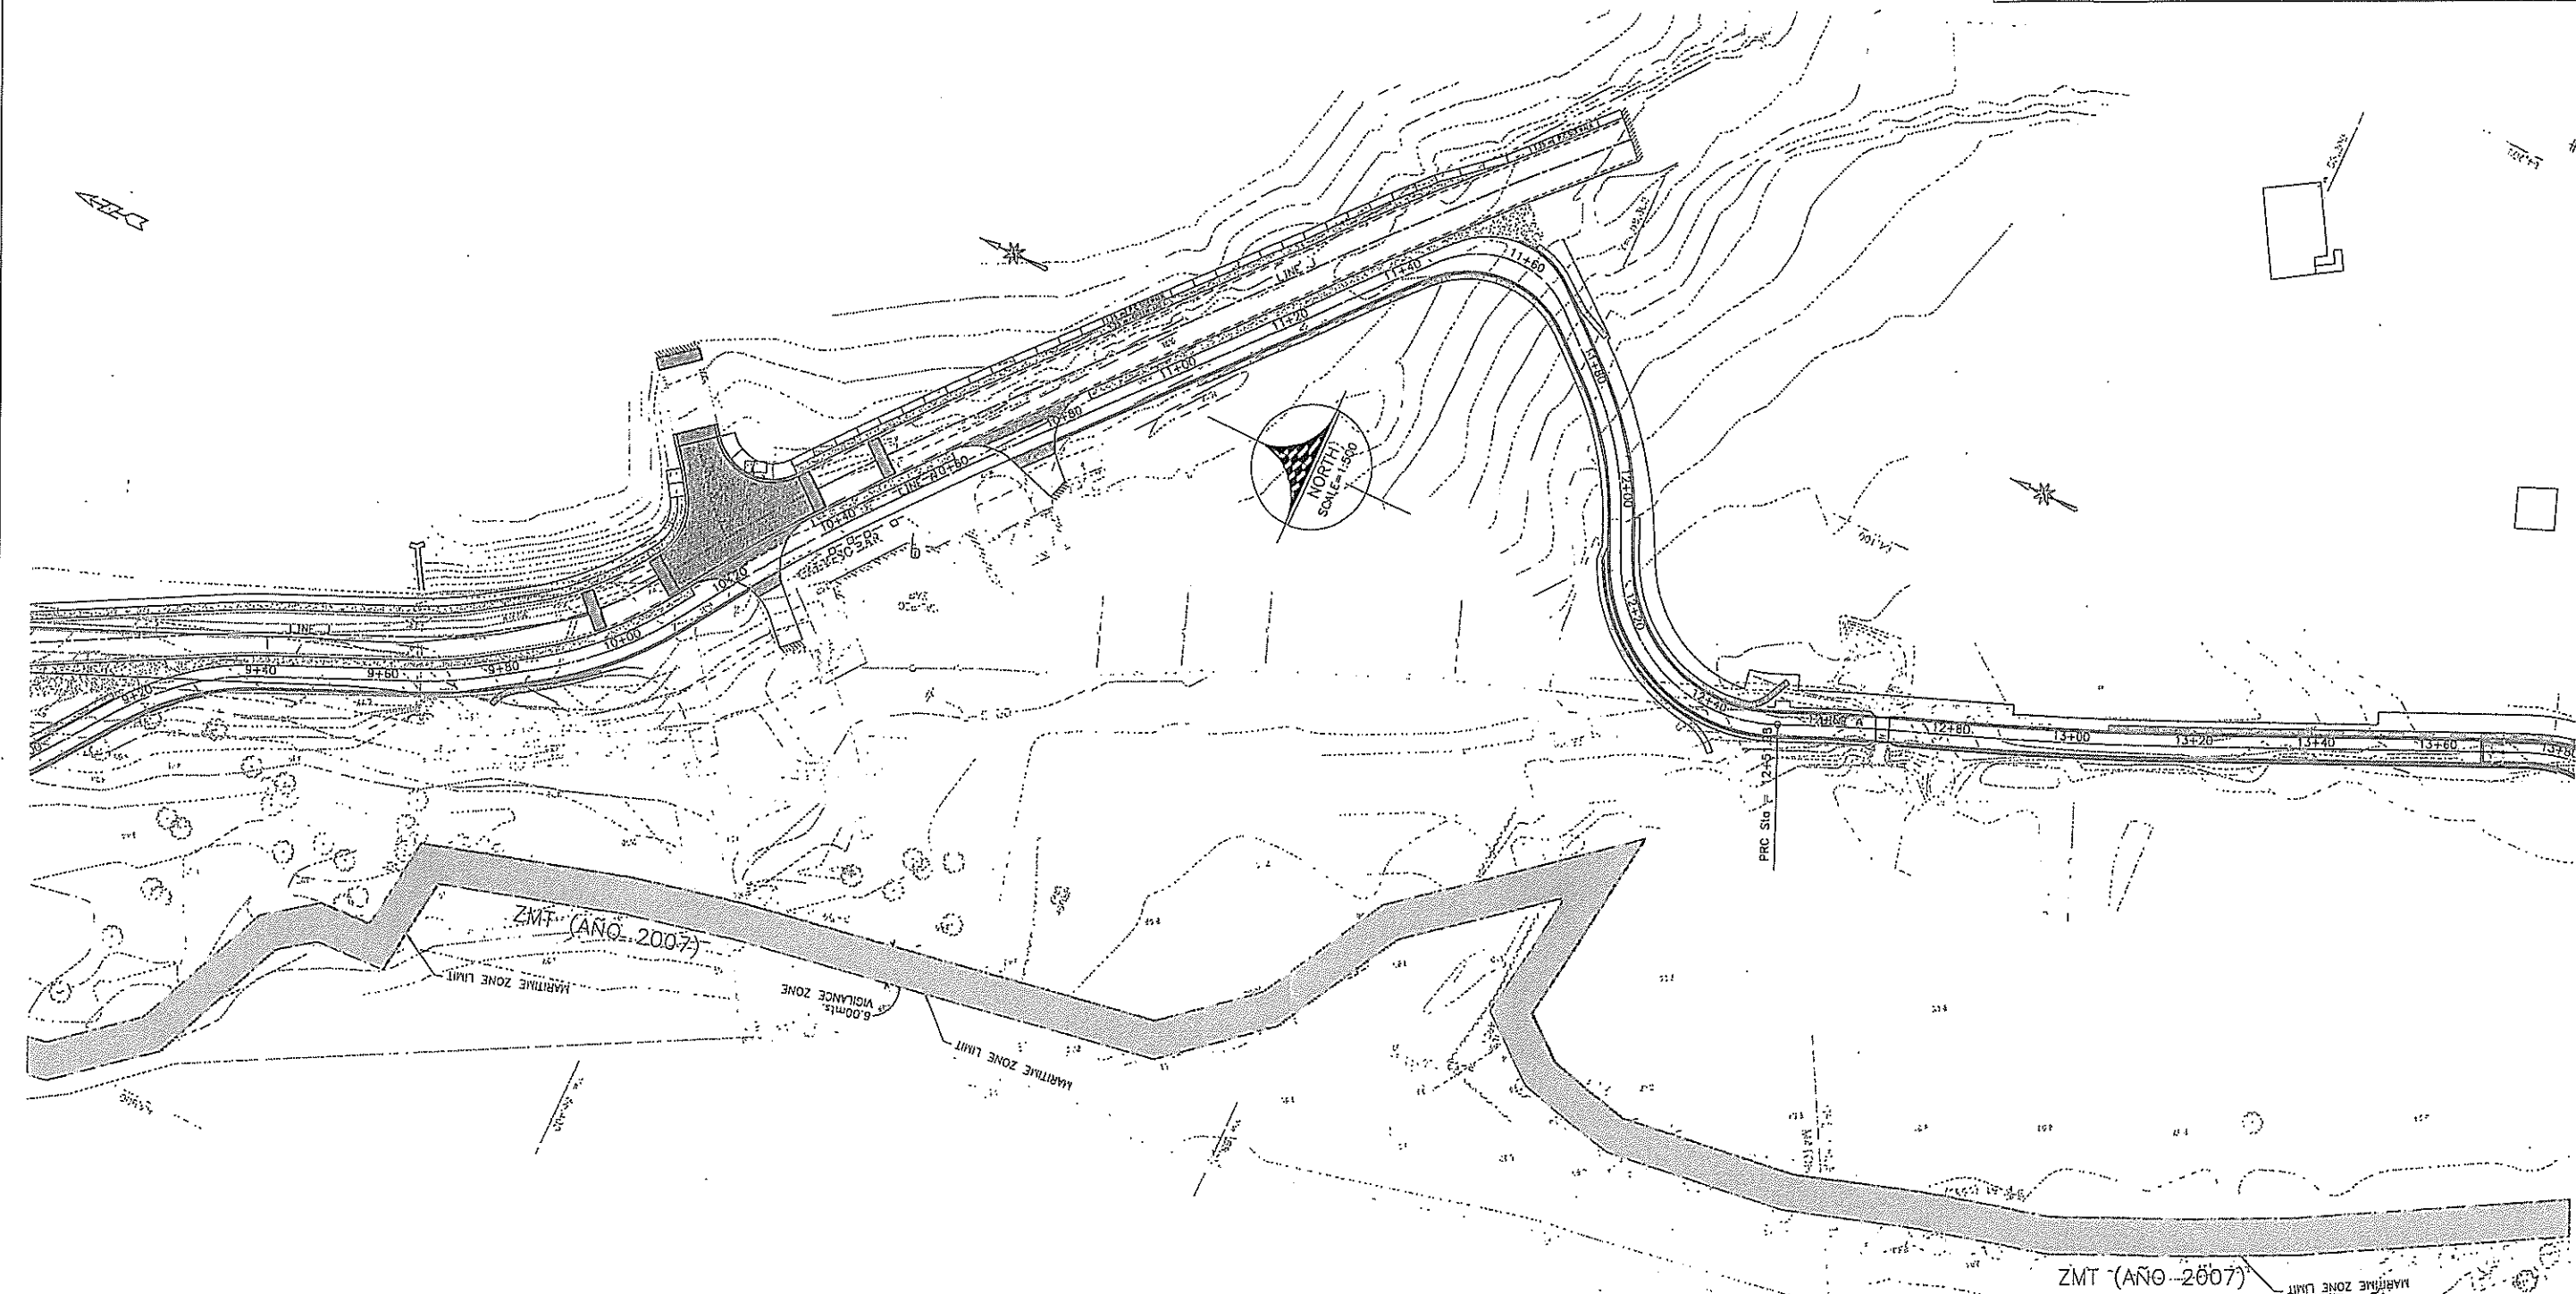

CERTIFICO que esta es copia fiel y exacta del documento original y para que asi conste, firmo la presente en San Juan, Puerto Rico a **DEC 19 2025**
Edgardo Venguez Riera
Secretario

GOBIERNO DE PUERTO RICO
JUNTA DE PLANIFICACIÓN

WORK	BY	DATE
DESIGN	AA	AA
DRAWING	AA	AA
TRACED	AA	AA
CHECK	AA	AA
FINAL CHECK	AA	AA

SCALES:
1M = 500M HOR
1M = 100M VER

PUERTO RICO HIGHWAY AND TRANSPORTATION AUTHORITY
DESIGN AREA
HIGHWAY DESIGN OFFICE

SCENIC WALK FOR BICYCLE AND
PEDESTRIAN ROUTE
MUNICIPALITY OF RINCON


DATE	REVISIONS

SCALE
1:500

PRELIMINARY CONSTRUCTION PLAN
OLD AND NEW ALIGNMENT COMPARISON

PP
4

FED AID H'WAY PROJECT NO.	AC. PROJECT CODE NO.	HIGHWAY P. R. 115	MUNICIPALITY	ISLAND	FISCAL YEAR	SHEET NO.	TOTAL SHEETS
FED CODE	L-005000023 AC-500023	—	RINCON	P.R.	2015	5	##

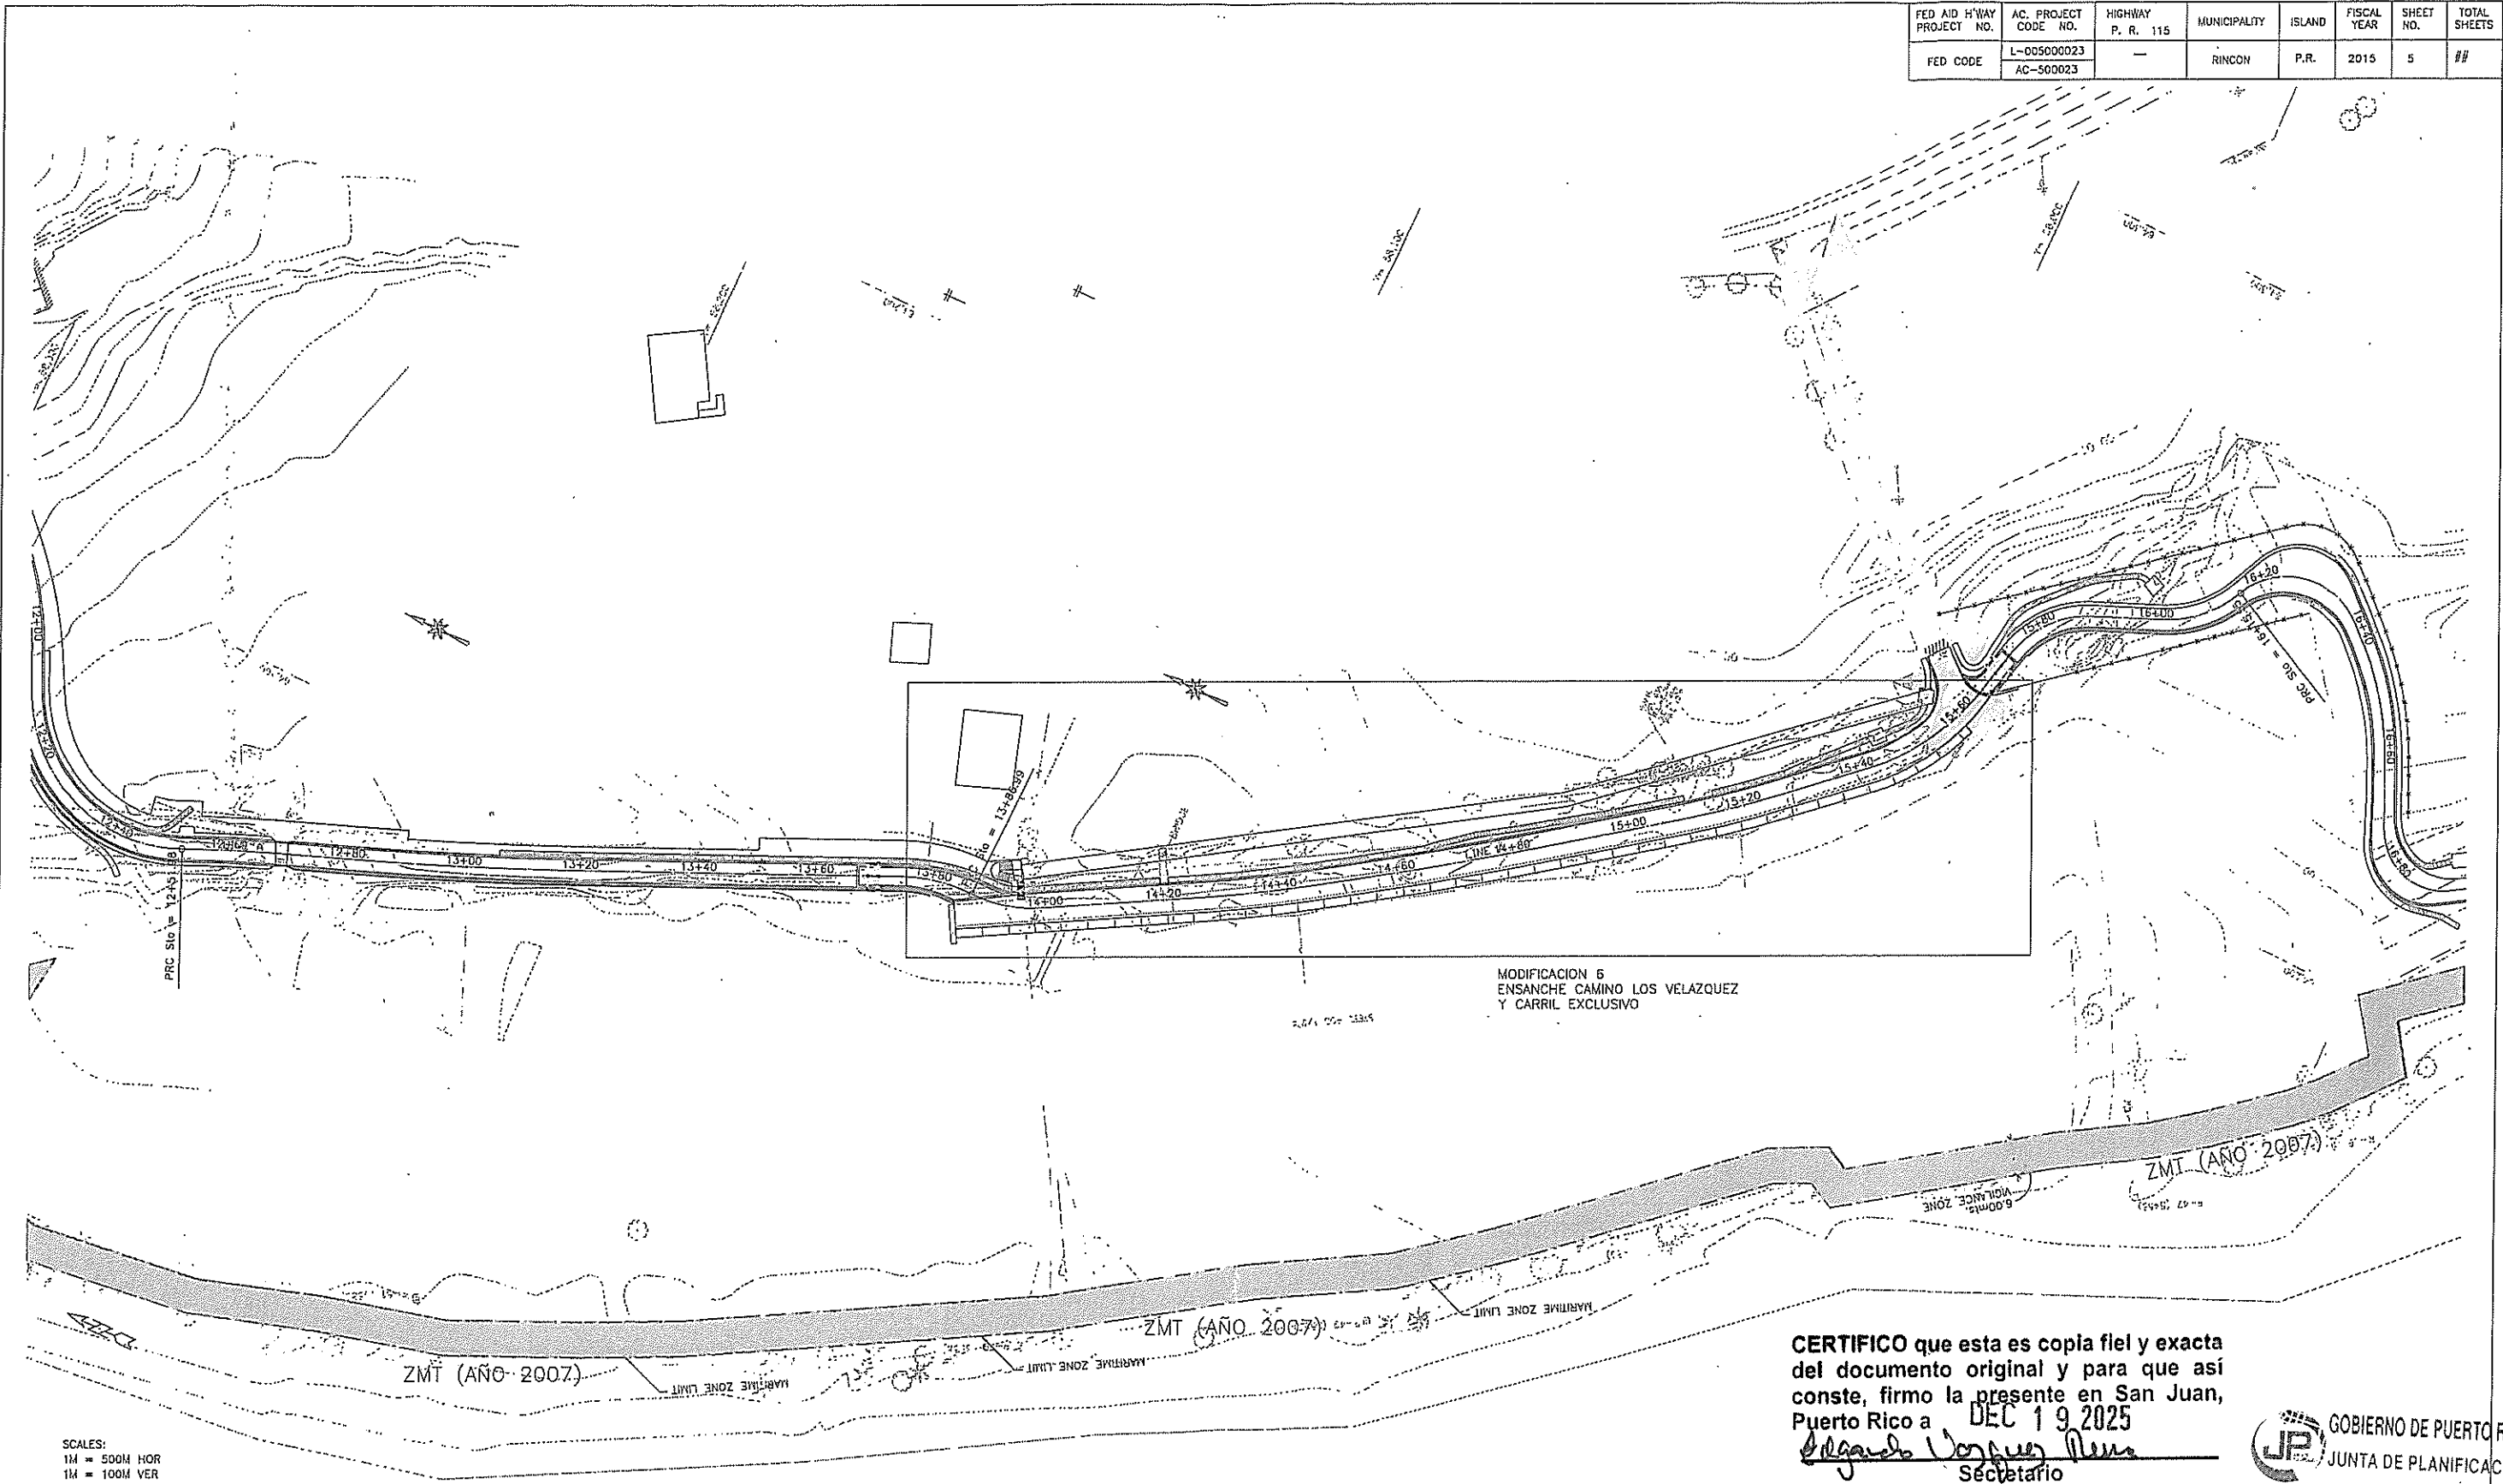

WORK	DATE	BY
DESIGN	AA	AA
DRAWING	AA	AA
TRACED	AA	AA
CHECK	AA	AA
FINAL CHECK	AA	AA

FILE NAME: C:\PROJECTS\AC-500023 TRIANGULACION\CARRETERAS\LOT\PCP20001.DWG

PUERTO RICO HIGHWAY AND TRANSPORTATION AUTHORITY
DESIGN AREA
HIGHWAY DESIGN OFFICE

SCENIC WALK FOR BICYCLE AND
PEDESTRIAN ROUTE
MUNICIPALITY OF RINCON

DATE	REVISIONS

SCALE
1:500


PRELIMINARY CONSTRUCTION PLAN
OLD AND NEW ALIGNMENT COMPARISON

PP
5

CERTIFICO que esta es copia fiel y exacta
del documento original y para que así
conste, firmo la presente en San Juan,
Puerto Rico a **DEC 19 2025**
Edgardo Vazquez Riera
Secretario

GOBIERNO DE PUERTO RICO
JUNTA DE PLANIFICACIÓN

FED AID H'WAY PROJECT NO.	AC. PROJECT CODE NO.	HIGHWAY P. R. 115	MUNICIPALITY	ISLAND	FISCAL YEAR	SHEET NO.	TOTAL SHEETS
FED CODE	L-005000023 AC-500023	—	RINCON	P.R.	2015	6	##

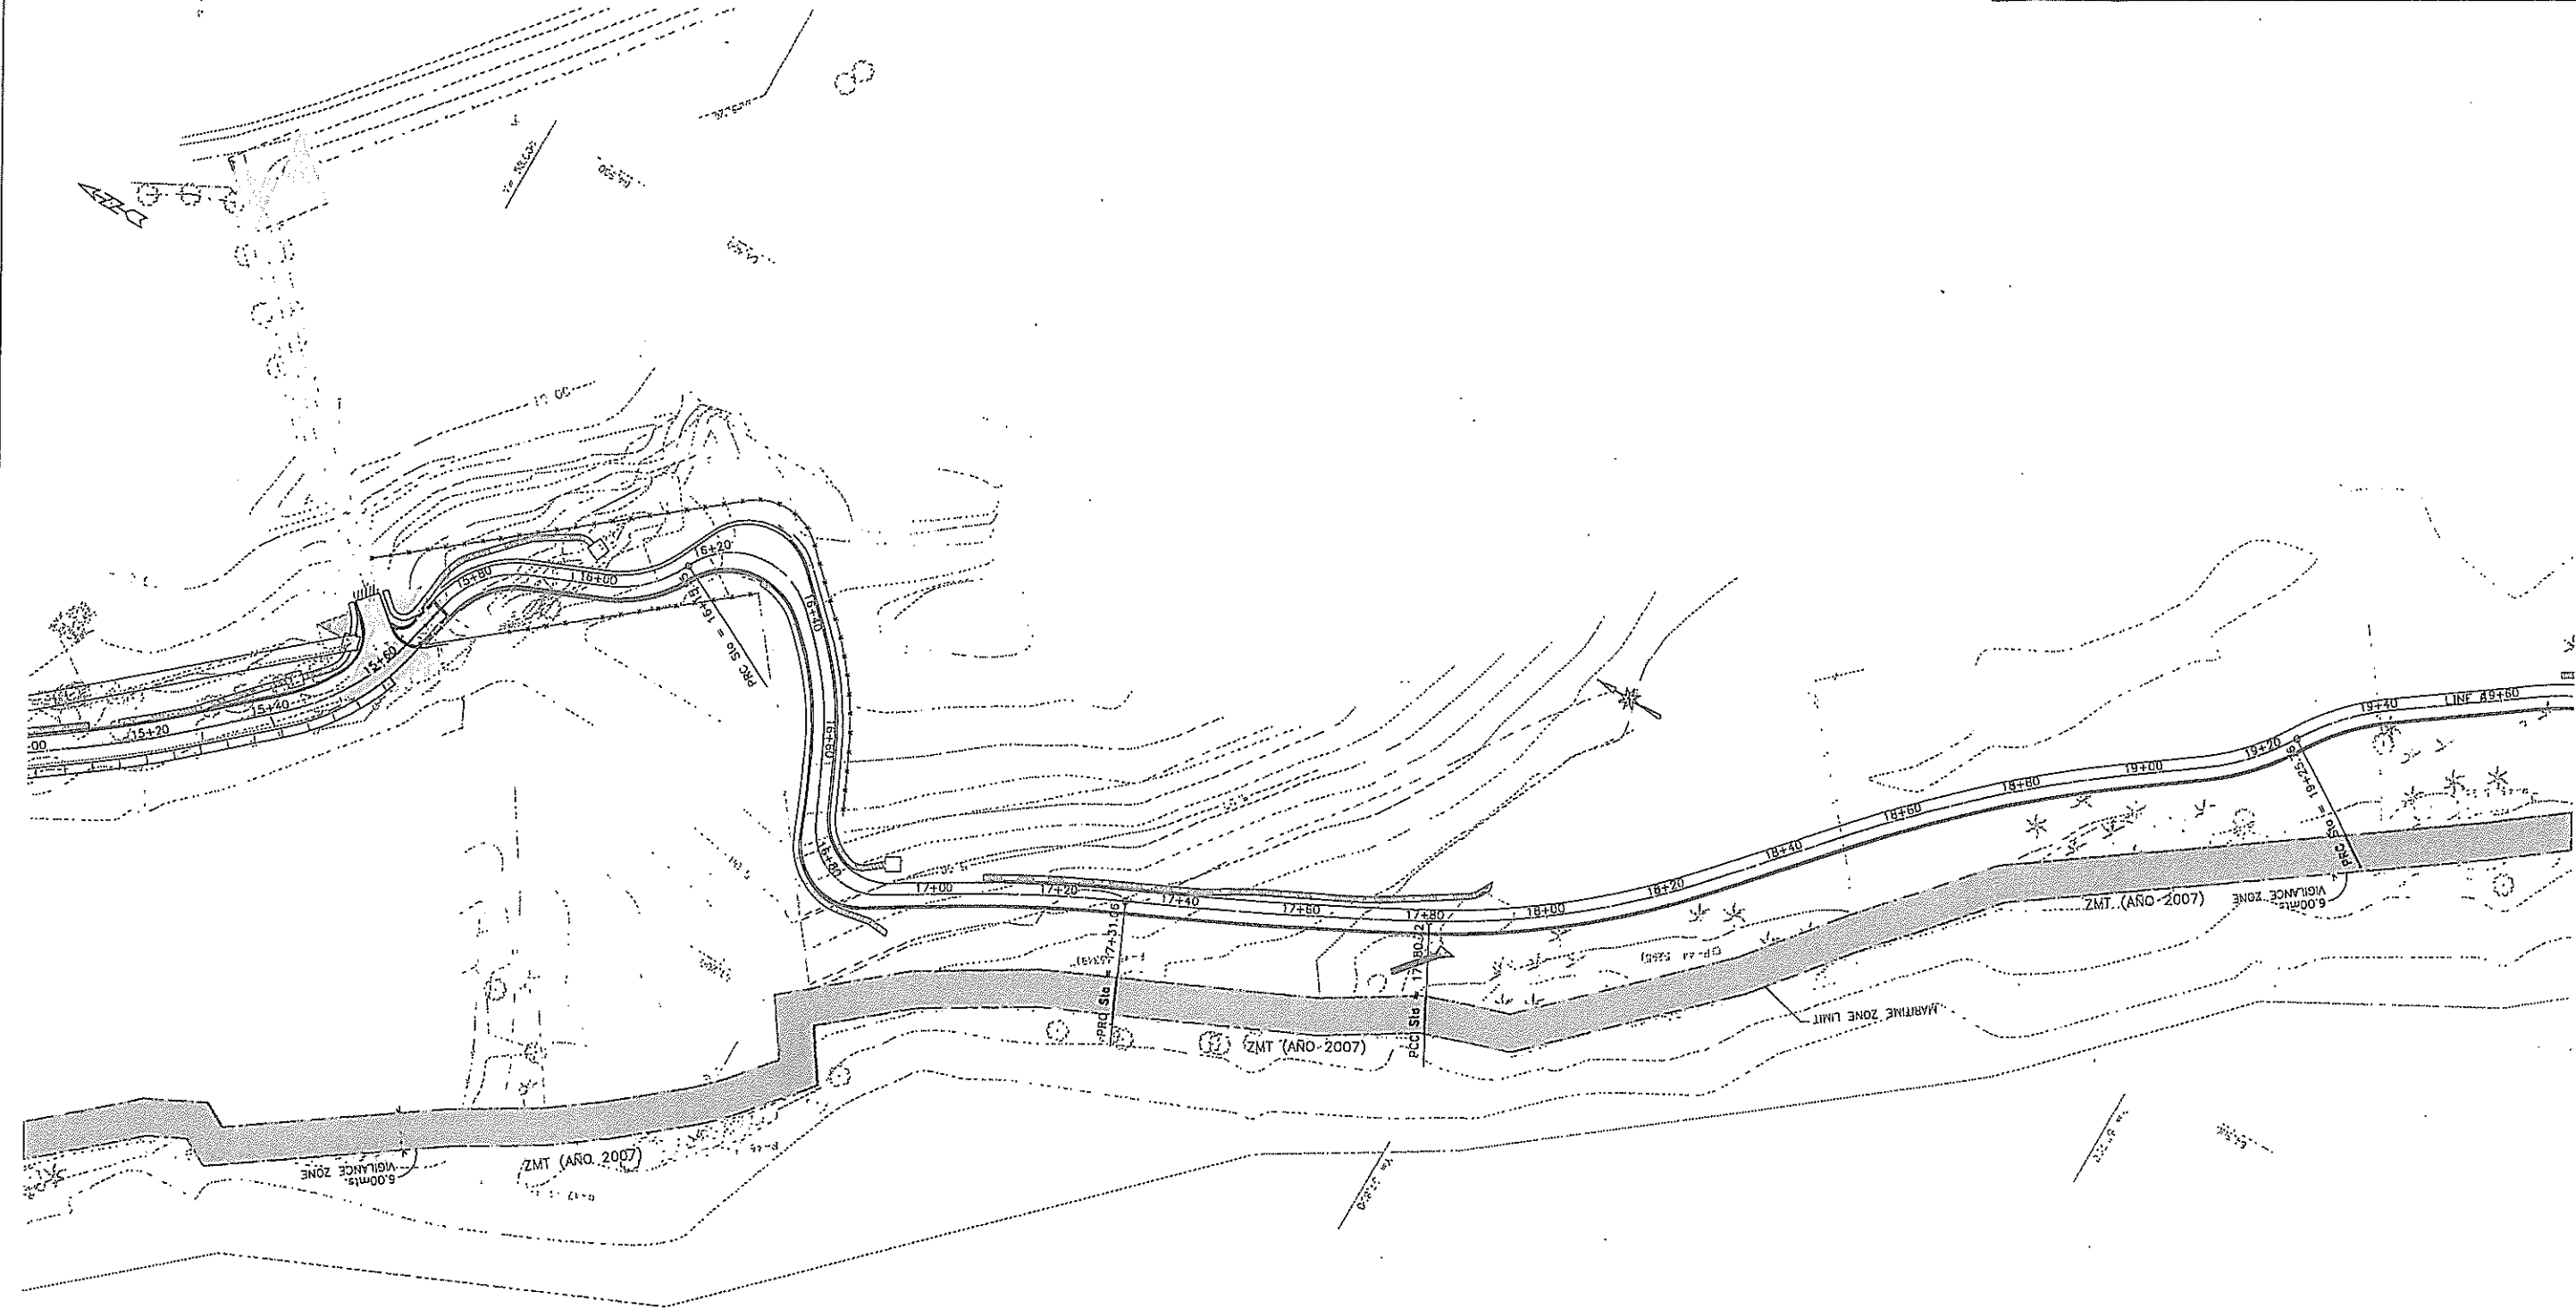

WORK	BY	DATE
DESIGN	AA	AA
DRAWING	AA	AA
TRACKED	AA	AA
CHECK	AA	AA
FINAL CHECK	AA	AA

FILE NAME: C:\PROJECTS\VC-500023 TRIANGULACION\500023 TRIANGULACION\CARRETERAS\LOT\PCP30001.DWG

SCALES:
1M = 500M HOR
1M = 100M VER

PUERTO RICO HIGHWAY AND TRANSPORTATION AUTHORITY
DESIGN AREA
HIGHWAY DESIGN OFFICE

SCENIC WALK FOR BICYCLE AND
PEDESTRIAN ROUTE
MUNICIPALITY OF RINCON


DATE	REVISIONS

SCALE
1:500



PRELIMINARY CONSTRUCTION PLAN
OLD AND NEW ALIGNMENT COMPARISON

PP
6

CERTIFICO que esta es copia fiel y exacta
del documento original y para que asi
conste, firmo la presente en San Juan,
Puerto Rico a **DEC 19 2025**
Edgardo Vazquez Rivera
Secretario

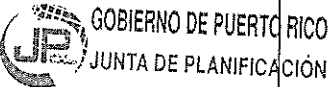

FED AID H'WAY PROJECT NO.	AC. PROJECT CODE NO.	HIGHWAY P. R. 115	MUNICIPALITY	ISLAND	FISCAL YEAR	SHEET NO.	TOTAL SHEETS
FED CODE	L-005000023 AC-500023	—	RINCON	P.R.	2015	7	##

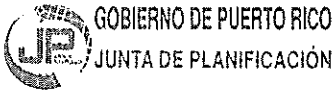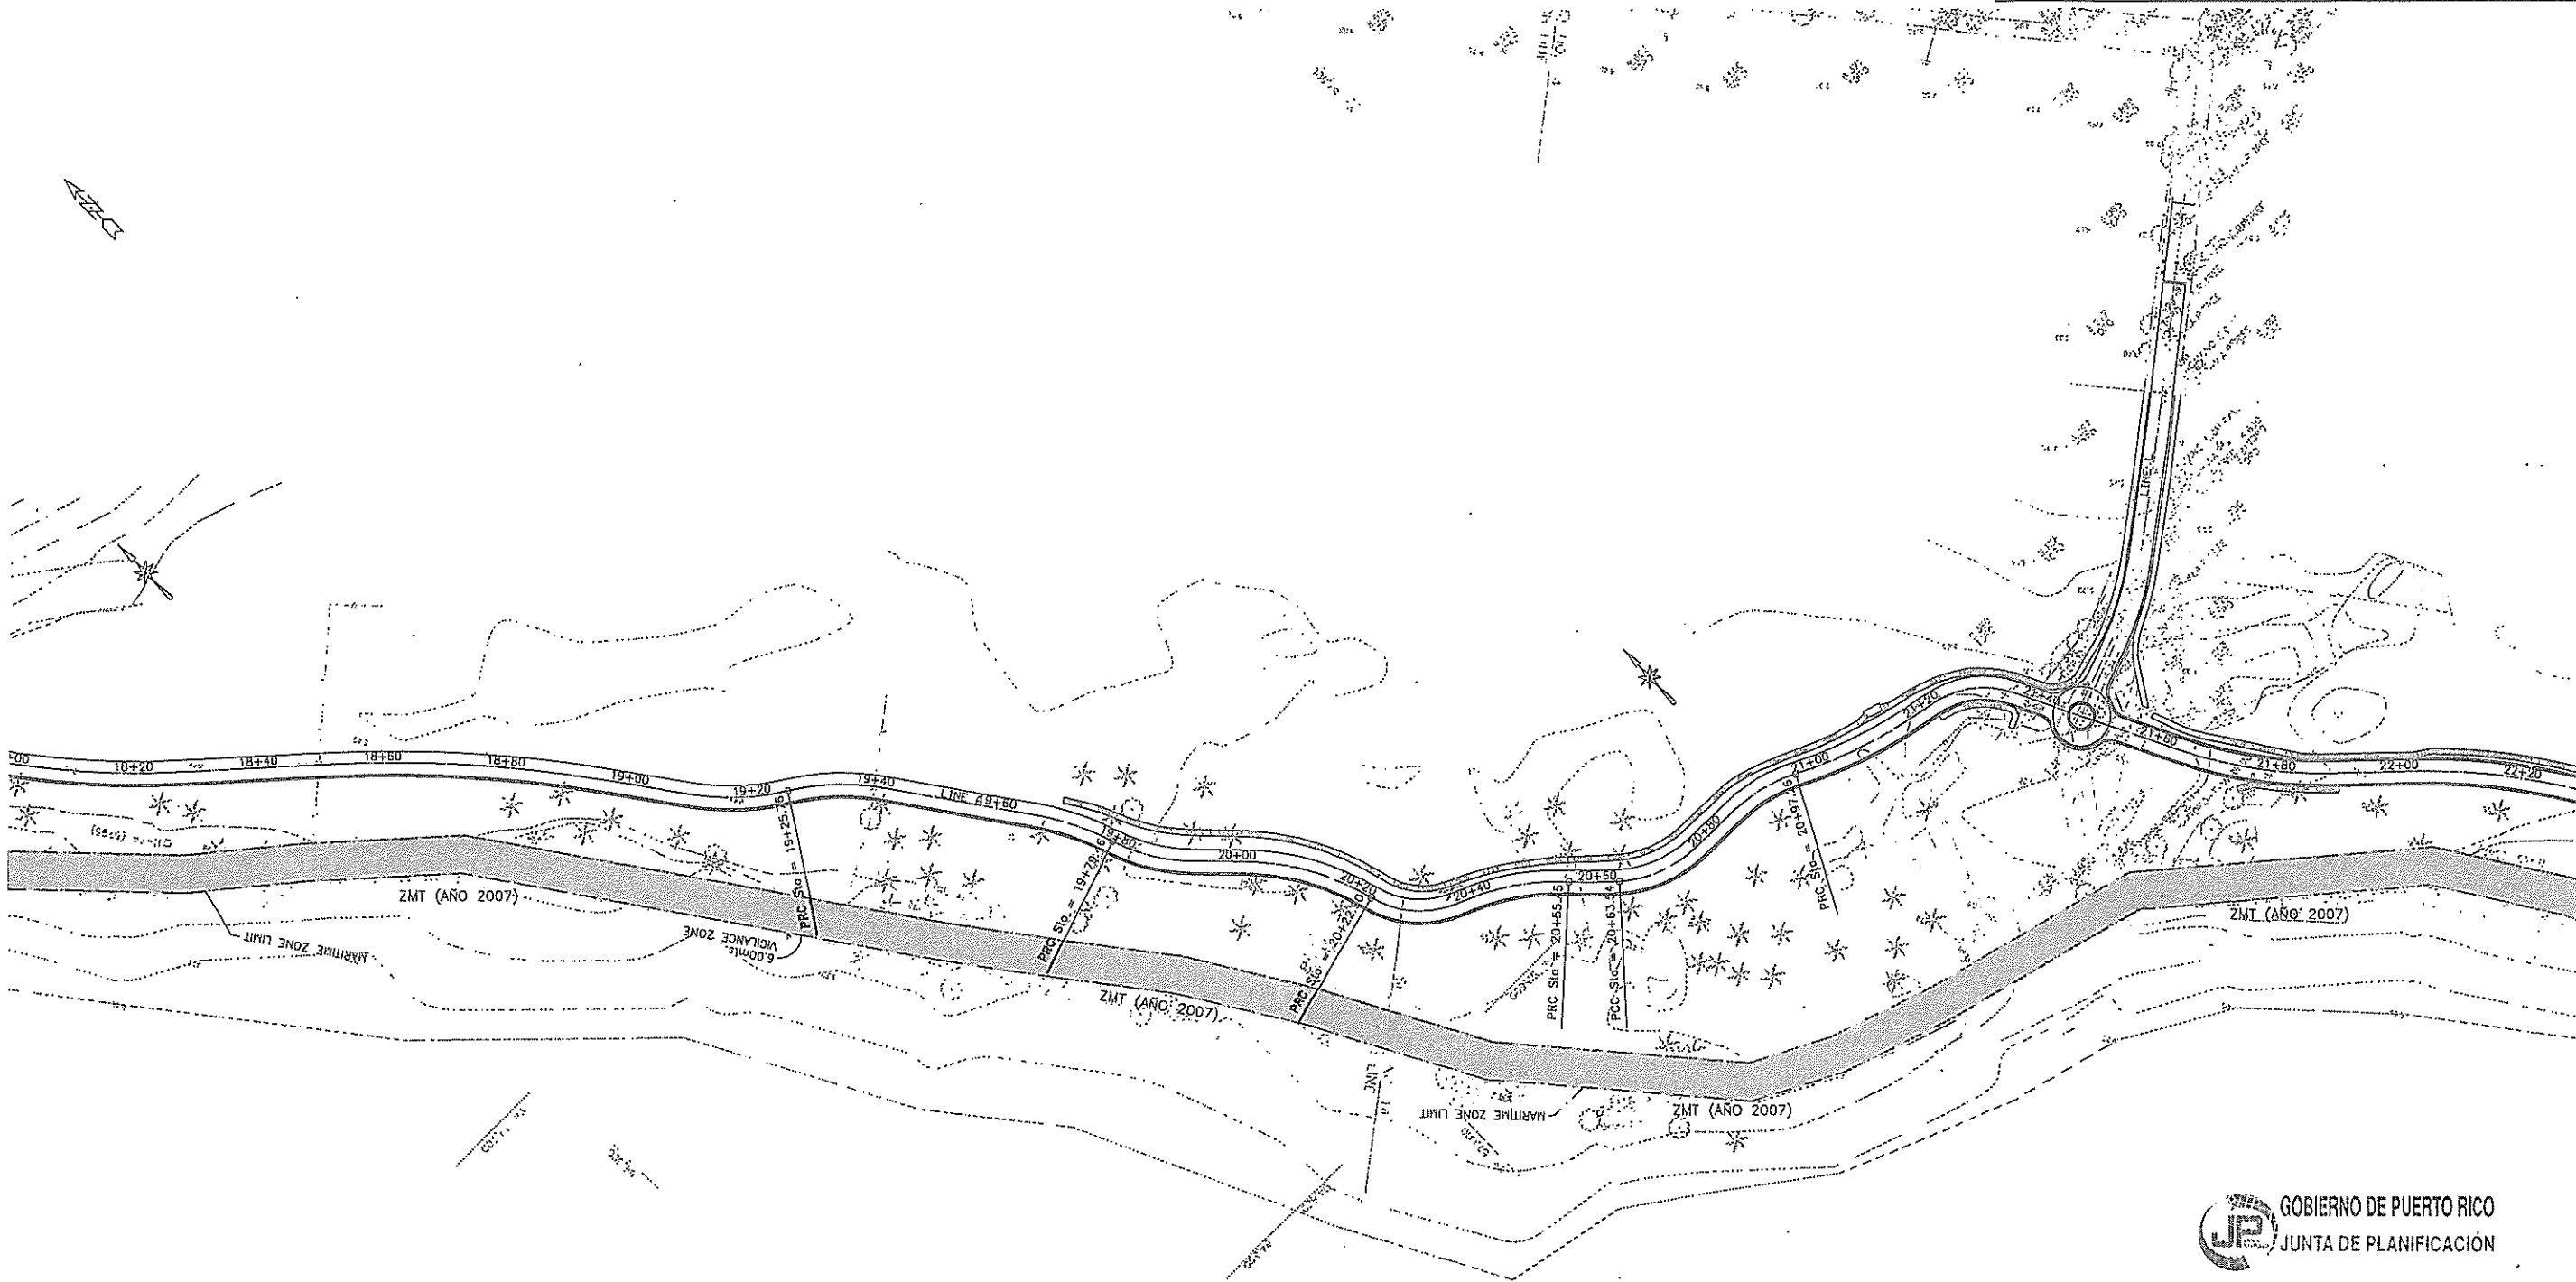

CERTIFICO que esta es copia fiel y exacta del documento original y para que así conste, firmo la presente en San Juan, Puerto Rico a **DEC 19 2025**
Eduardo Vazquez
Secretario

WORK	DATE
DESIGN	AA
DRAWING	AA
TRACED	AA
CHECK	AA
FINAL CHECK	AA

FILE NAME: C:\PROJECTS\AC-500023 TRIANGULACION\500023 TRIANGULACION\CARRITERAS\PILOT\ROP31001.DWG

SCALES:
1M = 500M HOR
1M = 100M VER

PUERTO RICO HIGHWAY AND TRANSPORTATION AUTHORITY
DESIGN AREA
HIGHWAY DESIGN OFFICE

SCENIC WALK FOR BICYCLE
AND PEDESTRIAN ROUTE
MUNICIPALITY OF RINCON


DATE	REVISIONS

SCALE
1:500


PRELIMINARY CONSTRUCTION PLAN
OLD AND NEW ALIGNMENT COMPARISON

PP
7

FED AID H'WAY PROJECT NO.	AC. PROJECT CODE NO.	HIGHWAY P. R. 115	MUNICIPALITY	ISLAND	FISCAL YEAR	SHEET NO.	TOTAL SHEETS
FED CODE	L-005000023 AC-500023	—	RINCON	P.R.	2015	8	##

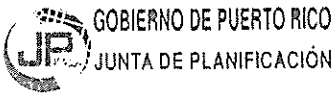

CERTIFICO que esta es copia fiel y exacta del documento original y para que así conste, firmo la presente en San Juan, Puerto Rico a DEC 19 2025
Edgardo Vazquez
Secretario

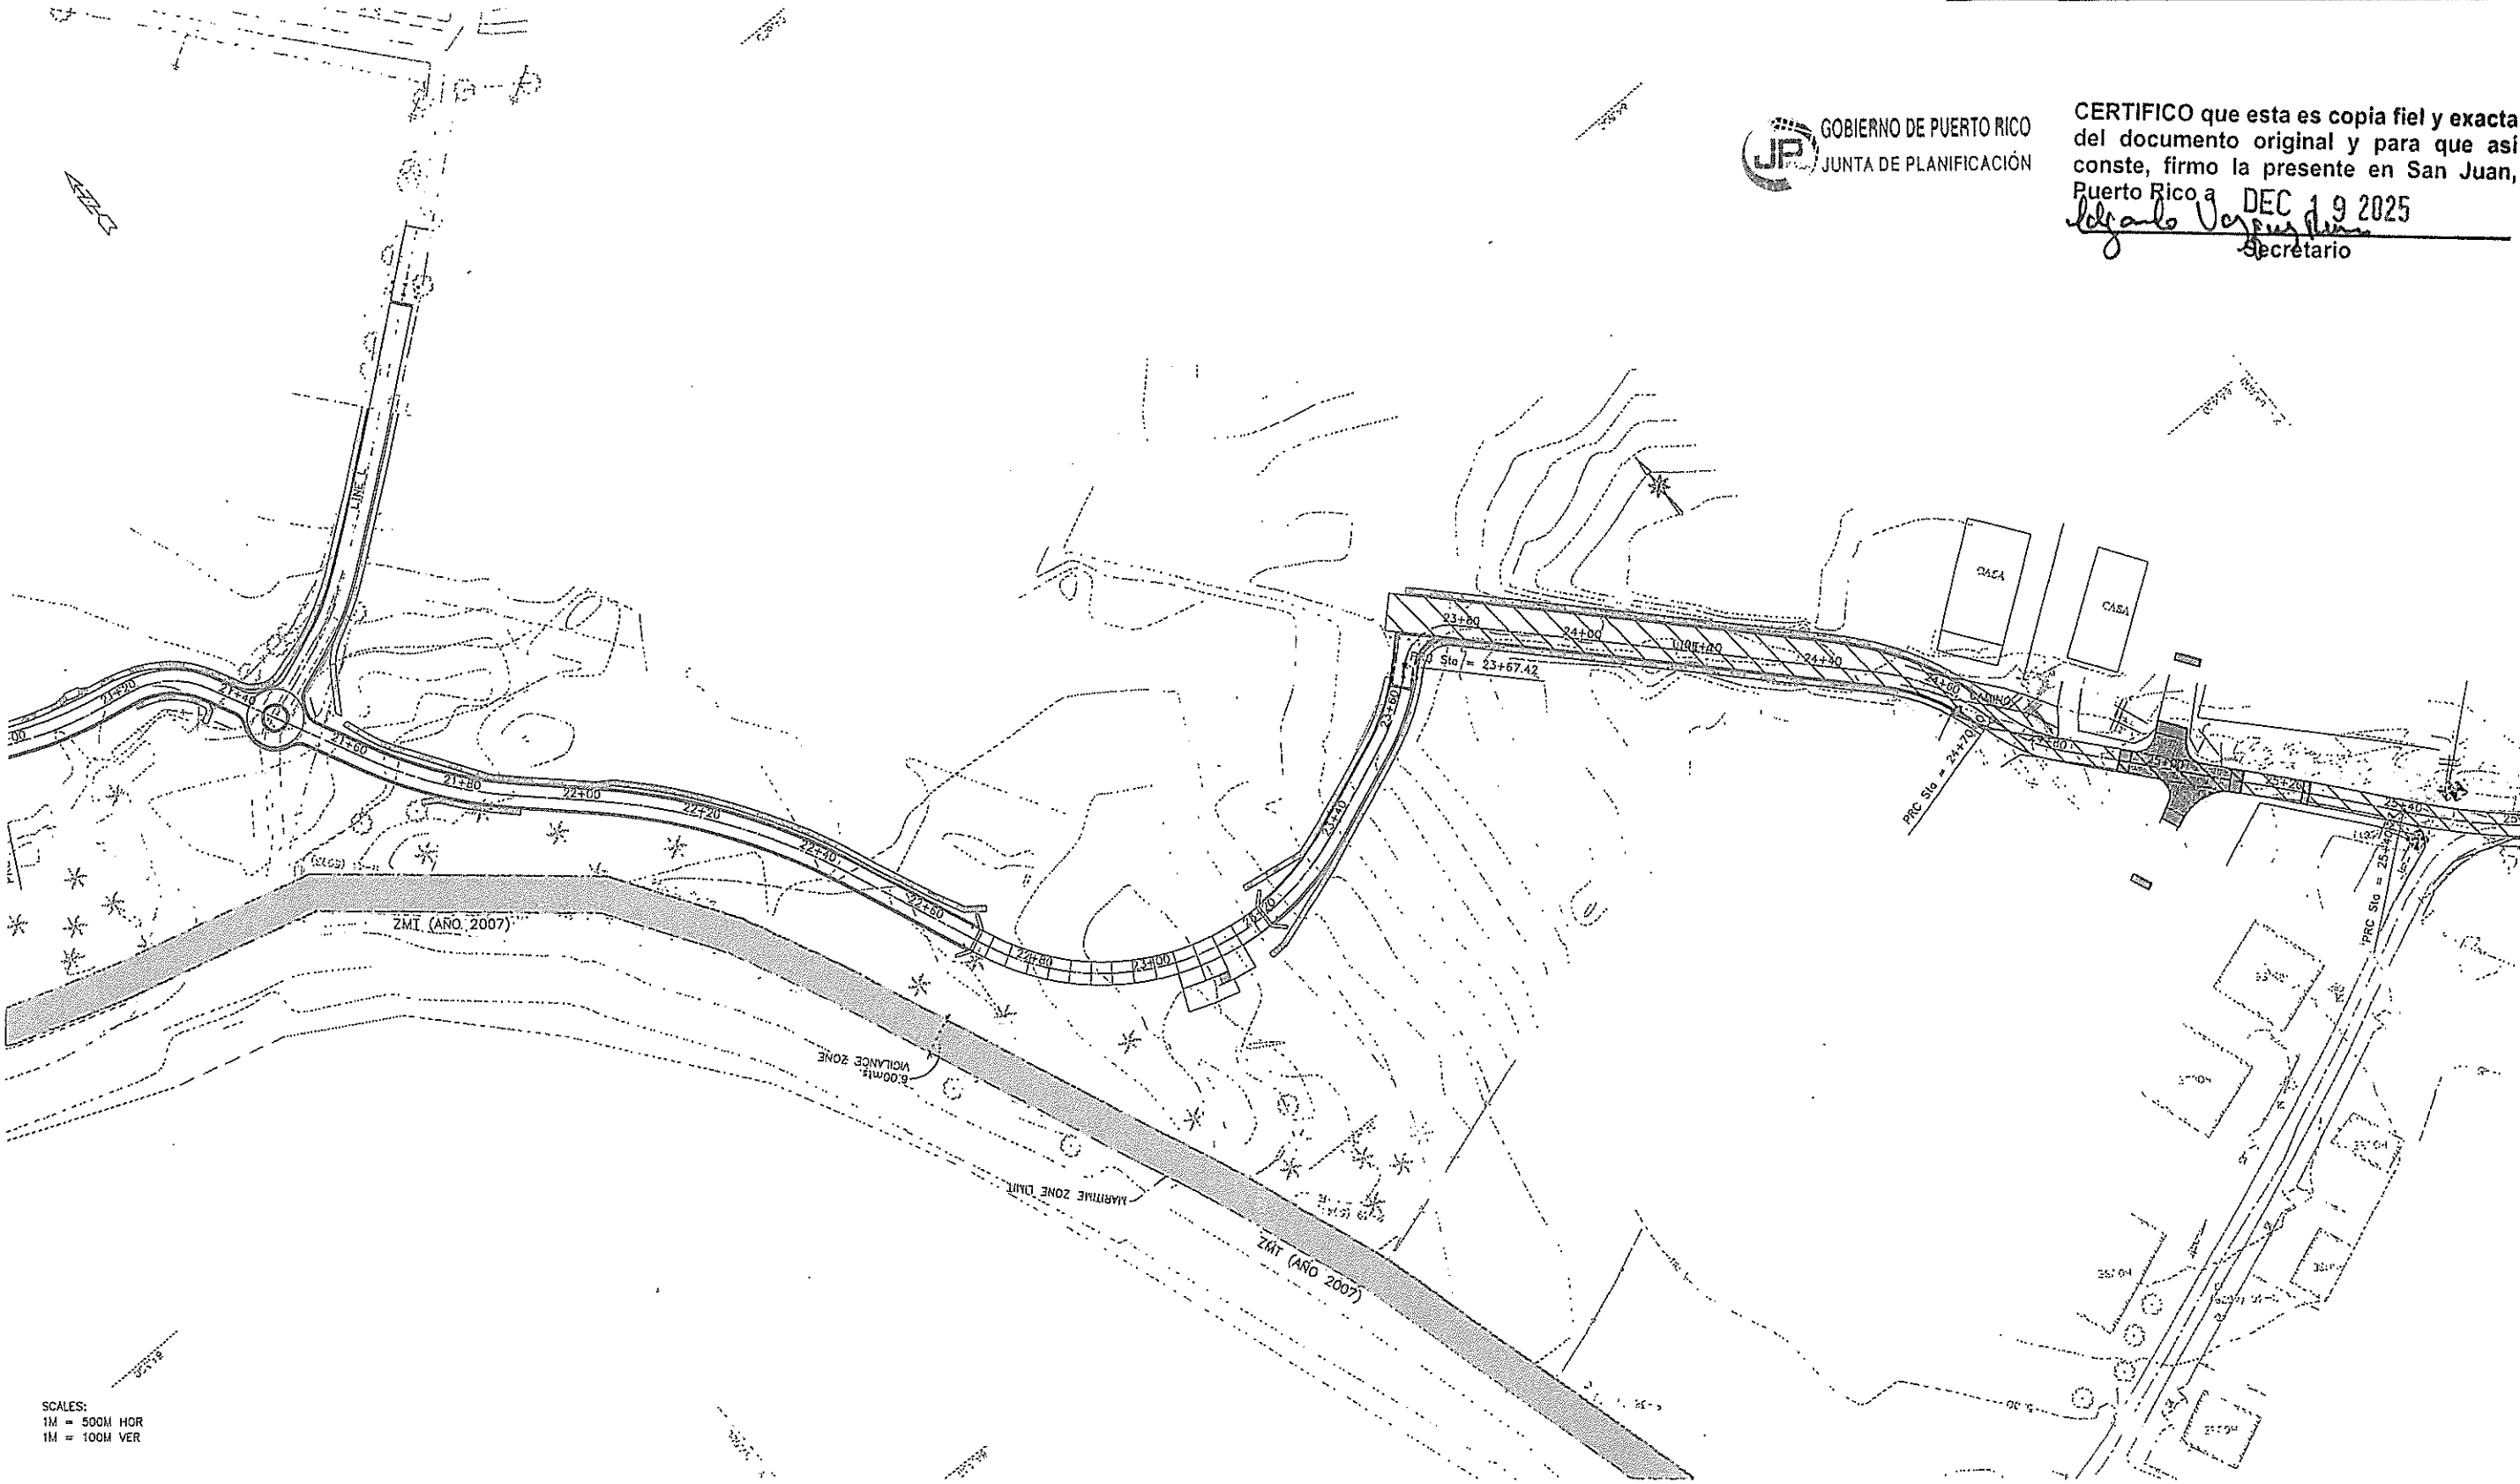

SCALES:
1M = 500M HOR
1M = 100M VER

WORK	BY	DATE
DESIGN	AA	AA
DRAWING	AA	AA
TRACED	AA	AA
CHECK	AA	AA
FINAL CHECK	AA	AA

FILE NAME: C:\PROJECTS\AC-500023 TRIANGULACION\CARRETERAS\LOT RCP32001.DWG

PUERTO RICO HIGHWAY AND TRANSPORTATION AUTHORITY
DESIGN AREA
HIGHWAY DESIGN OFFICE

SCENIC WALK FOR BICYCLE
AND PEDESTRIAN ROUTE
MUNICIPALITY OF RINCON


DATE	REVISIONS

SCALE
1:500

PRELIMINARY CONSTRUCTION PLAN
OLD AND NEW ALIGNMENT COMPARISON

PP
8

FED AID H'WAY PROJECT NO.	AC. PROJECT CODE NO.	HIGHWAY P. R. 115	MUNICIPALITY	ISLAND	FISCAL YEAR	SHEET NO.	TOTAL SHEETS
FED CODE	L-005000023 AC-500023	—	RINCON	P.R.	2015	10	##

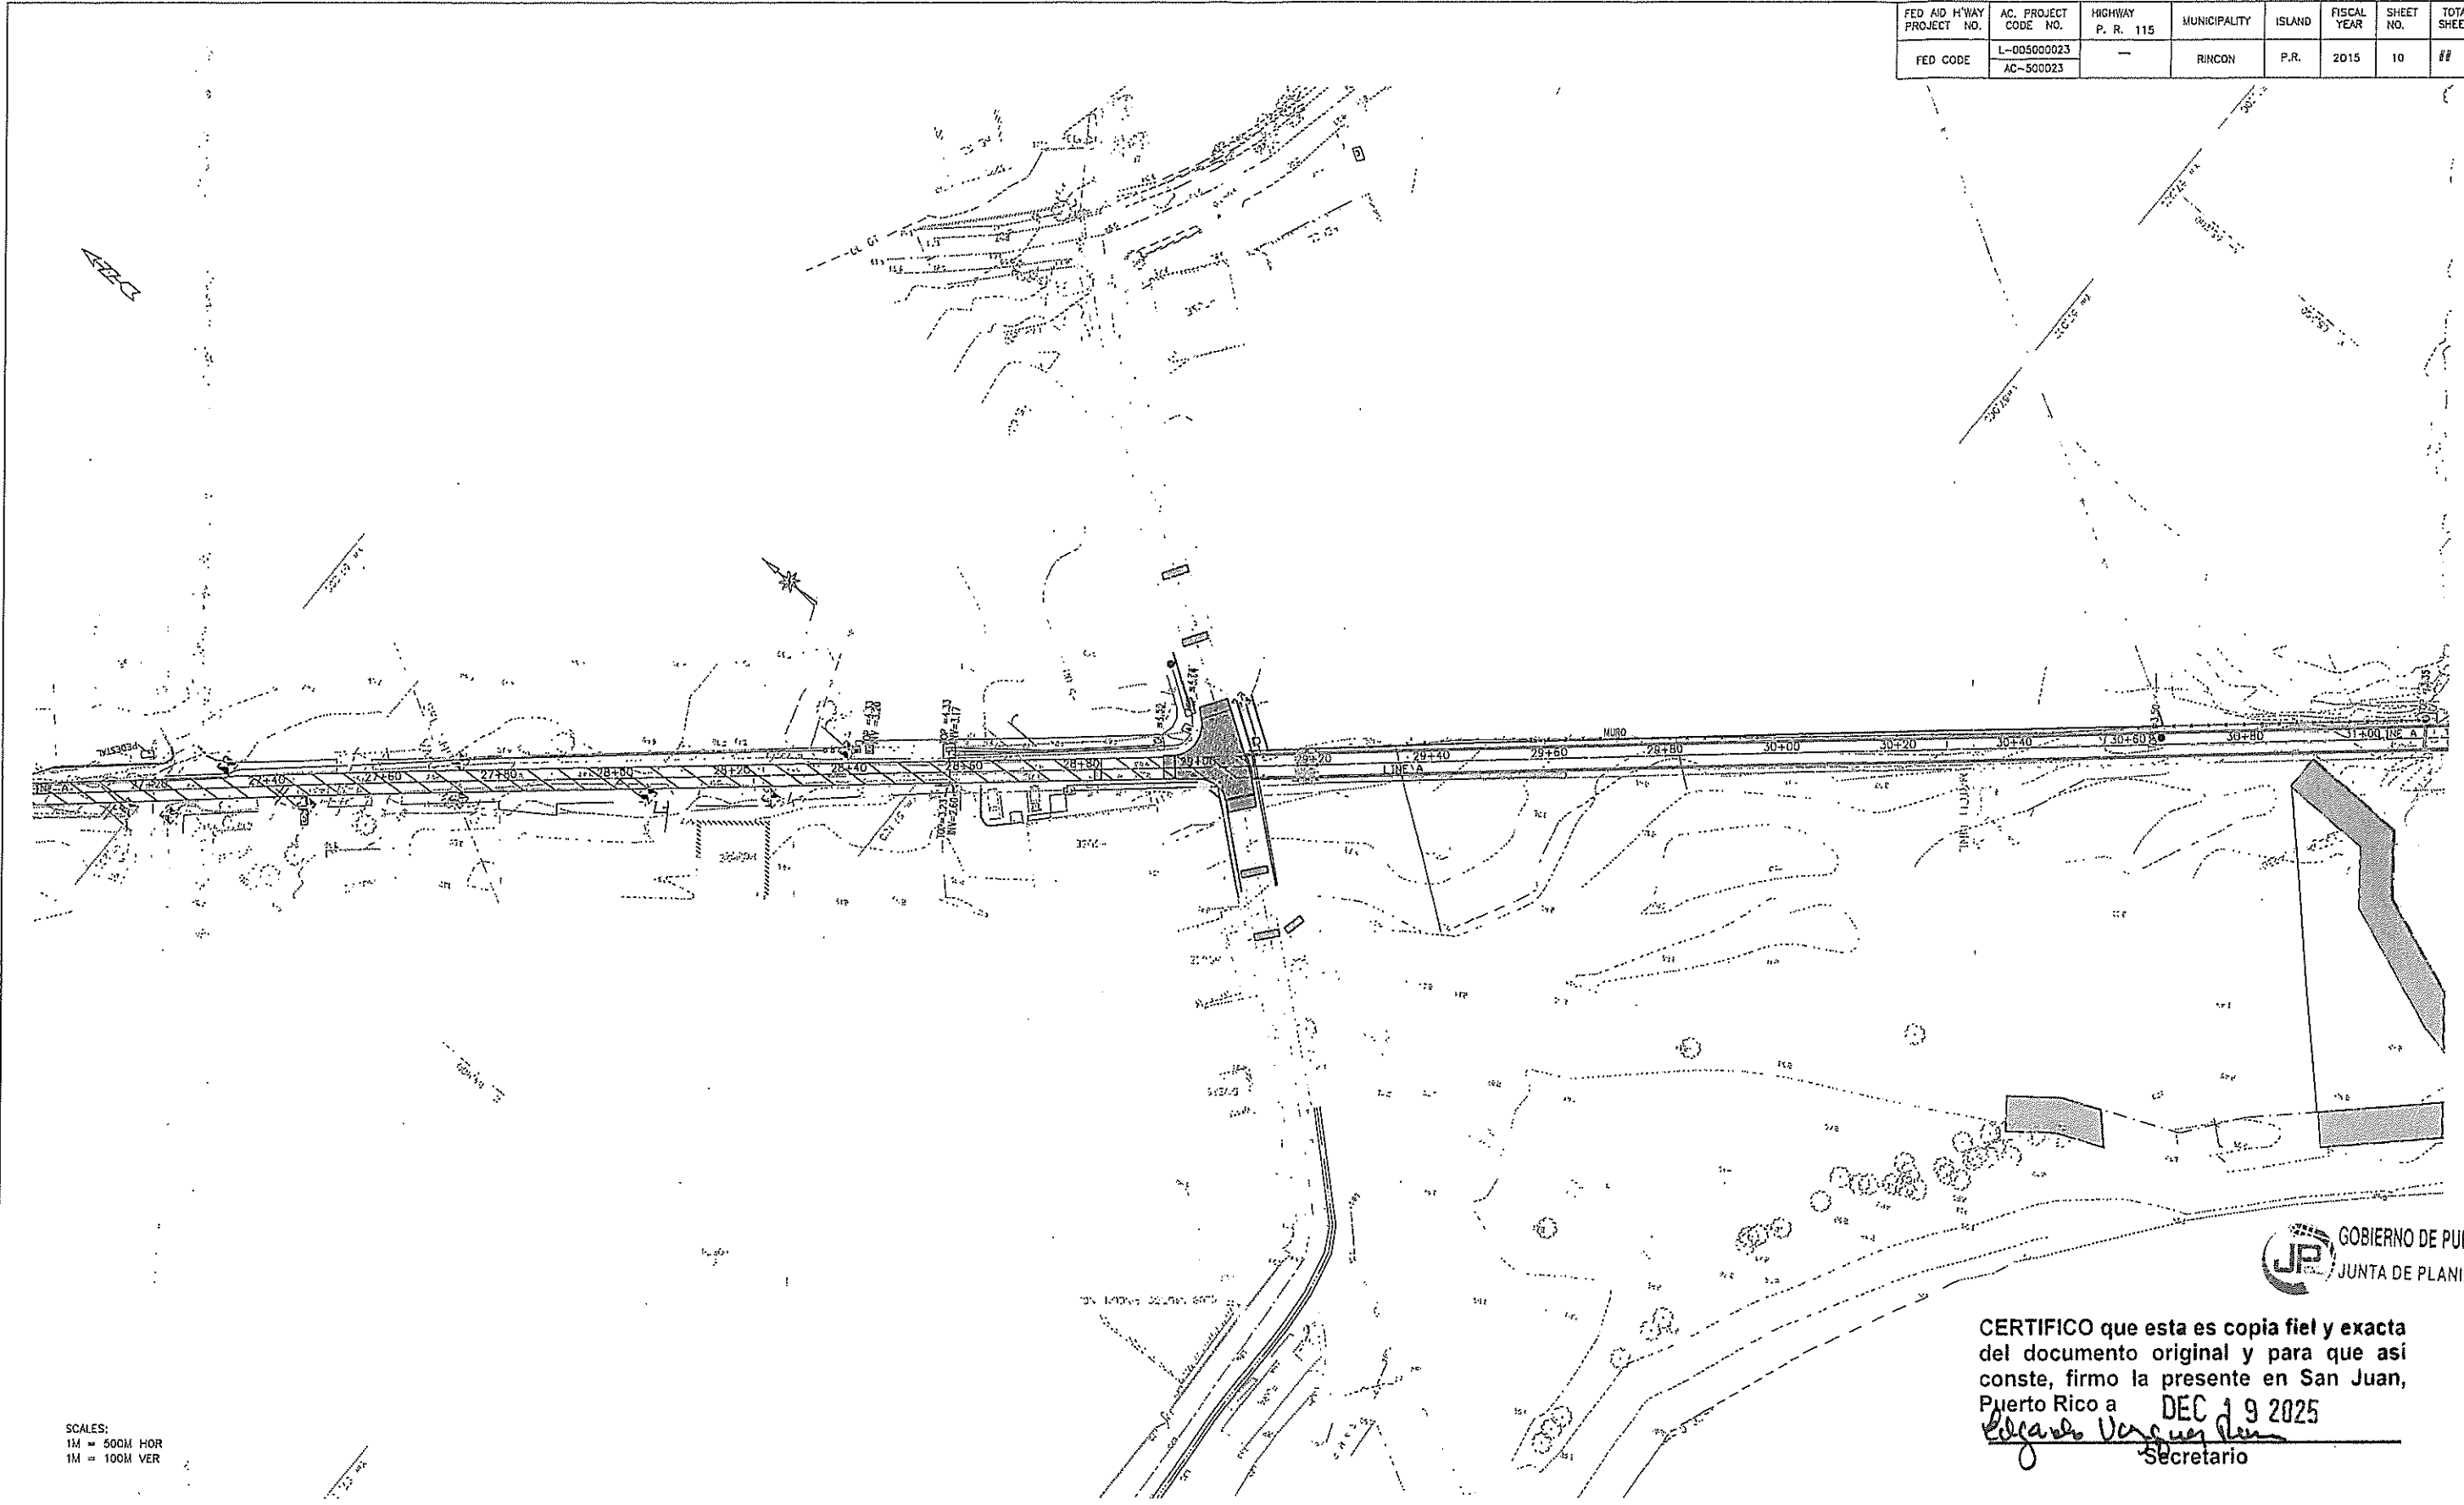

GOBIERNO DE PUERTO RICO
JUNTA DE PLANIFICACIÓN

CERTIFICO que esta es copia fiel y exacta
del documento original y para que así
conste, firmo la presente en San Juan,
Puerto Rico a **DEC 19 2025**
Edgardo Vargues
Secretario

WORK	BY	DATE
DESIGN	AA	AA
DRAWING	AA	AA
TRACED	AA	AA
CHECK	AA	AA
FINAL CHECK	AA	AA

SCALES:
1" = 500' HOR
1" = 100' VER

PUERTO RICO HIGHWAY AND TRANSPORTATION AUTHORITY
DESIGN AREA
HIGHWAY DESIGN OFFICE


SCENIC WALK FOR BICYCLE
AND PEDESTRIAN ROUTE
MUNICIPALITY OF RINCON

DATE	REVISIONS

SCALE
1:500

PRELIMINARY CONSTRUCTION PLAN
OLD AND NEW ALIGNMENT COMPARISON

PP
10

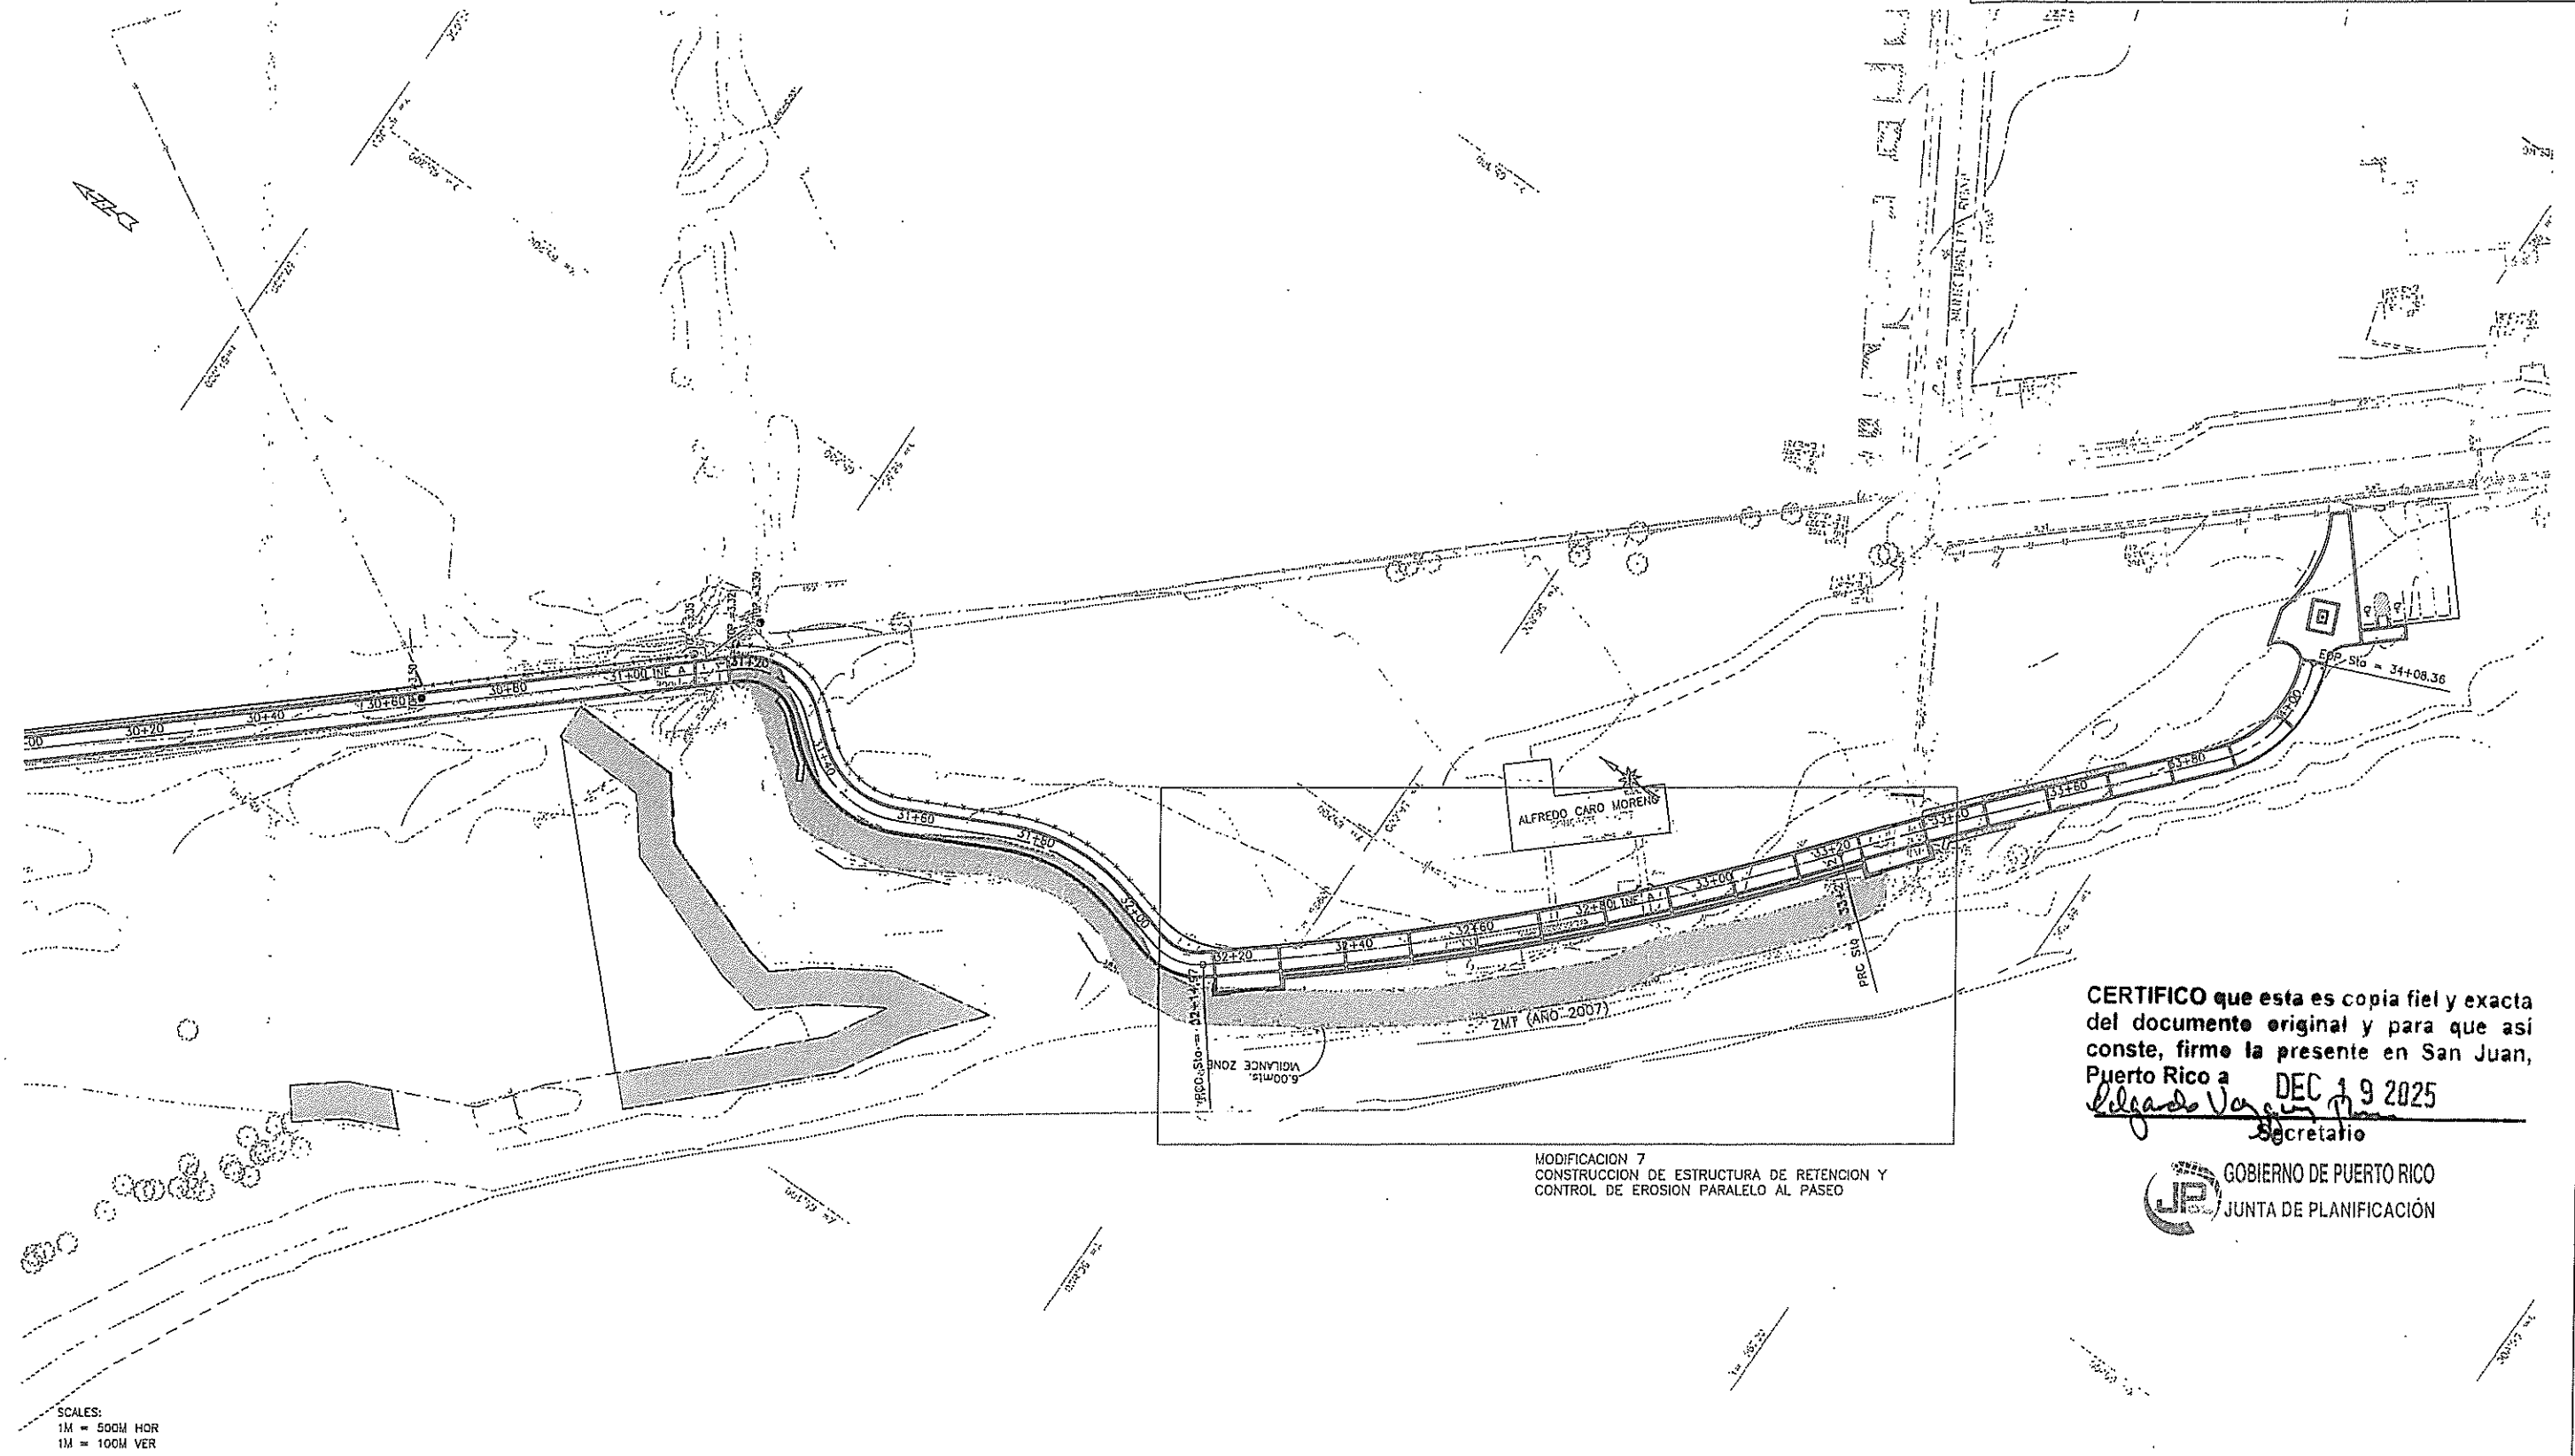

CERTIFICO que esta es copia fiel y exacta
del documento original y para que así
conste, firmo la presente en San Juan,
Puerto Rico a DEC 10 2005

Puerto Rico a Edgardo Vargas DEC 19 2025
Secretario

 GOBIERNO DE PUERTO RICO
JUNTA DE PLANIFICACIÓN

MODIFICACION 7
CONSTRUCCION DE ESTRUCTURA DE RETENCION Y
CONTROL DE EROSION PARALELO AL PASEO

WORK	BY	DATE
DESIGN	AA	AA
DRAWING	AA	AA
TRACING	AA	AA
CHECK	AA	AA
FINAL CHECK	AA	AA

PUERTO RICO HIGHWAY AND TRANSPORTATION AUTHORITY
DESIGN AREA
HIGHWAY DESIGN OFFICE

SCENIC WALK FOR BICYCLE
AND PEDESTRIAN ROUTE
MUNICIPALITY OF RINCON


DATE	REVISIONS

SCALE
1:500

PRELIMINARY CONSTRUCTION PLAN
OLD AND NEW ALIGNMENT COMPARISON

pp	11
----	----

FED AID H'WAY PROJECT NO.	AC. PROJECT CODE NO.	HIGHWAY P. R. 115	MUNICIPALITY	ISLAND	FISCAL YEAR	SHEET NO.	TOTAL SHEETS
FED CODE	L-005000023 AC-S00023	—	RINCON	P.R.	2015	12	##

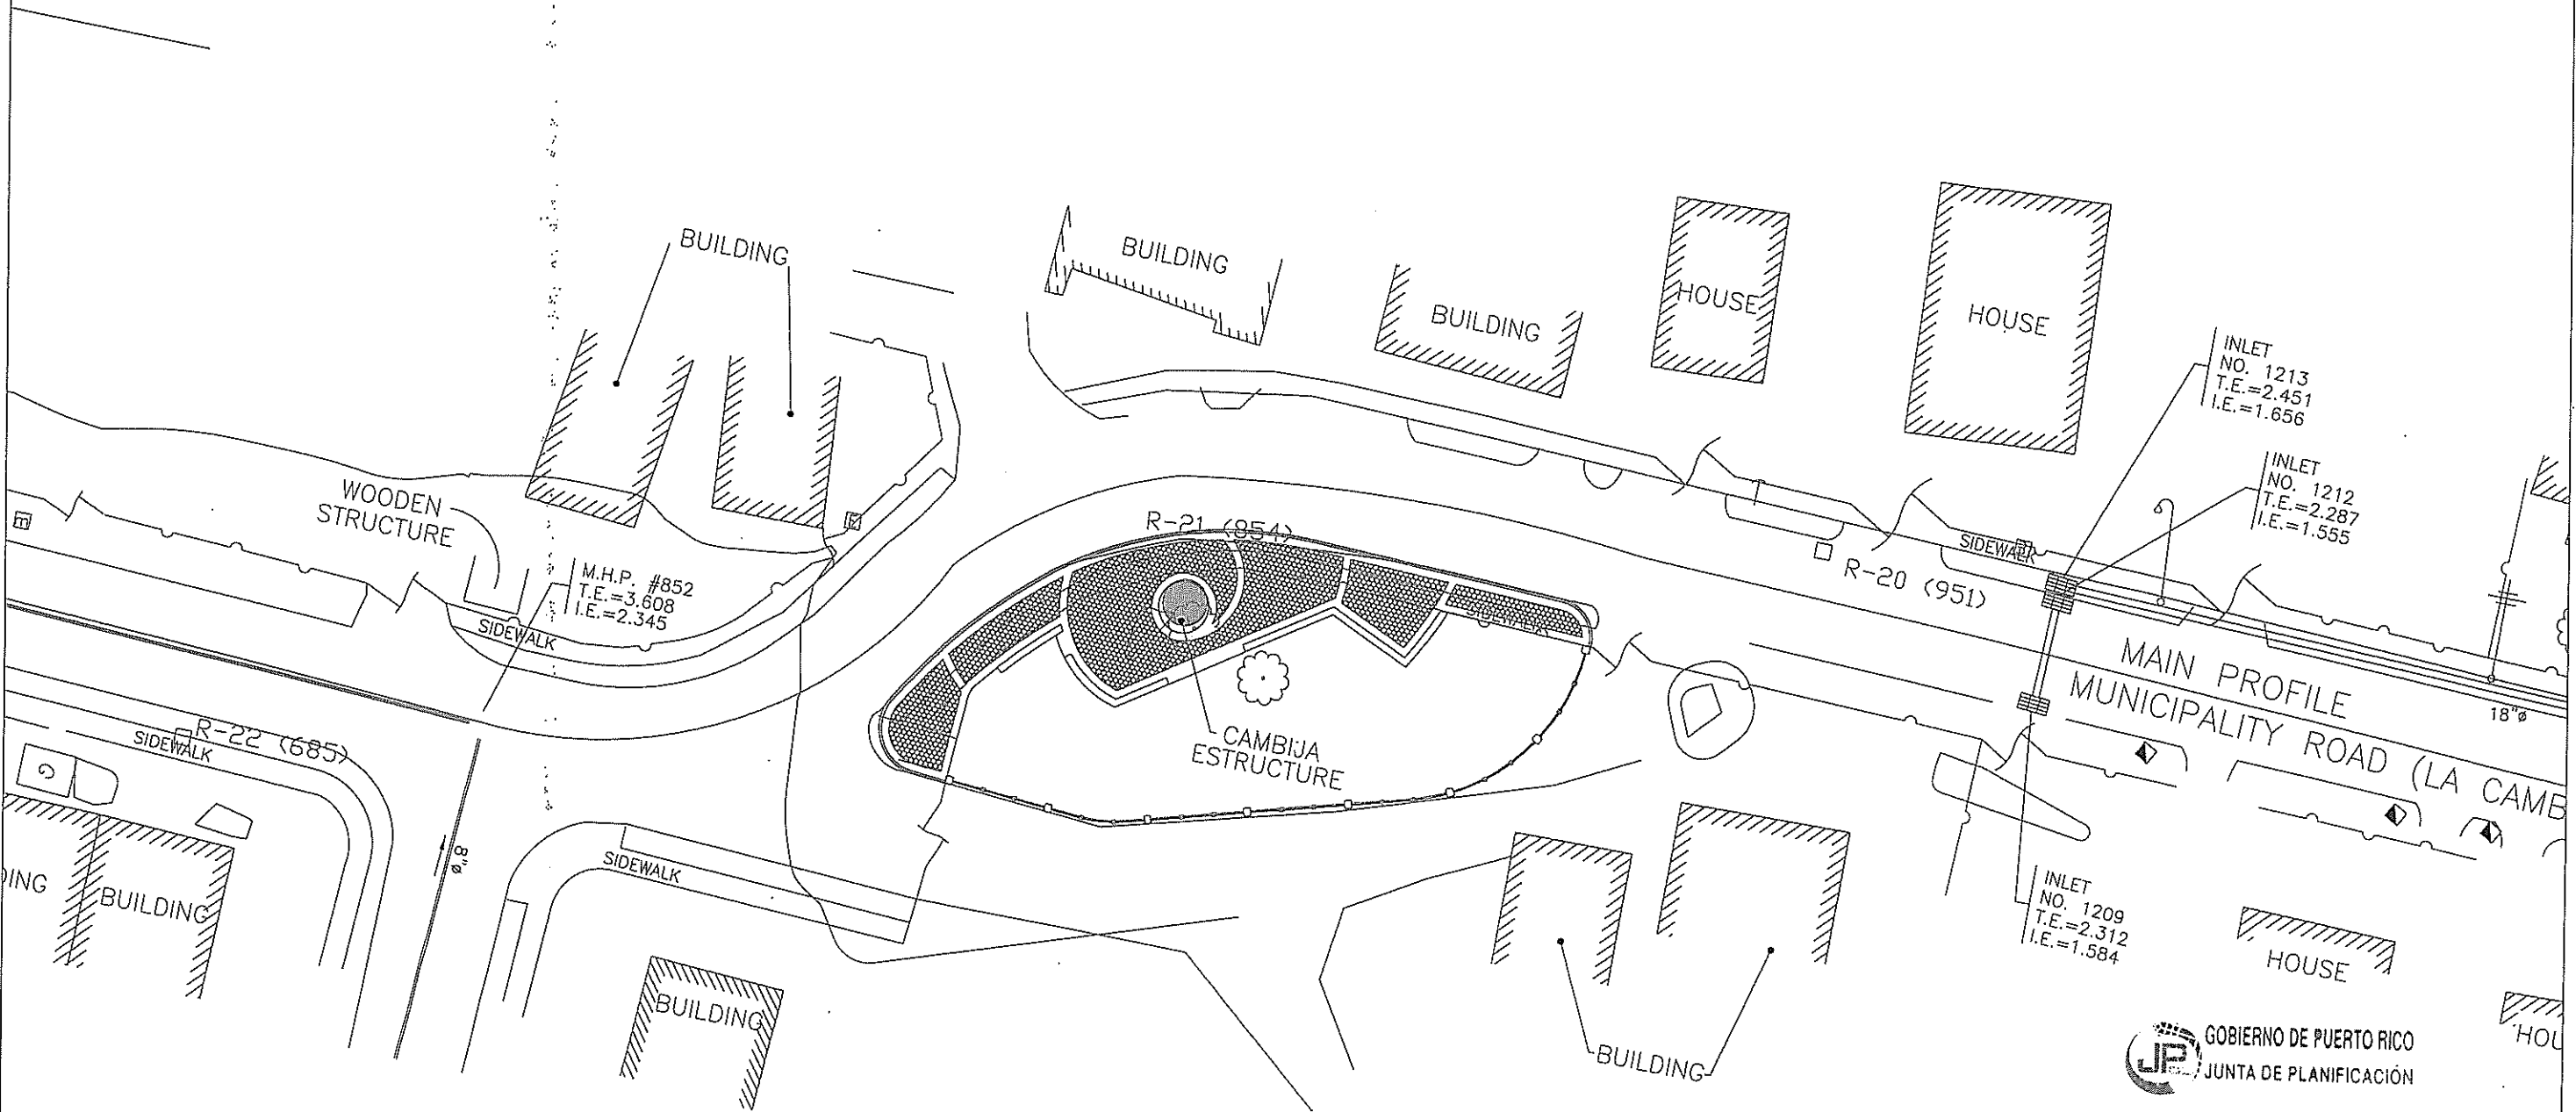

GOBIERNO DE PUERTO RICO
JUNTA DE PLANIFICACIÓN

CERTIFICO que esta es copia fiel y exacta del documento original y para que así conste, firmo la presente en San Juan, Puerto Rico a **DEC 19 2025**
[Signature]
Secretario

WORK	BY	DATE
DESIGN	AA	AA
DRAWING	AA	AA
REVISION	AA	AA
CHECK	AA	AA
FINAL CHECK	AA	AA

FILE NAME: C:\PROJECTS\AC-500023 TRIANGULACION\500023 TRIANGULACION\CARRETERAS\ROADS.DWG

PUERTO RICO HIGHWAY AND TRANSPORTATION AUTHORITY
DESIGN AREA
HIGHWAY DESIGN OFFICE

SCENIC WALK FOR BICYCLE
AND PEDESTRIAN ROUTE
MUNICIPALITY OF RINCON

DATE	REVISIONS

SCALE
1:200

PRELIMINARY CONSTRUCTION PLAN
LA CAMBIJA LANDMARK PLAZA

PP
12