



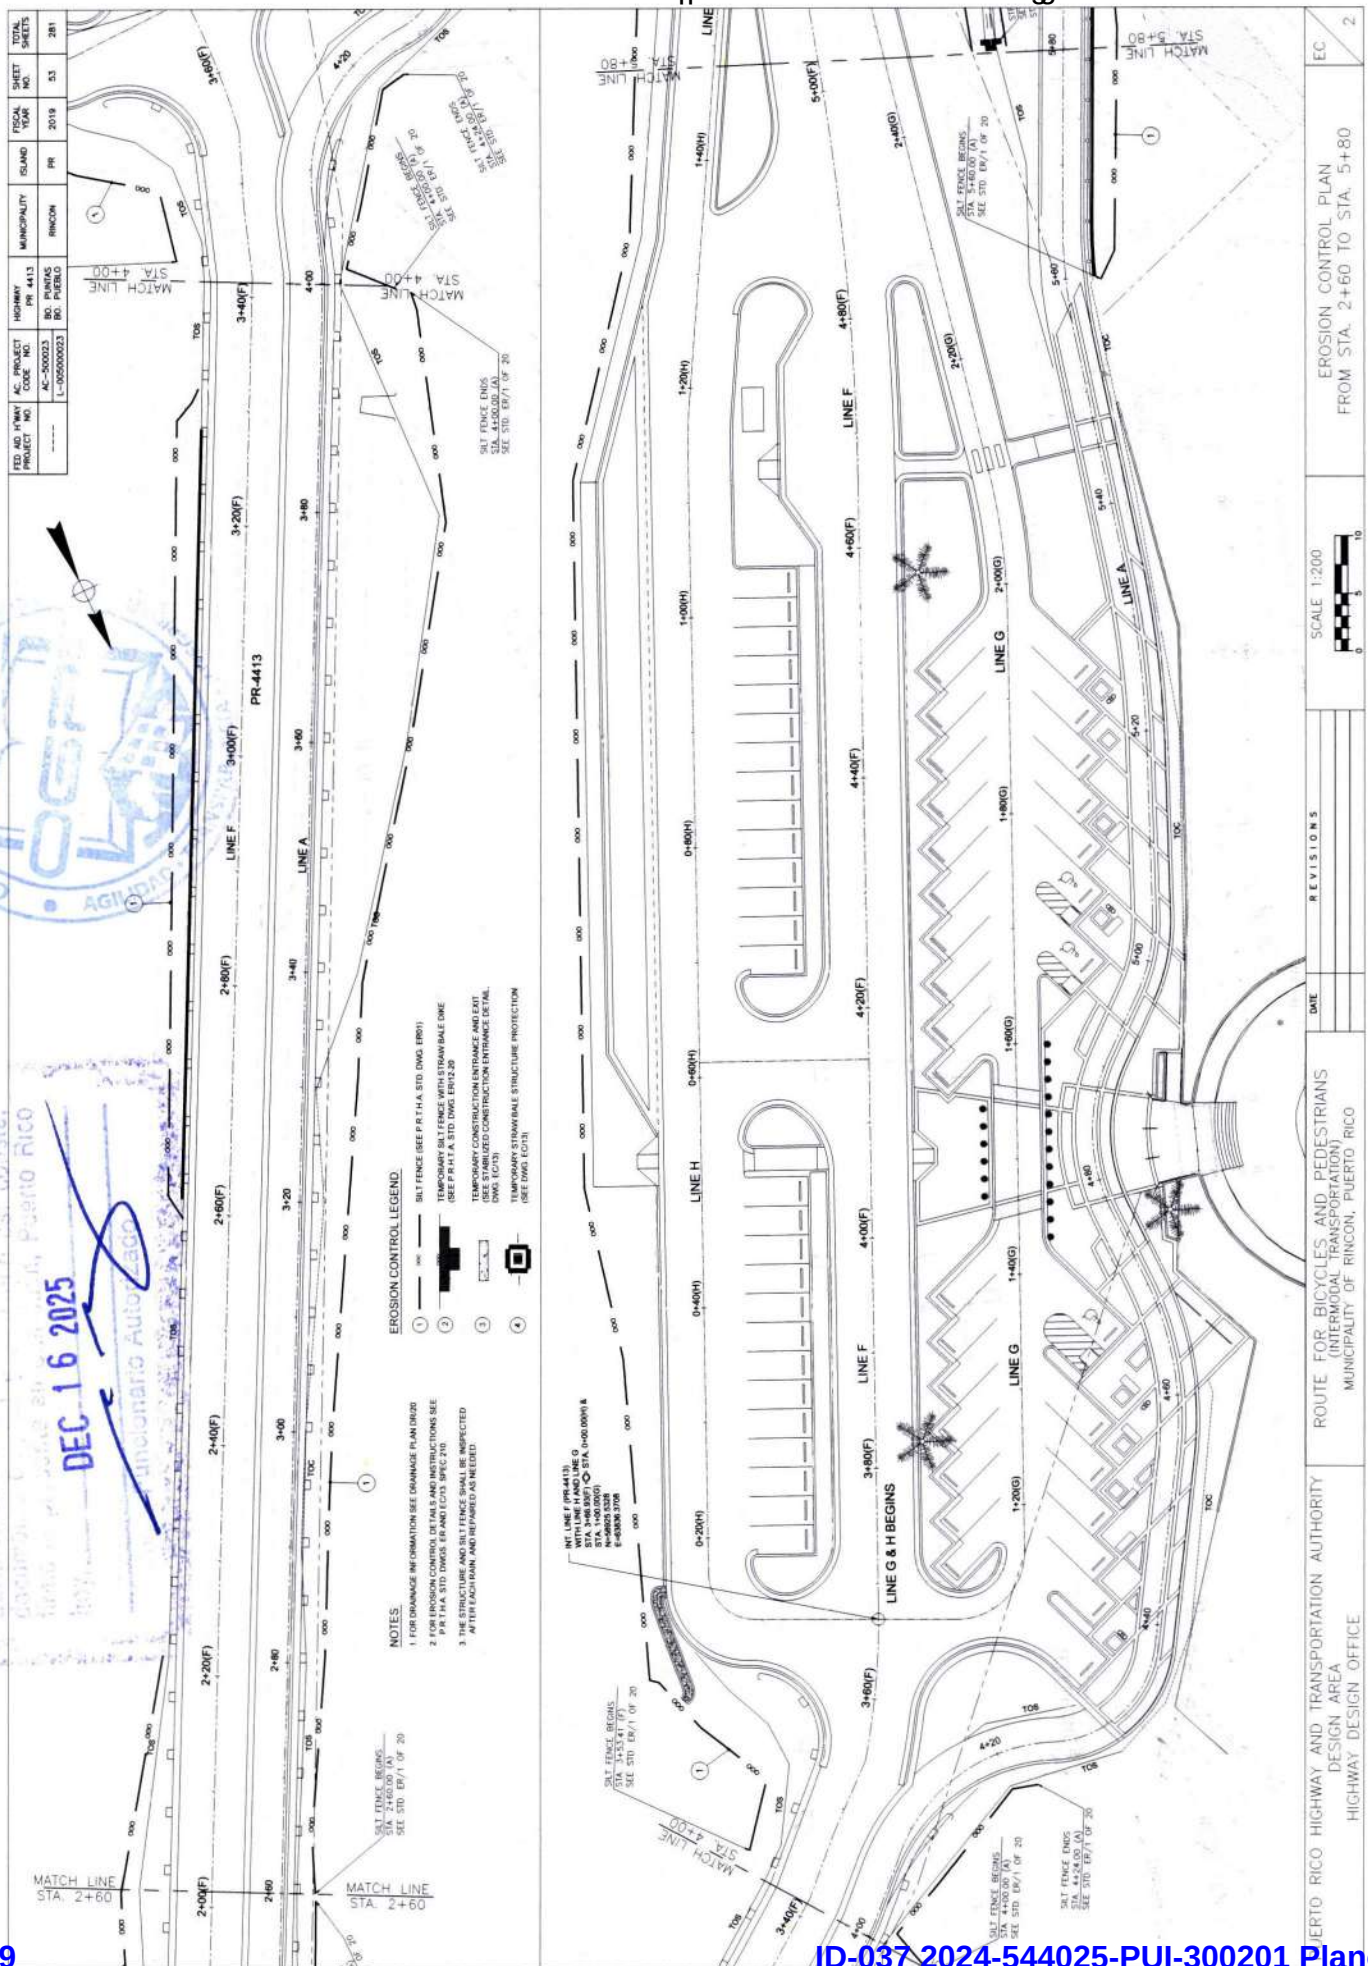


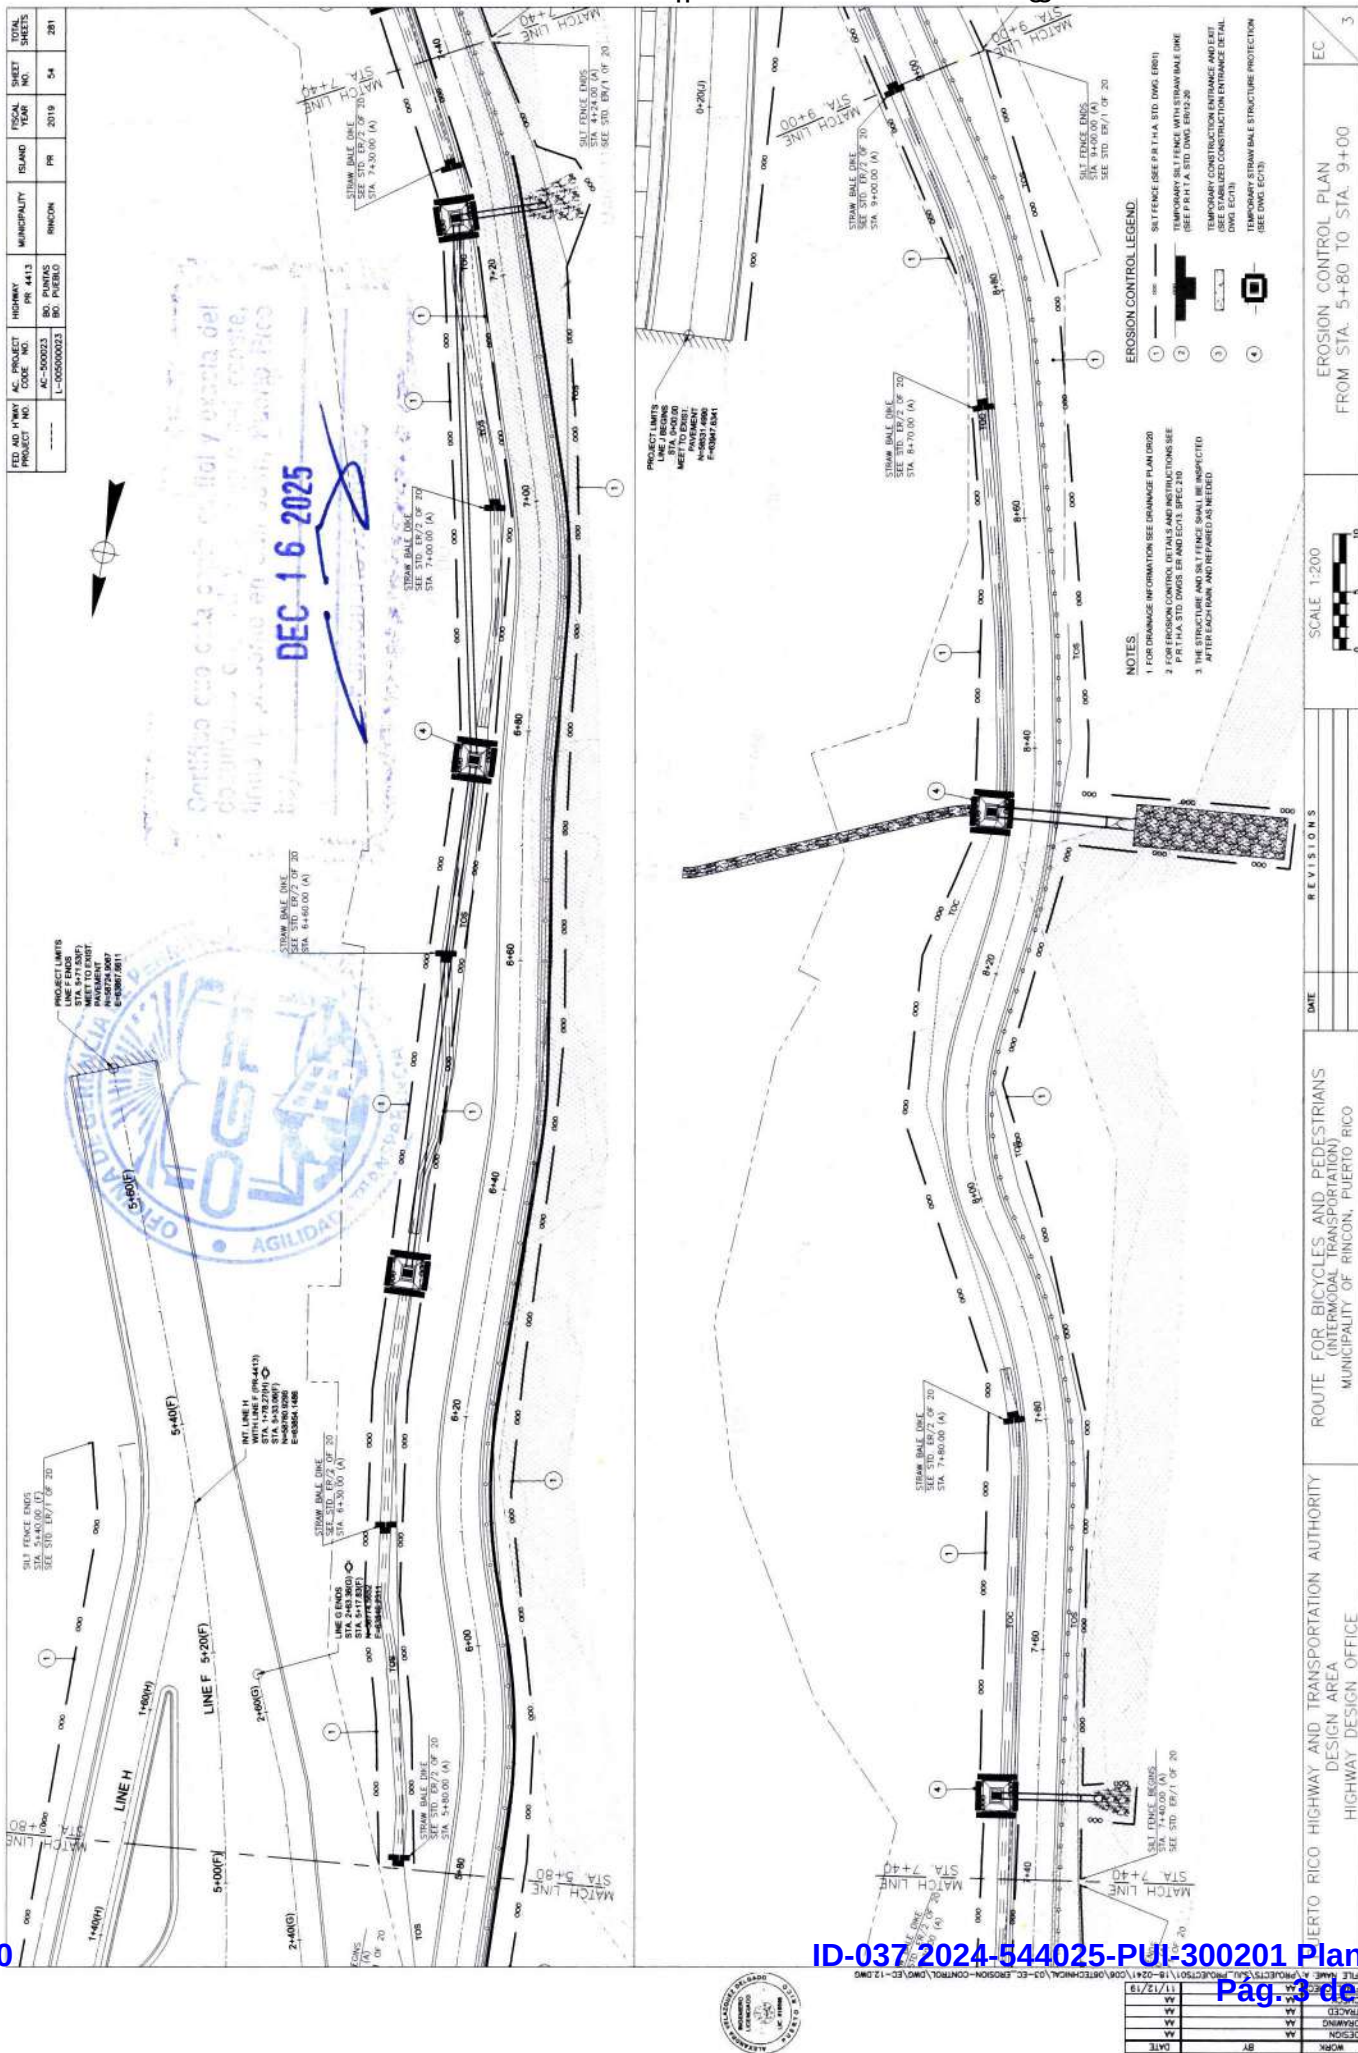


DATE	REVISIONS	SCALE 1:200	EROSION CONTROL PLAN FROM STA. 5+80 TO STA. 9+00
ROUTE FOR BICYCLES AND PEDESTRIANS (INTERMODAL TRANSPORTATION) MUNICIPALITY OF RINCON, PUERTO RICO			
PUERTO RICO HIGHWAY AND TRANSPORTATION AUTHORITY DESIGN AREA HIGHWAY DESIGN OFFICE			
Plan 3 de 7 TITLE NAME AND NUMBER PROJECT DRAWING NUMBER		EC 3	





DEC 16 2025

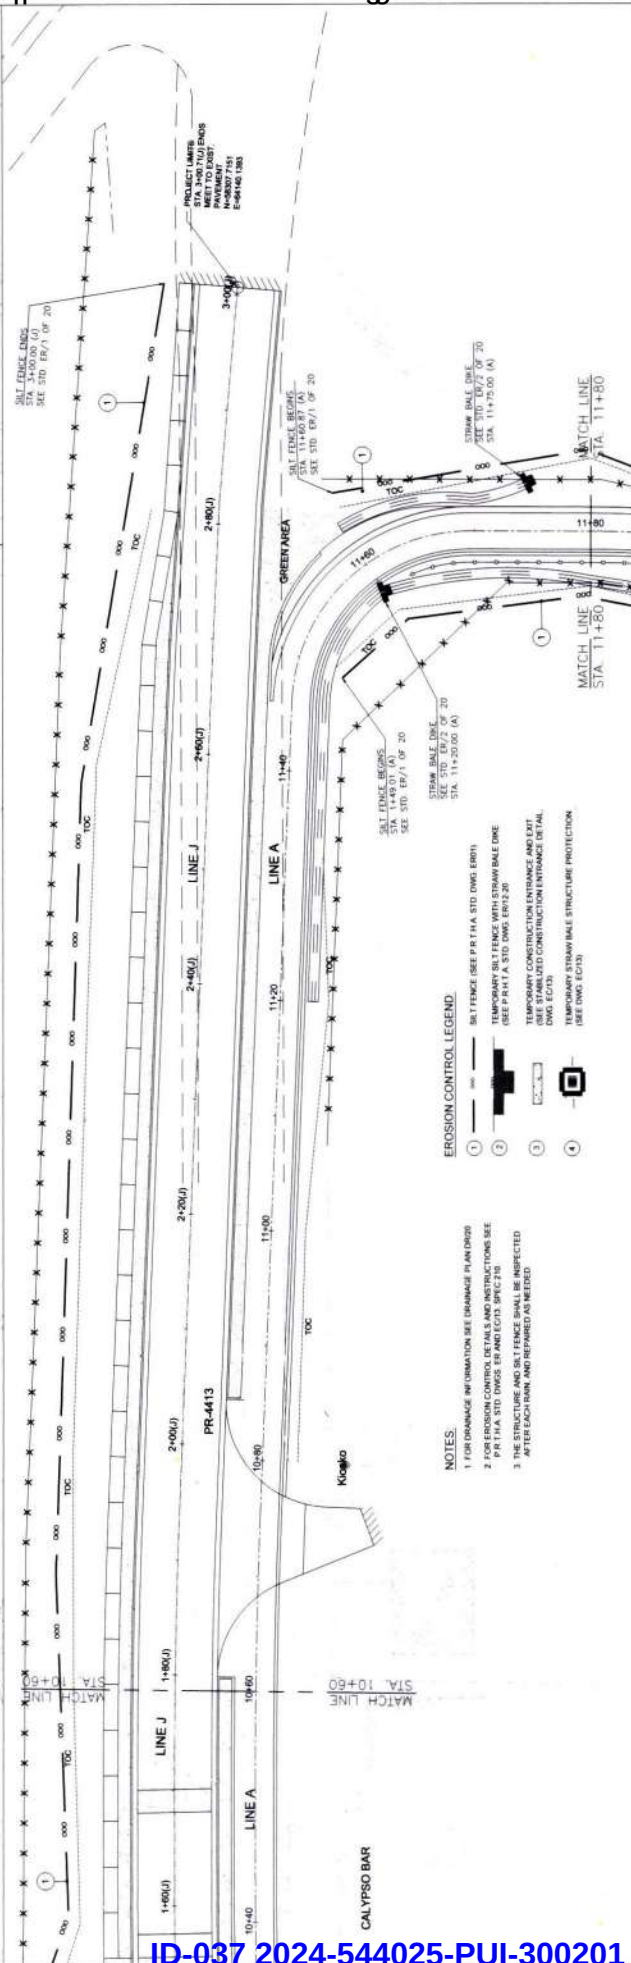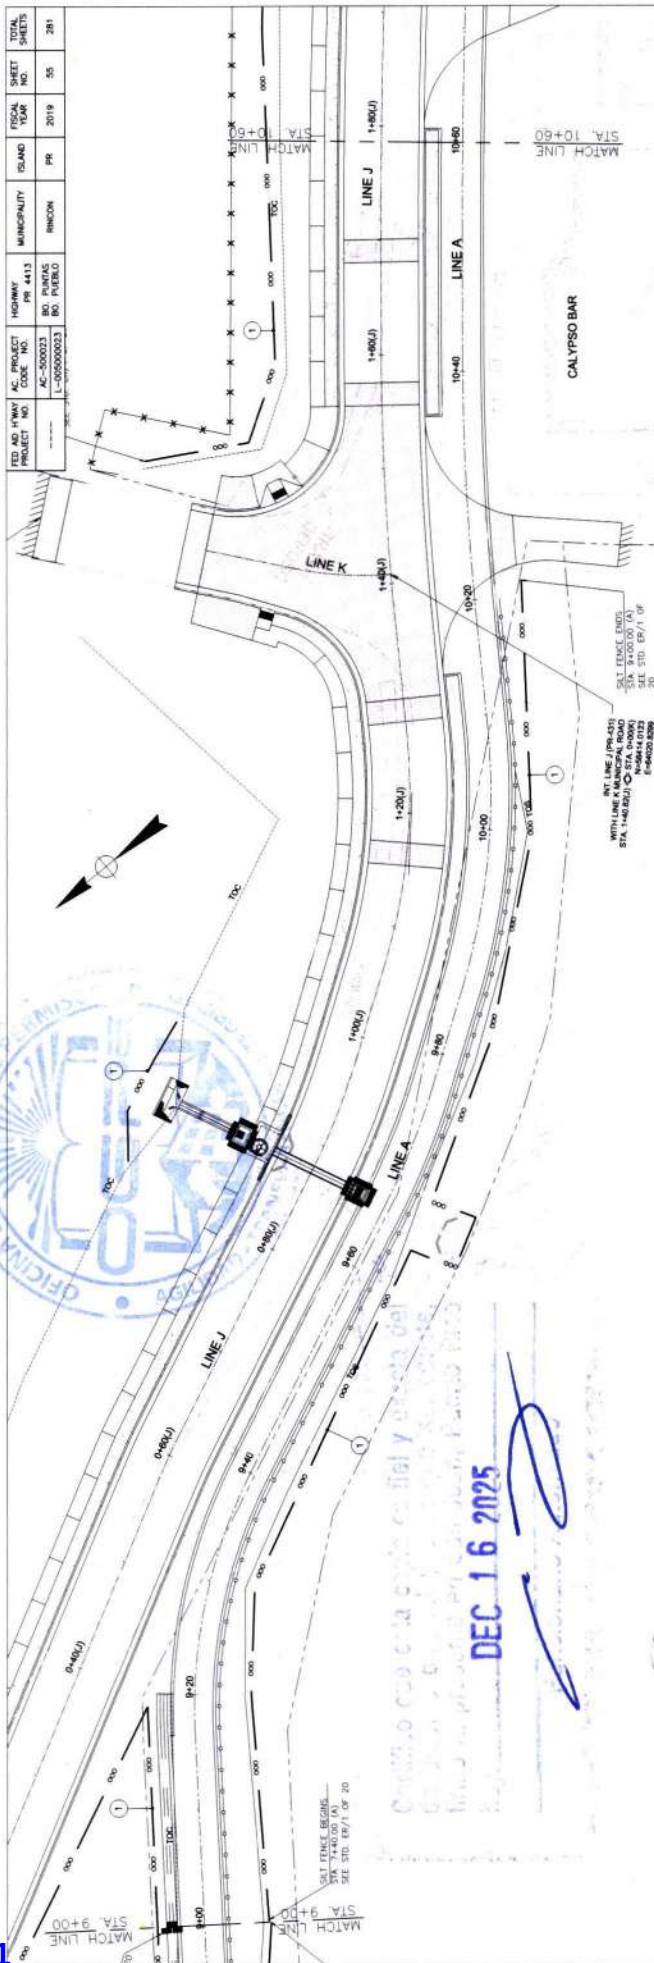

- EROSION CONTROL LEGEND**
- 1 Silt Fence (See PR 11A STD DWS ERT1)
 - 2 Temporary Silt Fence with Straw Bale Dike (See PR 11A STD DWS ERT2)
 - 3 Temporary Construction Entrance and Exit (See Standardized Construction Entrance Detail DWS ECT3)
 - 4 Temporary Straw Bale Structure Protection (See DWS ECT4)

- NOTES:**
- 1 FOR CHANGE INFORMATION SEE CHANGE PLAN ORDER
 - 2 FOR EROSION CONTROL DETAILS AND INSTRUCTIONS SEE
 - 3 PR 11A STD DWS ECT4 AND ECT5. PR 11C PR
 - 4 ALL EROSION CONTROL STRUCTURES SHALL BE INSPECTED AFTER EACH RAIN AND REPAIRED AS NEEDED

DATE		REVISIONS		EC	
ROUTE FOR BICYCLES AND PEDESTRIANS (INTERMODAL TRANSPORTATION)		EROSION CONTROL PLAN		FROM STA. 9+00 TO STA. 11+80	
MUNICIPALITY OF RINCON, PUERTO RICO		HIGHWAY DESIGN OFFICE		4	

241



DATE	BY	WORK
11/12/21	M	DESIGN
	M	TRACED
	M	SHOWN
	M	IN
	M	TO
	M	BY



Pág. 5 de



PROJECT TITLE	PUERTO RICO HIGHWAY AND TRANSPORTATION AUTHORITY DESIGN AREA HIGHWAY DESIGN OFFICE					
DATE						
REVISIONS						
SCALE	1:200					
						
EROSION CONTROL PLAN	FROM STA. 15+20 TO STA. 18+60					
EC	6					



244

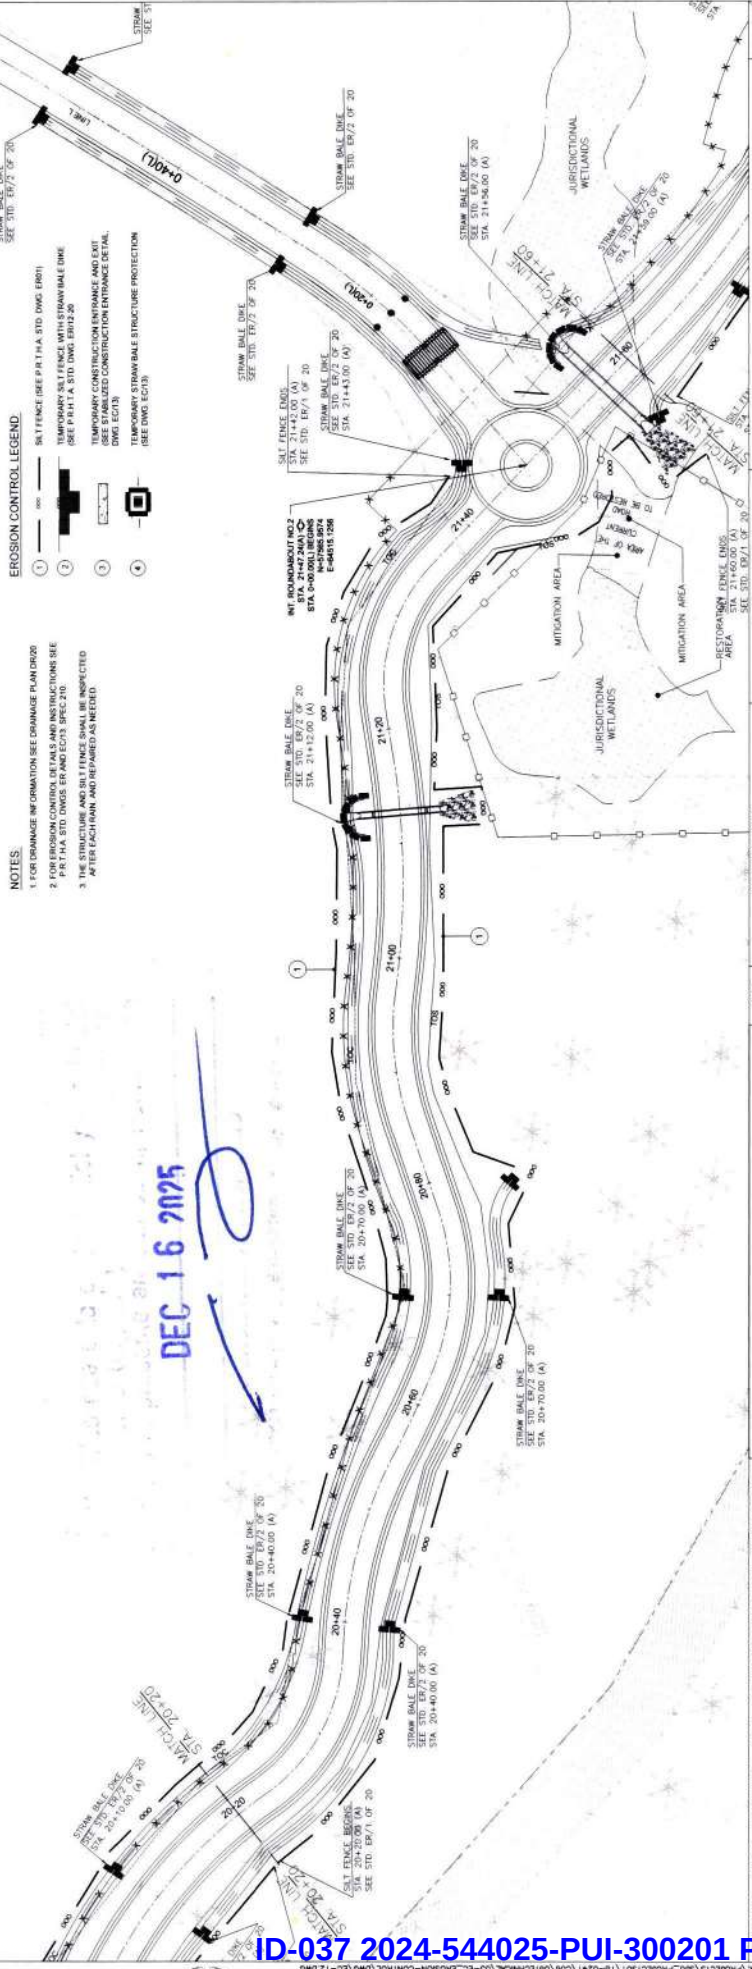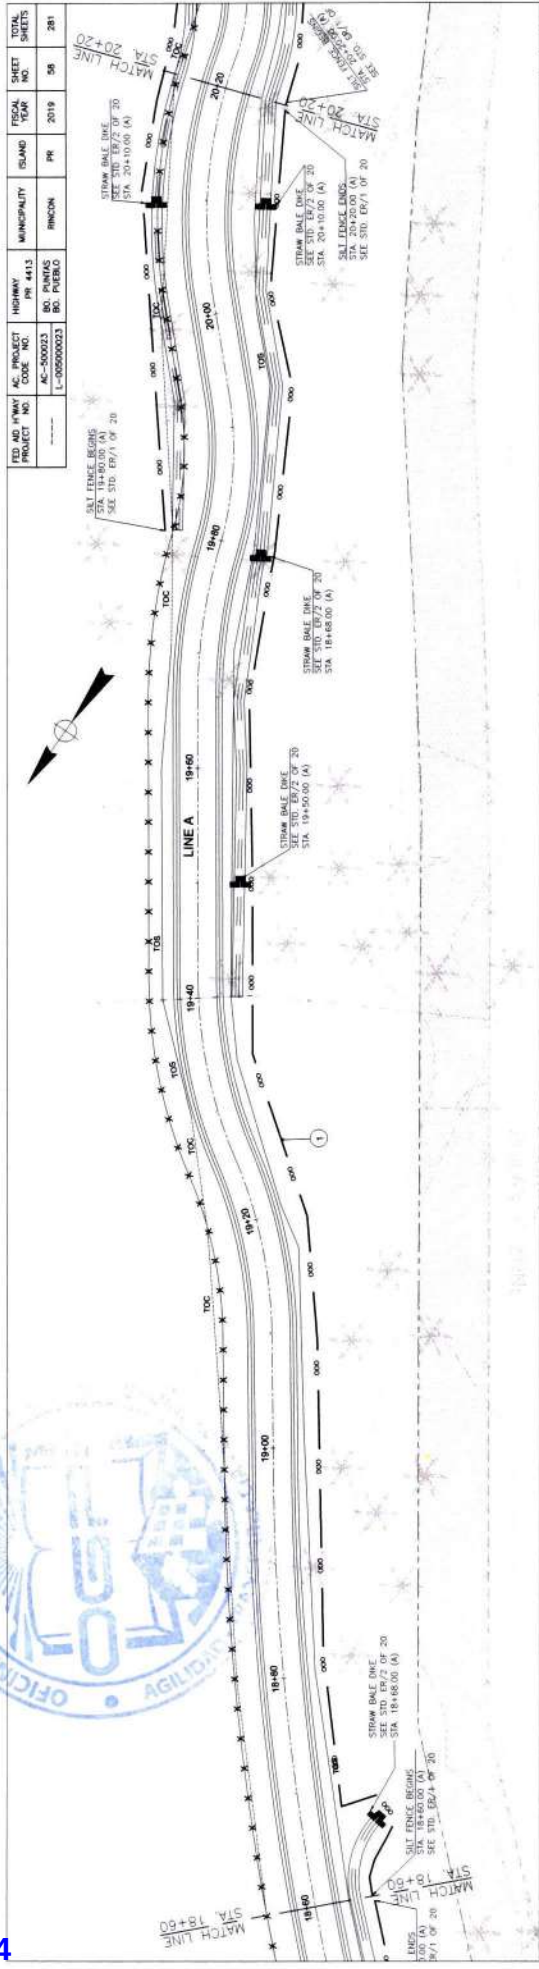

- NOTES**
- 1. FOR DRAINAGE INFORMATION SEE DRAINAGE PLAN DR20
 - 2. FOR EROSION CONTROL DETAILS AND INSTRUCTIONS SEE PRT HA STD DWG ERM AND ECT3
 - 3. THE STRUCTURE AND SALT FENCE SHALL BE INSPECTED AFTER EACH RAIN AND REPAIRED AS NEEDED
- EROSION CONTROL LEGEND**
- 1. SALT FENCE (SEE PRT HA STD DWG ERM)
 - 2. TEMPORARY SALT FENCE WITH STRAW BALE DIKE (SEE PRT HA STD DWG ERM)
 - 3. TEMPORARY CONSTRUCTION ENTRANCE DETAIL (SEE ECT3)
 - 4. TEMPORARY STRAW BALE STRUCTURE PROTECTION (SEE ECT3)


DEC 16 2025



DATE		REVISIONS	SCALE 1:200		EROSION CONTROL PLAN	
					FROM STA. 18+60 TO STA. 21+60	
					EC	
					7	

NO.	DATE	BY	WORK
1	12/12/19	MA	DESIGN
2		MA	REVISION
3		MA	REVISION
4		MA	REVISION
5		MA	REVISION
6		MA	REVISION
7		MA	REVISION

245

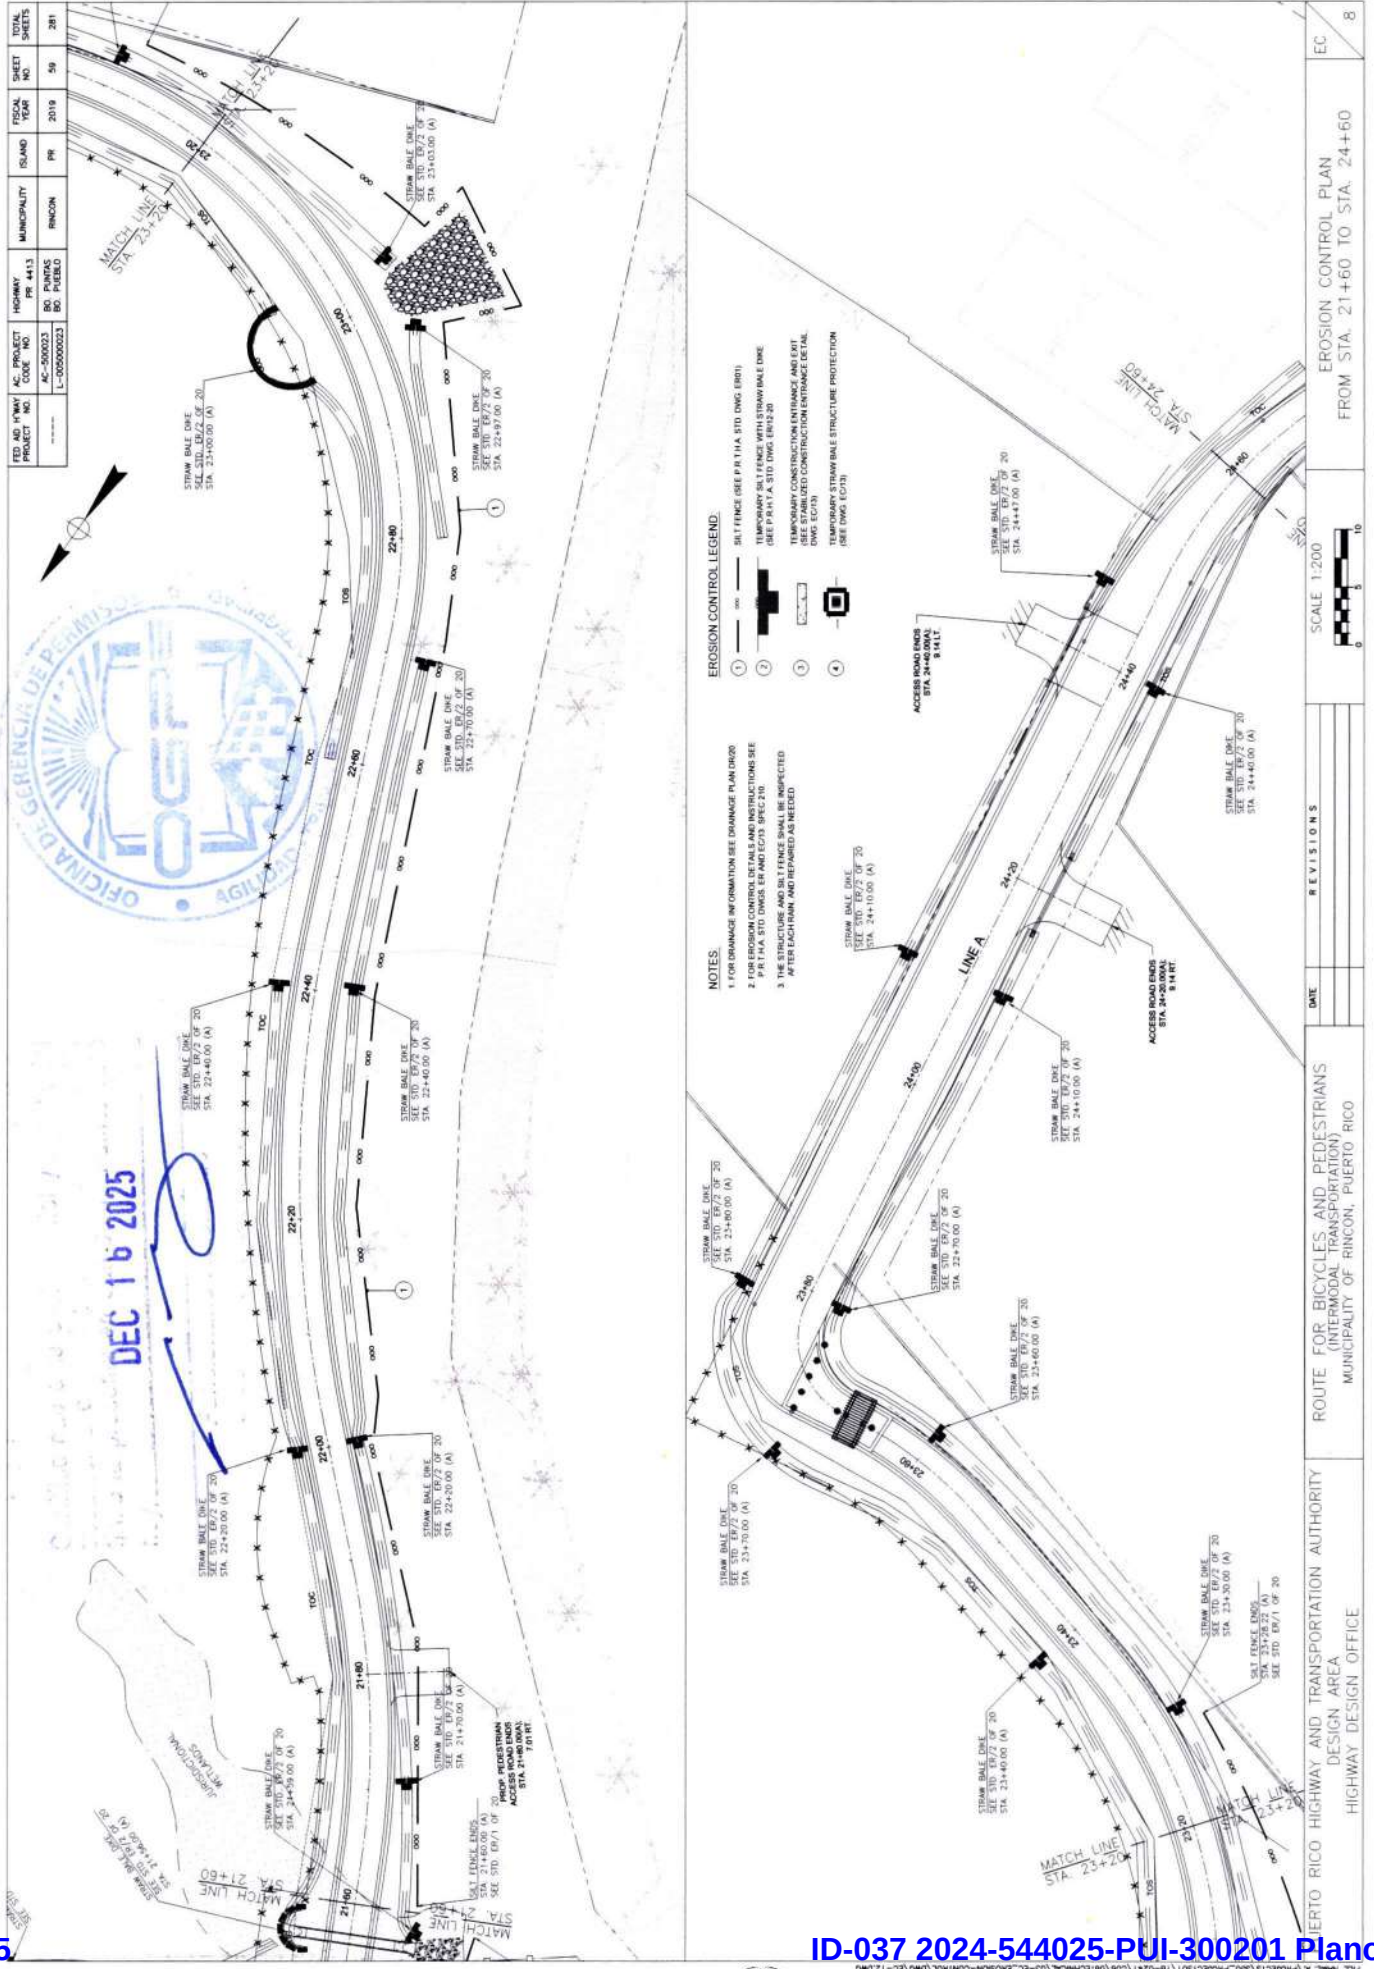






DEC 16 2025


FED. AID PROJ. NO.	AC-500023	PROJECT NO.	L-055000023	ISLAND	PR	2019	61	281
PROJECT NO.	---	PROJECT NO.	---	ISLAND	PR	2019	61	281

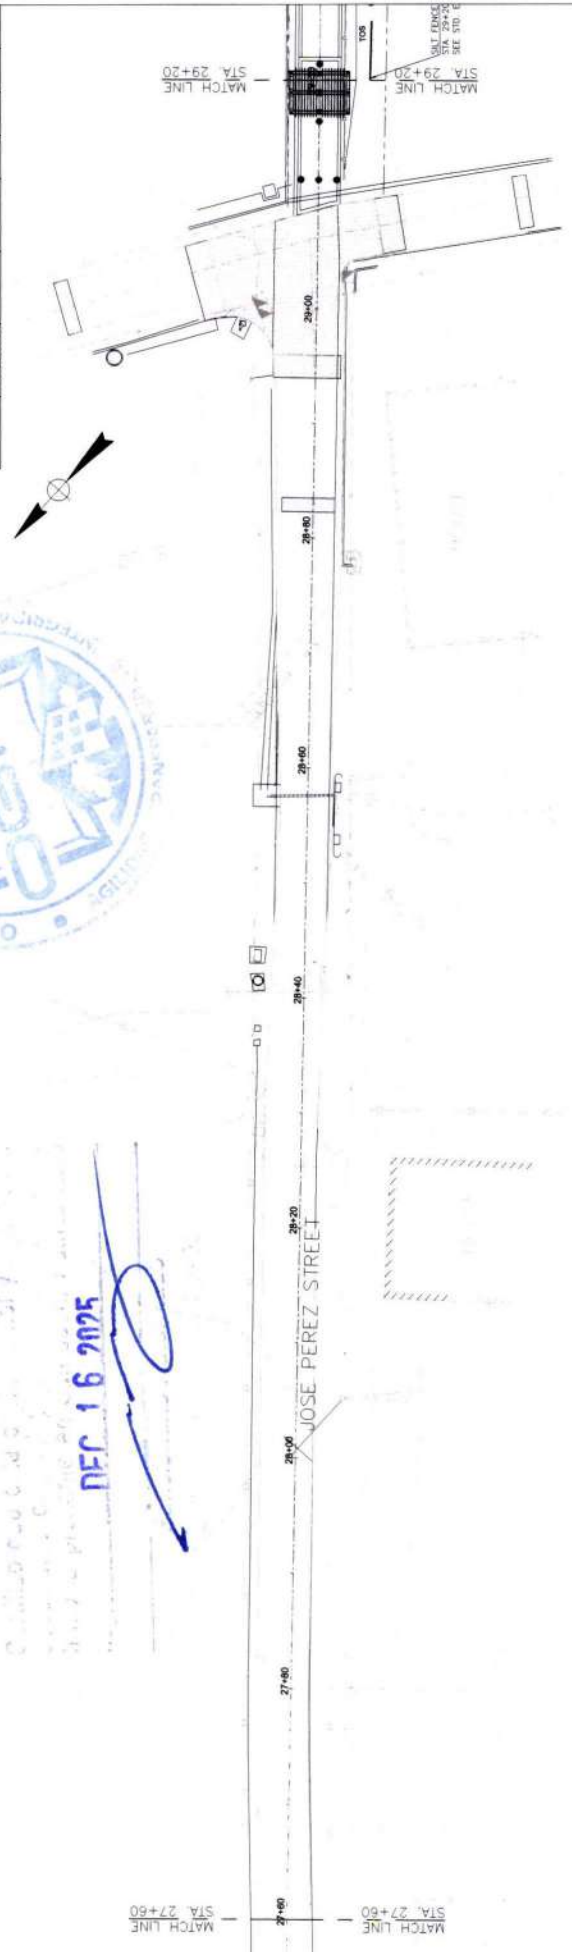

EROSION CONTROL LEGEND

- 1 SILT FENCE (SEE P.R.T.A. STD. DWG. E601)
- 2 TEMPORARY SILT FENCE WITH STRAW BALE DIKE (SEE P.R.T.A. STD. DWG. E612.20)
- 3 TEMPORARY CONSTRUCTION ENTRANCE AND EXIT (SEE STABILIZED CONSTRUCTION ENTRANCE DETAIL DWG. E671)
- 4 TEMPORARY STRAW BALE STRUCTURE PROTECTION (SEE DWG. E671)

- 1 FOR DRAINAGE INFORMATION SEE DRAINAGE PLAN (D20)
- 2 FOR EROSION CONTROL, DESIGN AND INSTALLATION SEE P.R.T.A. STD. DWGS. E6 AND E6-13 SPEC. 20
- 3 THE STRUCTURE AND SILT FENCE SHALL BE INSPECTED AFTER EACH RAIN, AND REPAIRED AS NEEDED.

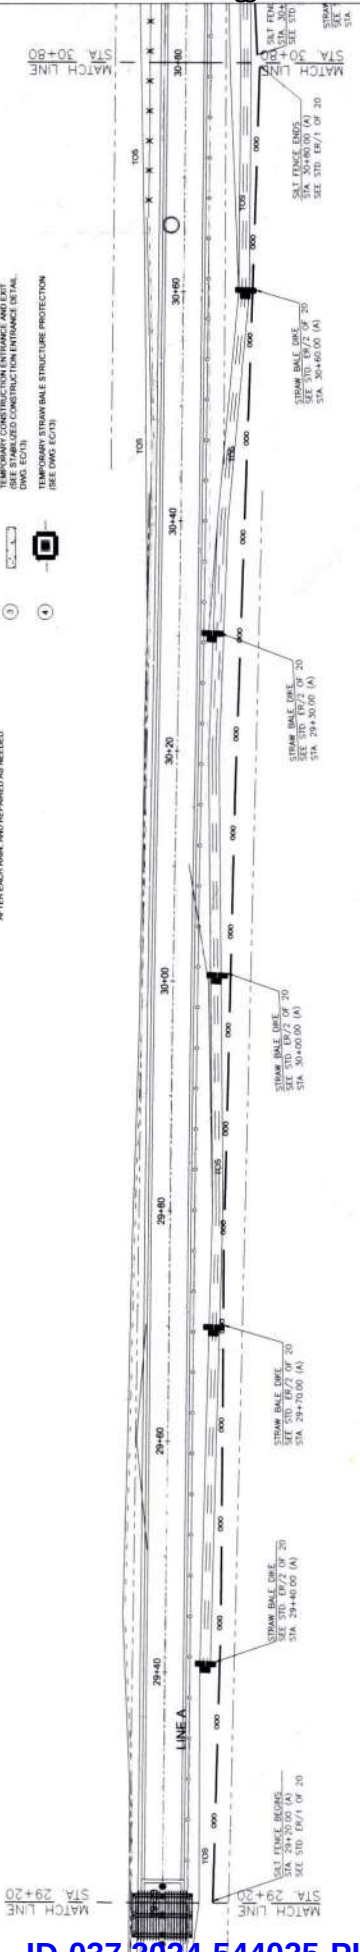


DATE	11/12/19	REVISIONS	SCALE 1:200	EC	10
ROUTE FOR BICYCLES AND PEDESTRIANS (INTERMODAL TRANSPORTATION) MUNICIPALITY OF RINCON, PUERTO RICO			EROSION CONTROL PLAN FROM STA. 27+60 TO STA. 30+80		




DATE	11/12/19
BY	MA
DESIGN	MA
CHECKED	MA
APPROVED	MA
PROJECT	MA




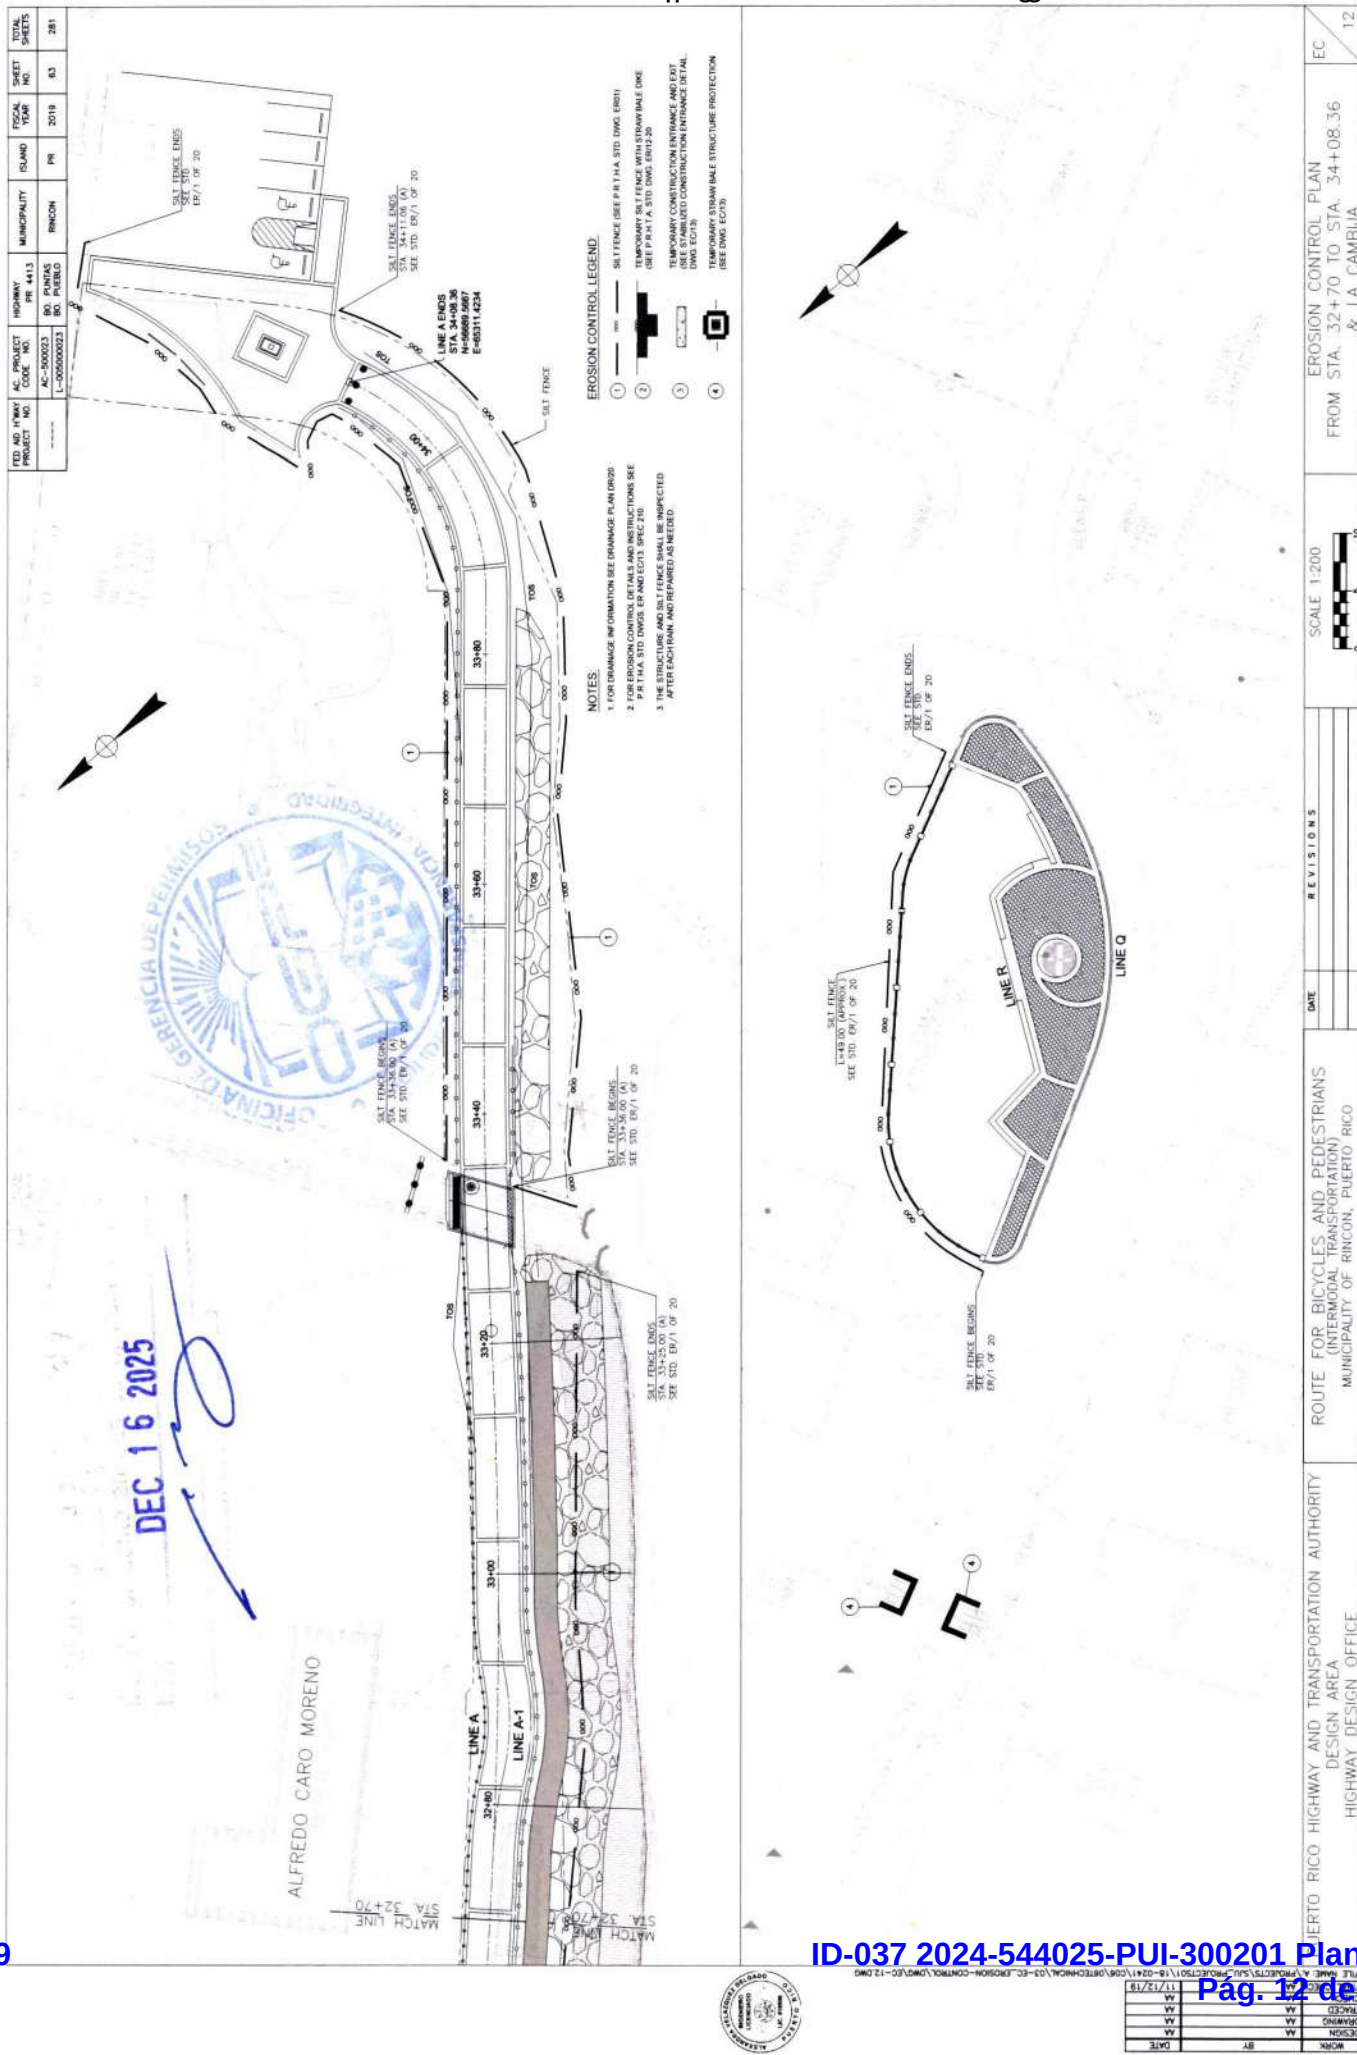

FED. AID HWY PROJECT NO.	AL. PROJECT CODE NO.	HIGHWAY PR. 4413	MUNICIPALITY	ISLAND	FISCAL YEAR	SHEET NO.	TOTAL SHEETS
-----	AC-500023	BO. PUNTA RICO	RINCON	PR	2019	64	281
	L-00000023	BO. PUNTA RICO					

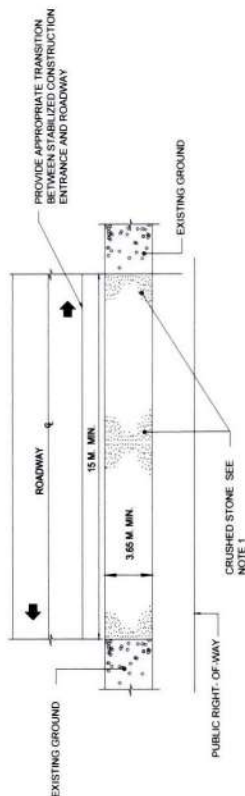

PLAN

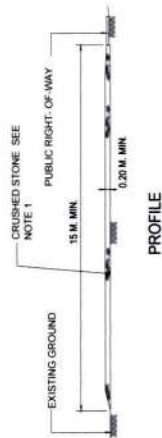


PROFILE

STABILIZED CONSTRUCTION ENTRANCE/EXIT AND TRUCK WASHING FACILITY DETAIL

NTS

STABILIZED CONSTRUCTION ENTRANCE & EXIT FOR TRUCK WASHING FACILITY - CONSTRUCTION SPECIFICATION

1. STONE SIZE - USE MSHA SIZE NO. 2 (2-2 1/2" TO 1") OR AASHTO DESIGNATION M43. SIZE NO. 2 (2-1/2" TO 1-1/2"). USE CRUSHED STONE.
2. WIDTH - NOT LESS THAN FULL WIDTH OF ALL POINTS OF INGRESS OR EGRESS.
3. WASHING - WHEN NECESSARY, WHEELS SHALL BE CLEANED TO REMOVE SEDIMENT PRIOR TO ENTRANCE INTO PUBLIC RIGHT-OF-WAY.
4. MAINTENANCE - THE ENTRANCE SHALL BE MAINTAINED TO PREVENT TRACKING OR FLOWING OF SEDIMENT INTO PUBLIC RIGHT-OF-WAY. ALL SEDIMENT SPILLED, DROPPED, WASHED OR TRACKED INTO PUBLIC RIGHT-OF-WAY MUST BE REMOVED IMMEDIATELY.

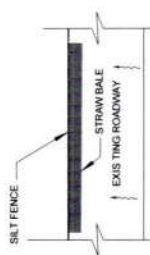

TEMPORARY SILT FENCE WITH STRAW BALE DIKE

NTS

Anchor Bales With 2'-2 1/2"x4' Staples Per Bale



TEMPORARY STRAW BALE PROTECTION AROUND INLET

NTS



DEC 16 2025

Handwritten signature and date stamp.

DATE	REVISIONS	NOT TO SCALE	SOIL EROSION AND SEDIMENT CONTROL DETAILS	EC
				13

PUERTO RICO HIGHWAY AND TRANSPORTATION AUTHORITY
DESIGN AREA
HIGHWAY DESIGN OFFICE

ROUTE FOR BICYCLES AND PEDESTRIANS
(INTERMODAL TRANSPORTATION)
MUNICIPALITY OF RINCON, PUERTO RICO