



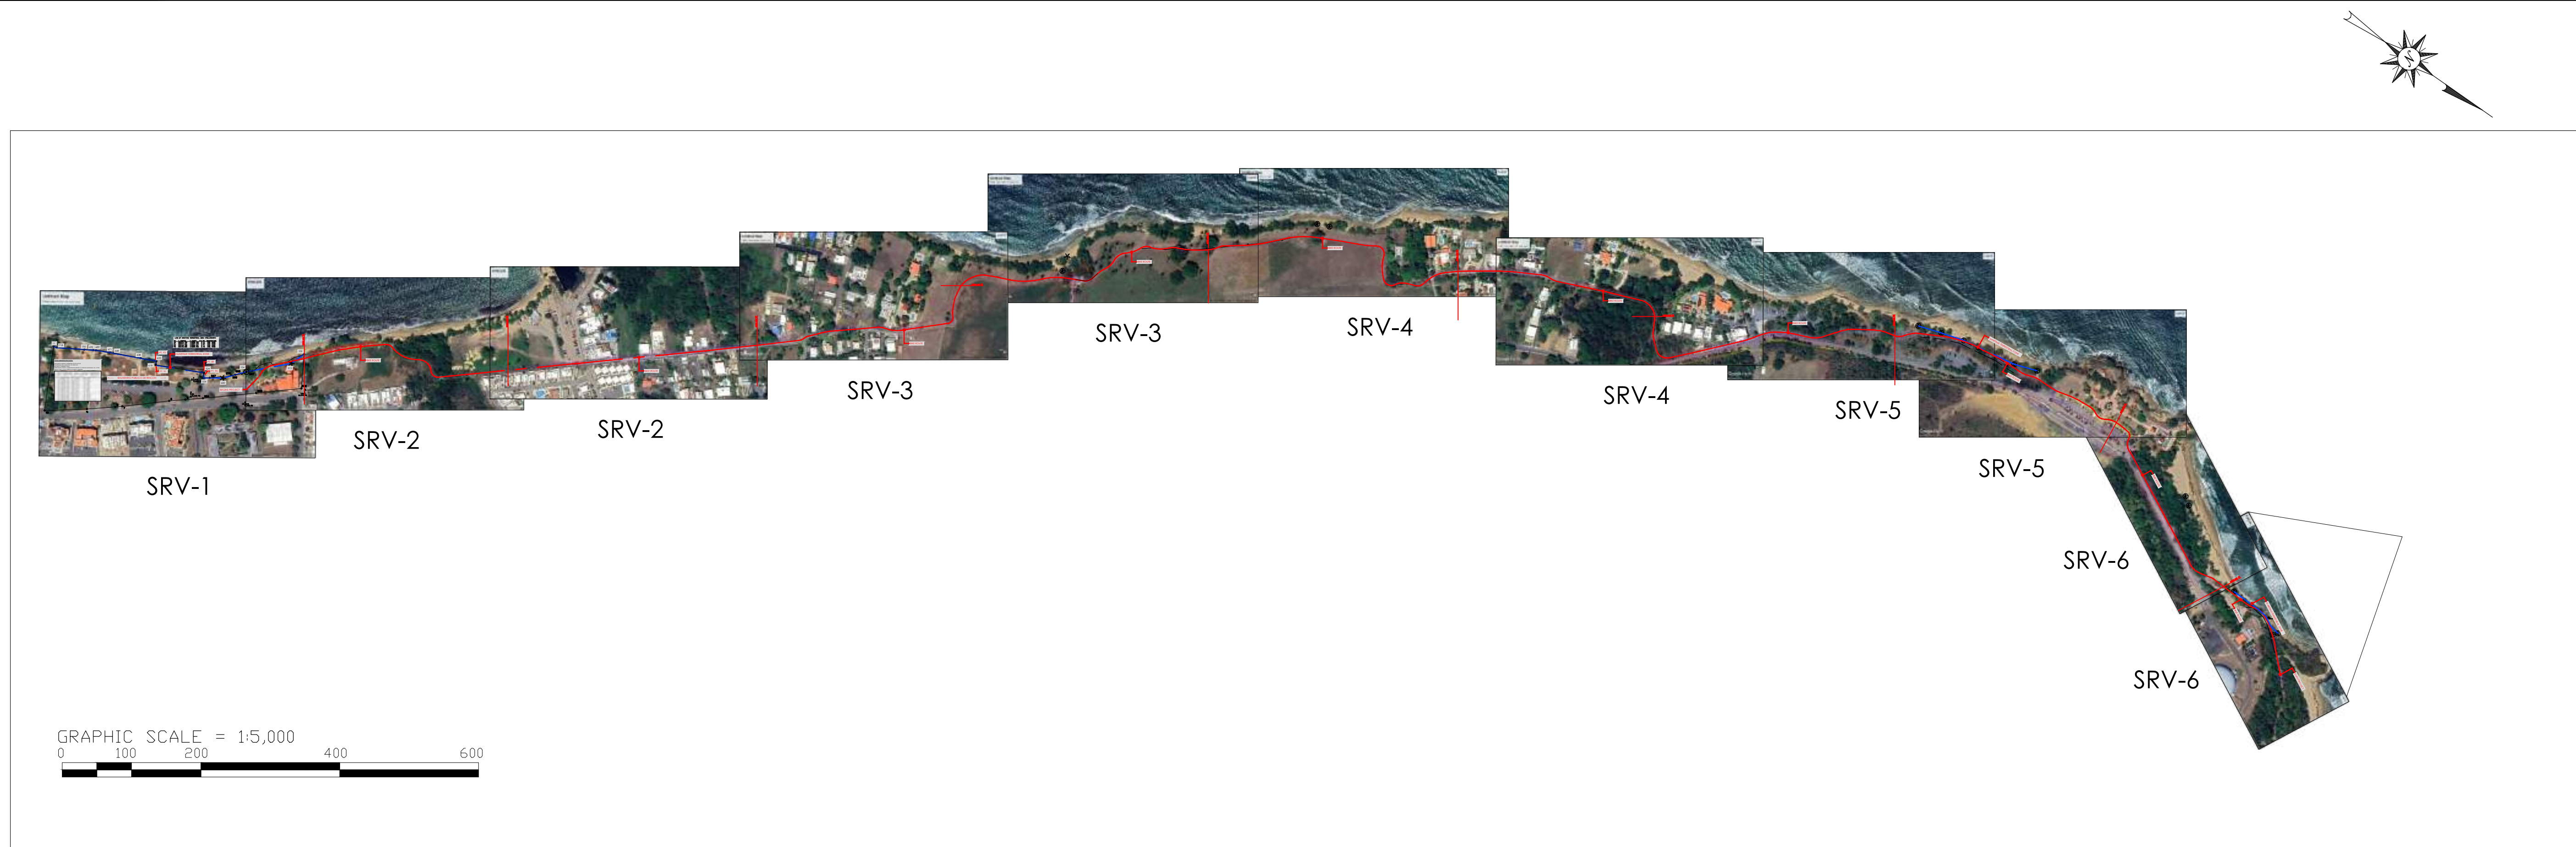

MASTER SITE PLAN
SCALE= 1:5,000

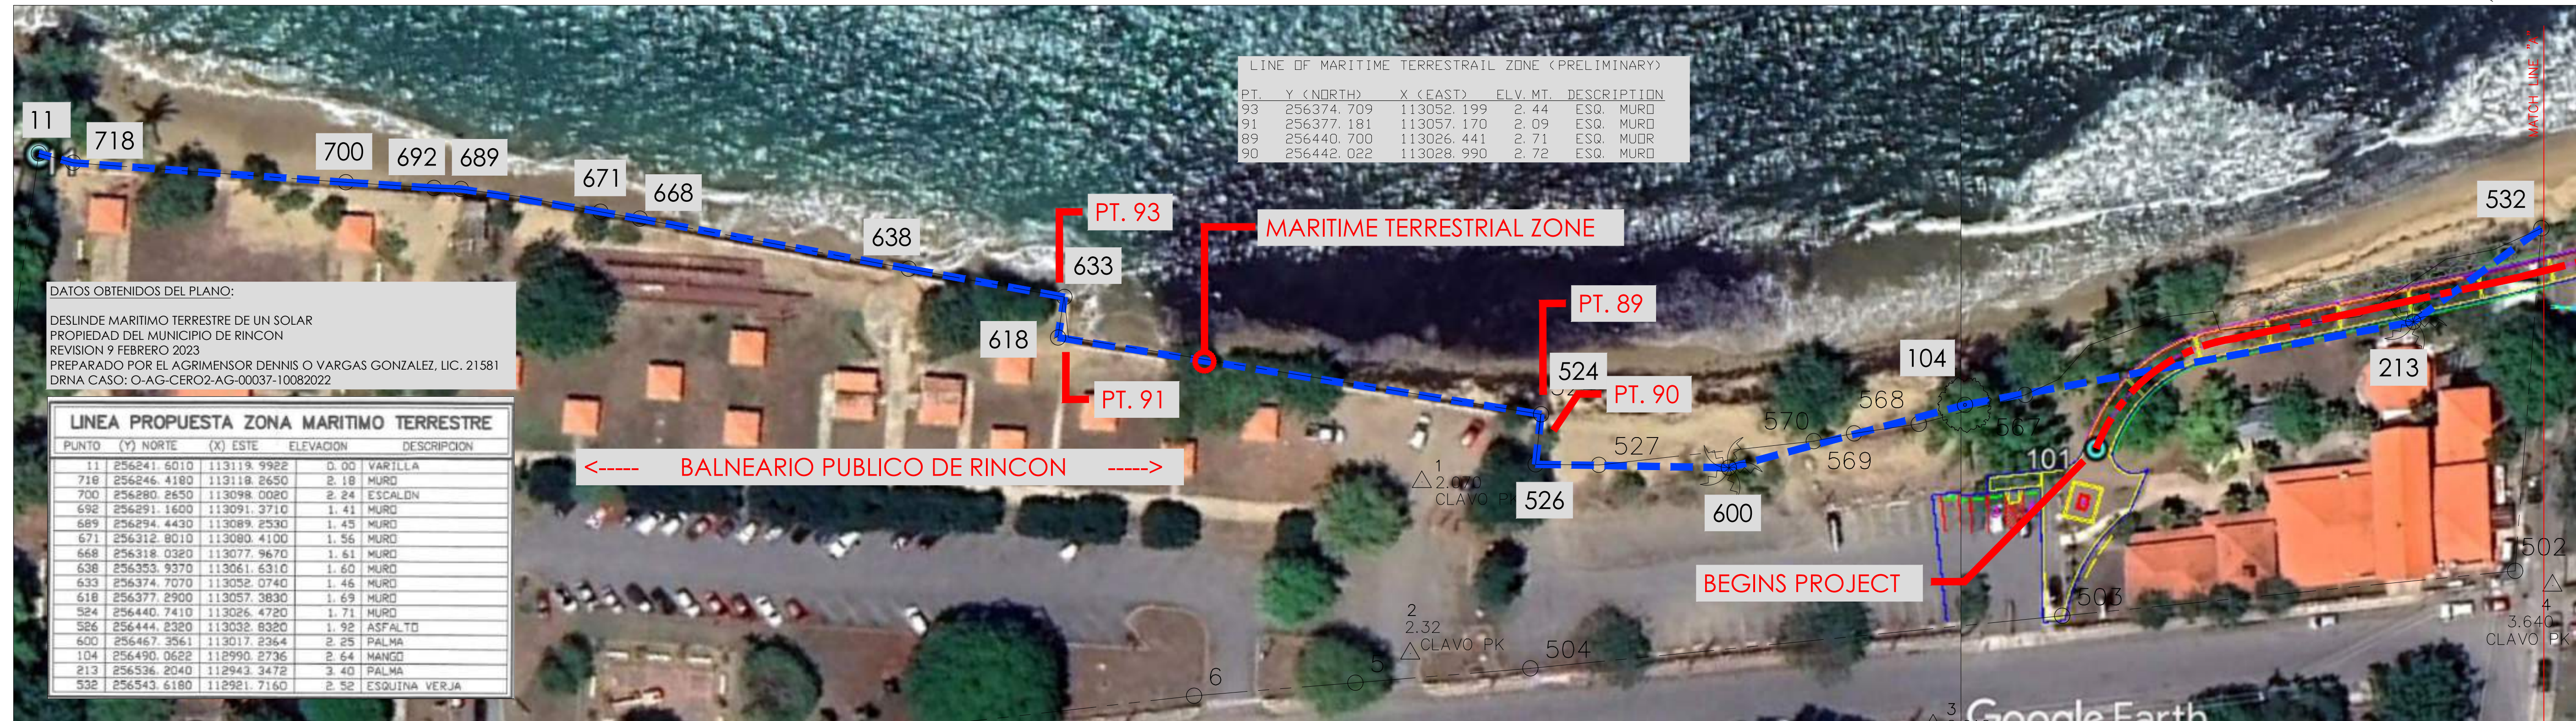

SITE PLAN
SCALE= 1:500

Surveyor Notes:


1. HORIZONTAL CONTROLS AREA TIED TO THE STATE PLANE COORDINATE SYSTEM NAD83 NA2011 EPOCH 2010, USING A GNSS ANTENNA TRIMBLE R-6 CONNECTED TO A VIRTUAL REFERENCE STATION.
2. VERTICAL CONTROLS ARE PRVD02 HORTOMETRIC HEIGH GEOD18 (PUERTO RICO) USING A GNSS ANTENNA TRIMBLE R-6 CONNECTED TO A VIRTUAL REFERENCE STATION
3. FIELD WORKS WERE PERFORMED USING A TOTAL INSTRUMENT TRIMBLE M3 IN SEVERAL SUNNY DAYS DURING APRIL 24, 2025
4. ALL DISTANCE A ELEVATION ARE EXPRESSED IN THE METRIC UNITS SYSTEM, EXCEPT FOR PIPE DIAMETERS THAT ARE EXPRESSED IN INCHES.
5. SPOT ELEVATIONS REFER TO SPECIFIC COORDINATES; HOWEVER, CONTOUR LINES ONLY INDICATE THE GENERAL BEHAVIOR OF THE TERRAIN AND ARE GENERATED BY INTERPOLATION OF THE DATA COLLECTED ON THE FIELD.

Surveyor's Certification :

The undersigned, registered surveyors license no. 5615 authorized to exercise his profession in Puerto Rico does hereby certify that the plot hereon drawn is a true representation of the existing conditions.


Survey Performed By:

Gerardo R. Cerra Ortiz
Surveyor Lic. no. 5615
Dated: JANUARY 15, 2026

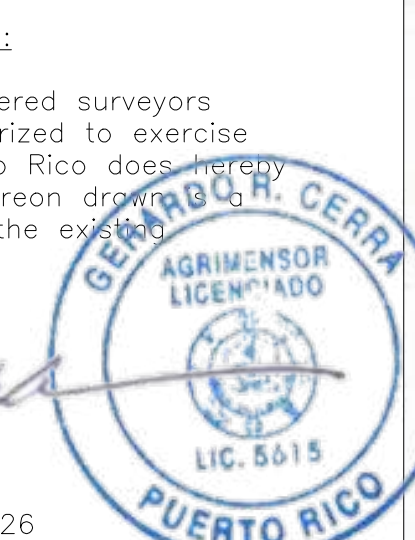

STUDY OF THE MARITIME TERRESTRAIL ZONE OF
RINCON BICYCLE AND PEDESTRIAN TRAIL

MUNICIPALITY OF RINCON, PUERTO RICO

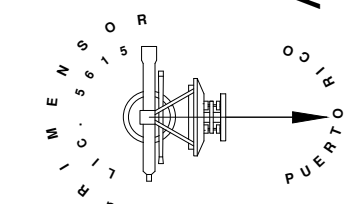

Agrim. Gerardo Cerra Ortiz

REVISIONS DATE

SHEET NAME

SITE PLAN

SCALE: 1:500
PROJECT & FILE No. 25-04
DESIGNED BY:
DRAWN BY: V. LÓPEZ
DATE: JUNE 5, 2025
SHEET NO. 1 OF 6
DRAWING NO. SRV-1



SITE PLAN
SCALE= 1:500



SITE PLAN
SCALE= 1:500



AGRICULTOR
GERARDO R. CERRA
PUERTO RICO

Agrim. Gerardo Cerra Ortiz

STUDY OF THE MARITIME TERRESTRIAL ZONE OF RINCON BICYCLE AND PEDESTRIAN TRAIL

MUNICIPALITY OF RINCON, PUERTO RICO


REVISIONS	DATE
-----------	------

SHEET NAME

SITE PLAN

SCALE:	1: 500	SHEET NO.
PROJECT & FILE No.	25-04	2
DESIGNED BY:		OF
		6
DRAWN BY:	V. LOPEZ	DRAWING NO.
DATE:	JUNE 5, 2025	SRV-2



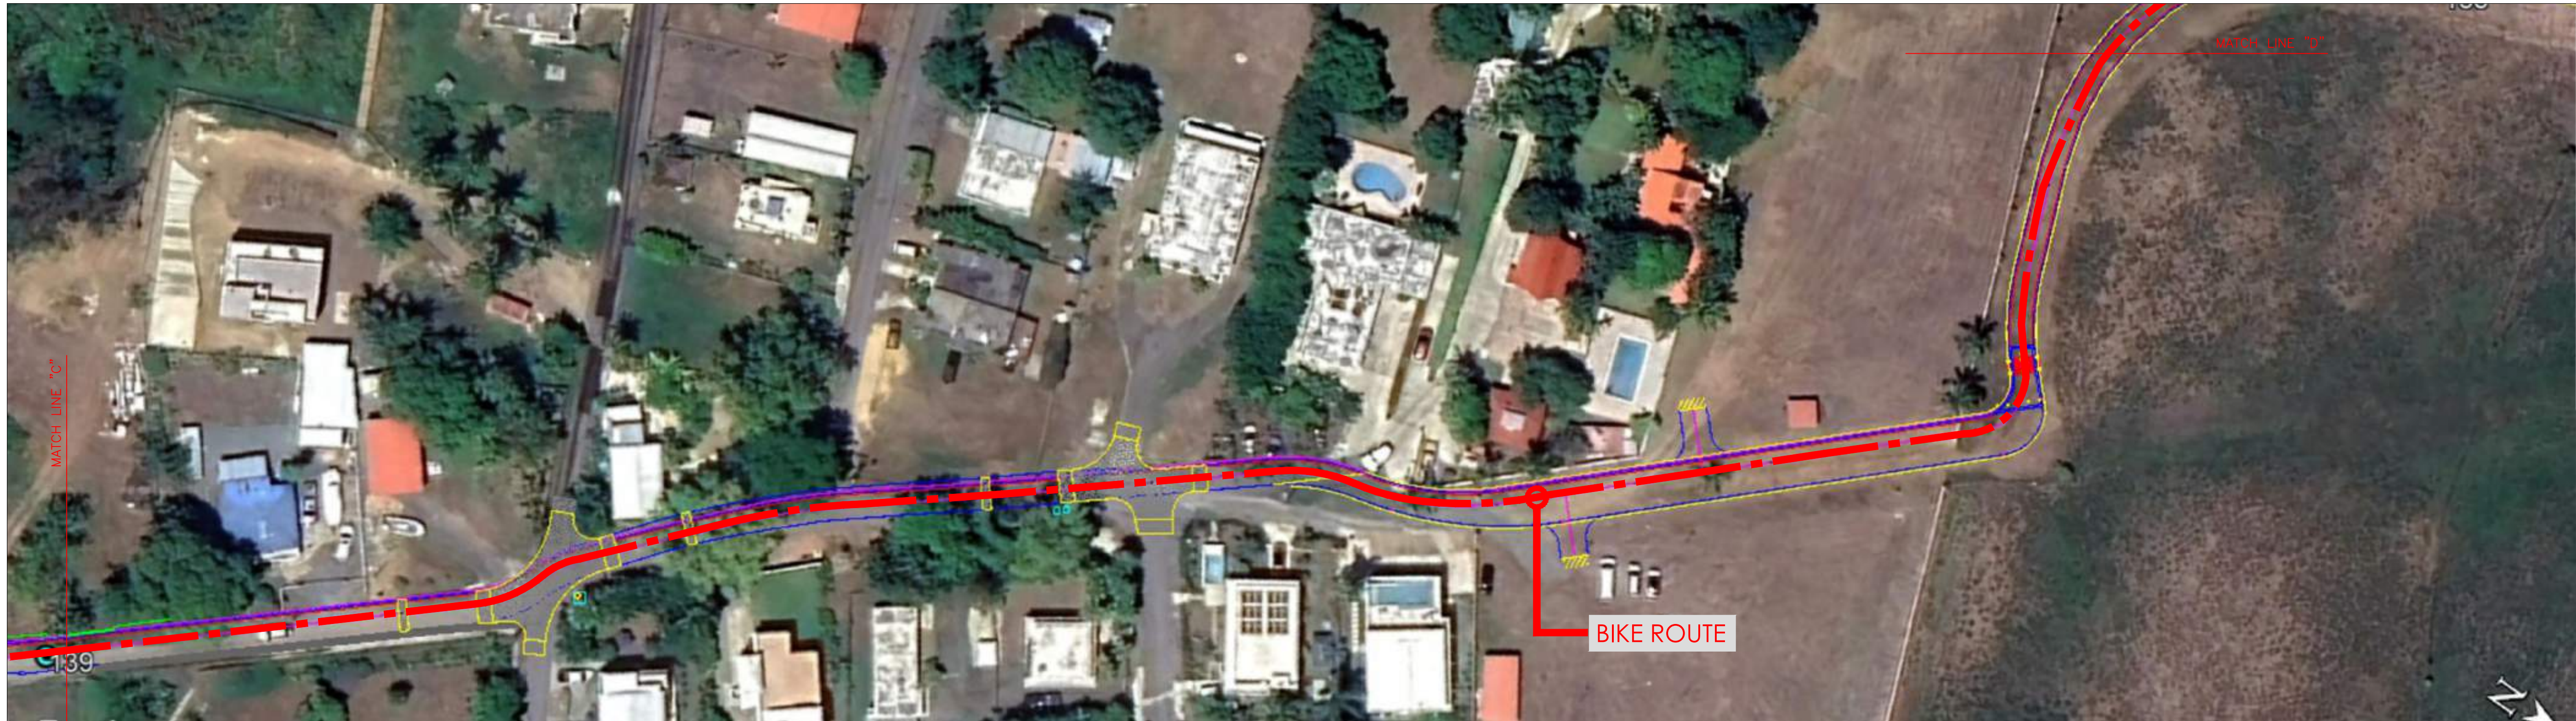

SITE PLAN
SCALE= 1:500



SITE PLAN
SCALE= 1:500



REVISIONS	DATE
-----------	------

SHEET NAME

SITE PLAN

SCALE:	1:500	SHEET NO.	3
PROJECT & FILE NO.	25-04	OF	6
DESIGNED BY:		DRAWING NO.	SRV-3
DRAWN BY:	V. LOPEZ		
DATE:	JUNE 5, 2025		

Gerardo R. Cerra

GERARDO R. CERRA
AGRICULTOR
LICENCIADO
LIC. 5615
PUERTO RICO



SITE PLAN
SCALE= 1:500



SITE PLAN
SCALE= 1:500



AGRICULTOR
GERARDO R. CERRA
LIC. 5015
PUERTO RICO

Agrim. Gerardo Cerra Ortiz

STUDY OF THE MARITIME TERRESTRIAL ZONE OF RINCON BICYCLE AND PEDESTRIAN TRAIL

MUNICIPALITY OF RINCON, PUERTO RICO

REVISIONS	DATE

SHEET NAME

SITE PLAN

SCALE: 1:500
PROJECT & FILE No. 25-04


DESIGNED BY:
DRAWN BY: V. LÓPEZ

DATE: JUNE 5, 2025

SHEET NO.
4
OF
6
DRAWING NO.
SRV-4



SITE PLAN
SCALE= 1:500

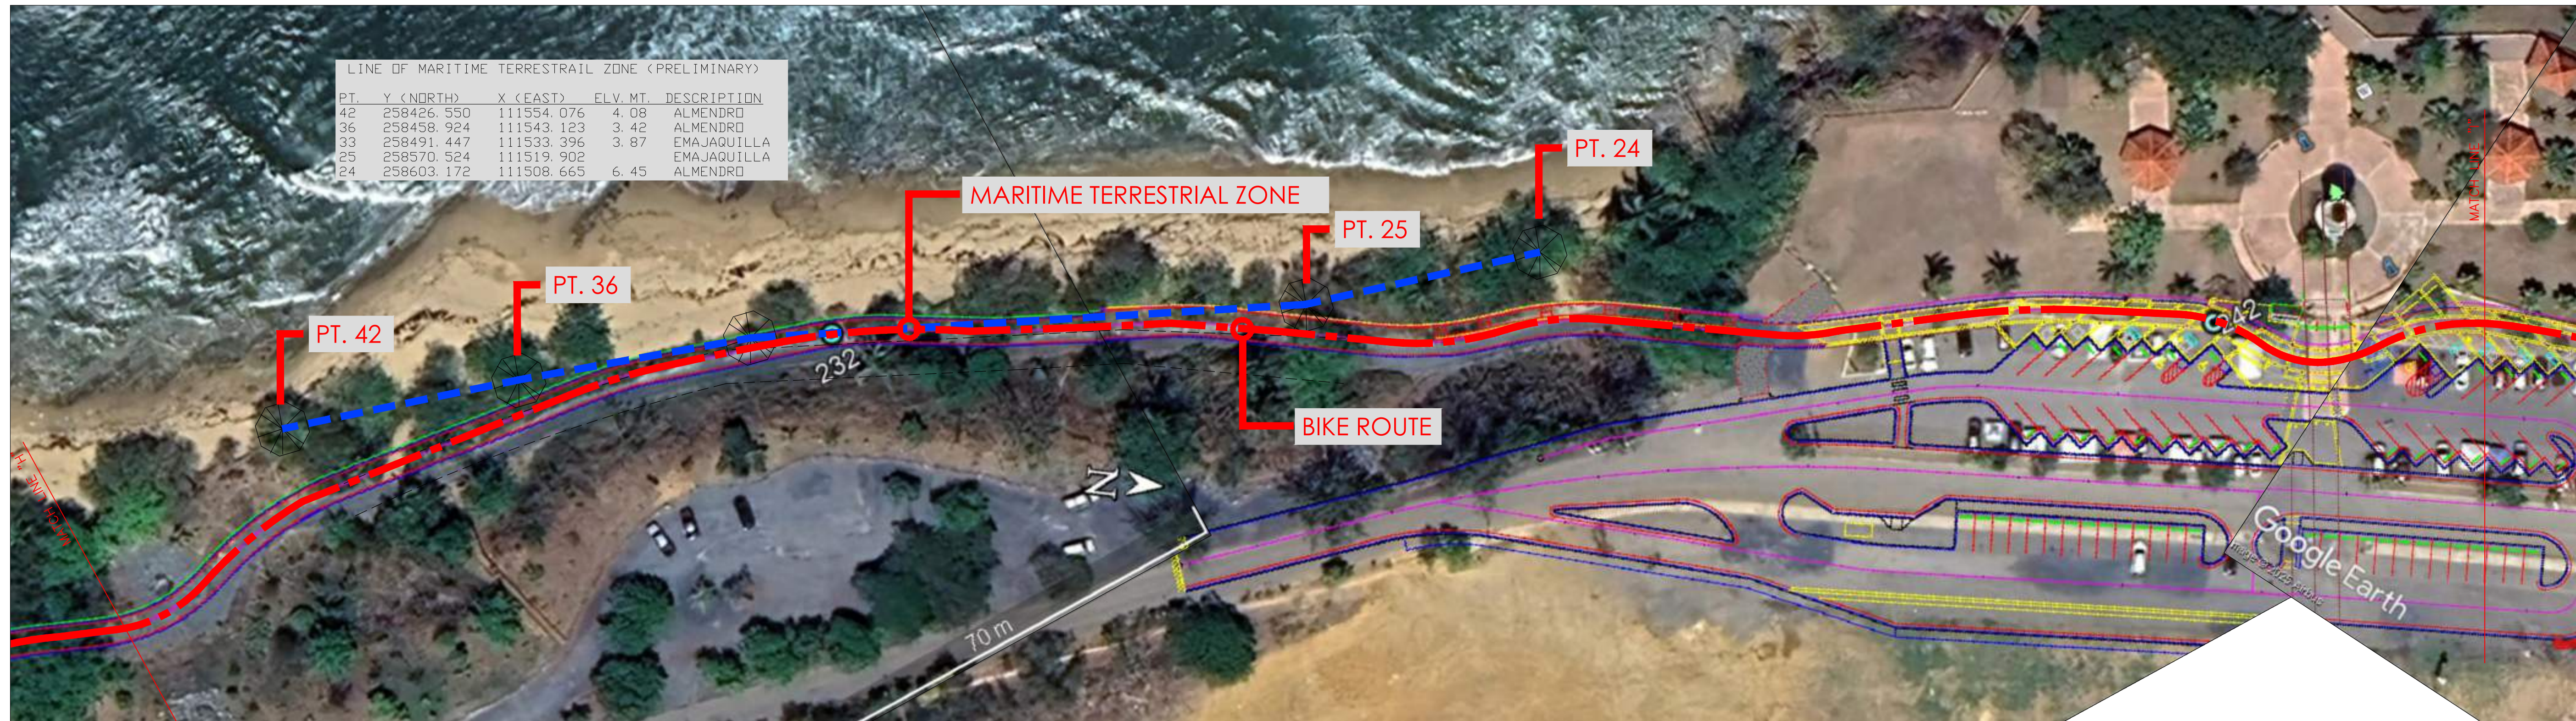

SITE PLAN
SCALE= 1:500



STUDY OF THE MARITIME TERRESTRIAL ZONE OF RINCON BICYCLE AND PEDESTRIAN TRAIL

MUNICIPALITY OF RINCON, PUERTO RICO

REVISIONS DATE

SHEET NAME

SITE PLAN

SCALE: 1:500
PROJECT & FILE No. 25-04
SHEET NO. 5 OF 6
DESIGNED BY: V. LÓPEZ
DRAWN BY: V. LÓPEZ
DATE: JUNE 5, 2025
SRV-5



SITE PLAN
SCALE= 1:500



SITE PLAN
SCALE= 1:500



STUDY OF THE MARITIME TERRESTRIAL ZONE OF RINCON BICYCLE AND PEDESTRIAN TRAIL

MUNICIPALITY OF RINCON, PUERTO RICO

REVISIONS	DATE
-----------	------

SHEET NAME

SITE PLAN

SCALE: 1:500

PROJECT & FILE No. 25-04

DESIGNED BY:
V. LÓPEZ

DRAWN BY: V. LÓPEZ

DATE: JUNE 5, 2025

SHEET NO.

6

OF

6

DRAWING NO.

SRV-6