


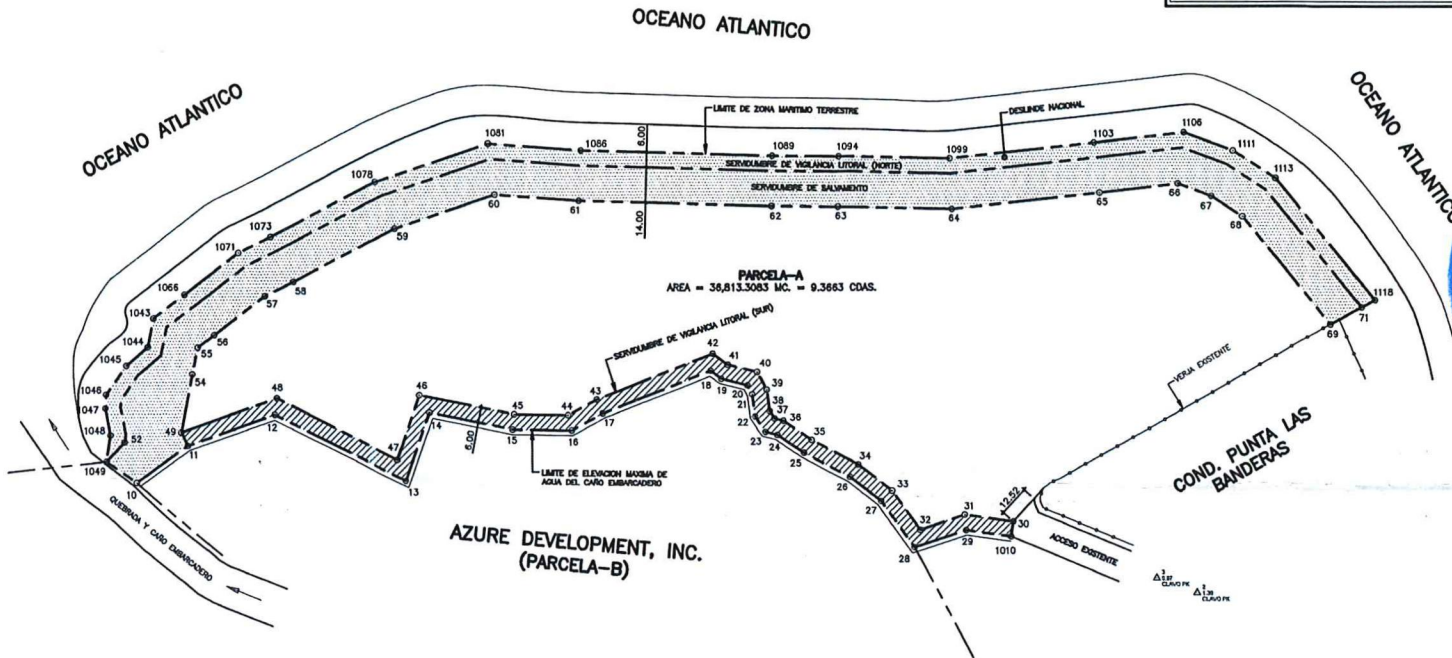

PLANO DE MENSURA Y DESLINDE DE LA Z.M.T.

DE LA PARCELA-A, PROPIEDAD DE AZURE DEVELOPMENT, INC, UBICADA EN EL BO. MATA DE PLATANO, SECTOR PUNTA LA BANDERA AVENIDA OCEAN DRIVE DEL TERMINO MUNICIPAL DE LUQUILLO, PR.

NUMERO DE CASO: 0-AG-CER02-PO-00038-2912022



DATOS DE MENSURA						
DE SERVIDUMBRE DE VIGILANCIA LITORAL (SUR)						
PUNTO	LINEA	DISTANCIA	RAMBO	(Y) NORTE	(X) ESTE	DESCRIPCION
30	30-31	18.550	N 81°48'45" W	281565.127	275170.2108	VARILLA
31	31-32	18.814	S 71°34'15" W	281559.133	275182.2465	VARILLA
32	32-33	19.301	N 30°41'15" W	281574.8003	275141.0508	VARILLA
33	33-34	17.237	N 51°49'53" W	281585.4527	275127.4550	VARILLA
34	34-35	21.175	N 61°07'37" W	281586.3360	275108.7278	VARILLA
35	35-36	13.658	N 58°08'23" W	281602.8581	275097.3623	VARILLA
36	36-37	3.657	N 76°21'35" W	281603.8024	275083.8287	VARILLA
37	37-38	3.577	N 38°33'15" W	281608.8010	275091.8811	VARILLA
38	38-39	8.609	N 07°32'35" W	281615.3352	275090.7210	VARILLA
39	39-40	2.555	N 27°11'15" W	281622.3483	275087.0248	VARILLA
40	40-41	12.370	N 76°28'53" W	281635.5487	275074.9781	VARILLA
41	41-42	7.548	N 54°19'51" W	281628.8008	275068.8548	VARILLA
42	42-43	50.482	S 62°05'20" W	281605.2534	275021.7660	VARILLA
43	43-44	13.237	S 62°05'20" W	281605.2534	275021.0670	VARILLA
44	44-45	21.237	N 88°54'23" W	281605.8784	274986.2330	VARILLA
45	45-46	38.030	N 78°32'45" W	281613.1286	274948.8806	VARILLA
46	46-47	27.058	S 18°39'13" W	281587.8110	274940.8671	VARILLA
47	47-48	53.659	N 63°12'30" W	281612.2333	274992.7003	VARILLA
48	48-49	40.768	S 70°57'01" W	281598.9290	274854.1664	VARILLA
49	49-50	8.991	S 28°38'30" W	281593.9370	274884.7590	VARILLA
50	50-51	37.118	N 70°47'50" W	281605.1240	274981.8100	VARILLA
51	51-52	58.680	S 83°25'25" W	281579.5160	274944.2400	VARILLA
52	52-53	28.870	N 19°28'15" W	281606.5190	274953.8830	VARILLA
53	53-54	34.381	S 78°32'45" W	281599.8890	274887.2790	VARILLA
54	54-55	23.835	S 88°59'23" W	281599.3470	275011.5100	VARILLA
55	55-56	10.846	S 88°59'23" W	281604.0000	275008.0850	VARILLA
56	56-57	16.833	N 68°52'43" W	281622.9120	275087.9840	VARILLA
57	57-58	8.678	S 34°12'31" W	281618.7100	275072.4280	VARILLA
58	58-59	10.841	N 78°28'53" W	281617.1700	275062.8650	VARILLA
59	59-60	4.171	S 27°51'15" W	281613.4280	275084.9140	VARILLA
60	60-61	7.315	S 37°33'15" W	281604.8390	275088.0850	VARILLA
61	61-62	2.838	S 37°33'15" W	281604.8390	275088.0850	VARILLA
62	62-63	7.315	S 37°33'15" W	281604.8390	275088.0850	VARILLA
63	63-64	4.338	S 78°28'53" W	281597.3800	275084.9140	VARILLA
64	64-65	12.843	S 88°59'23" W	281600.2070	275102.0240	VARILLA
65	65-66	20.814	S 88°59'23" W	281600.2070	275102.0240	VARILLA
66	66-67	20.814	S 88°59'23" W	281600.2070	275102.0240	VARILLA
67	67-68	15.833	S 88°59'23" W	281600.2070	275102.0240	VARILLA
68	68-69	15.833	S 88°59'23" W	281600.2070	275102.0240	VARILLA
69	69-70	15.833	S 88°59'23" W	281600.2070	275102.0240	VARILLA
167	167-168	15.833	S 88°59'23" W	281600.2070	275102.0240	VARILLA
168	168-169	15.833	S 88°59'23" W	281600.2070	275102.0240</	